
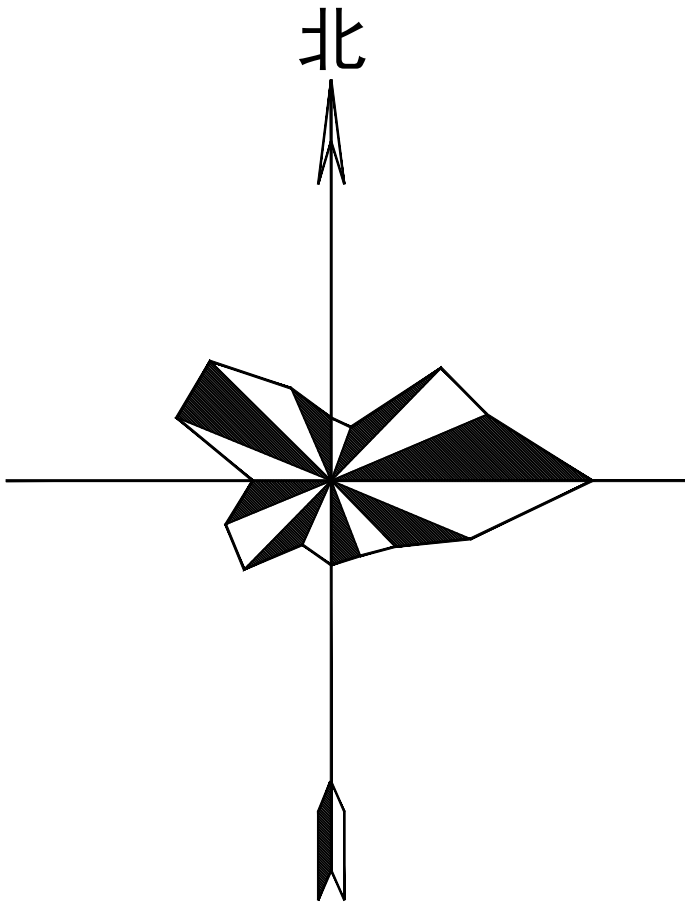


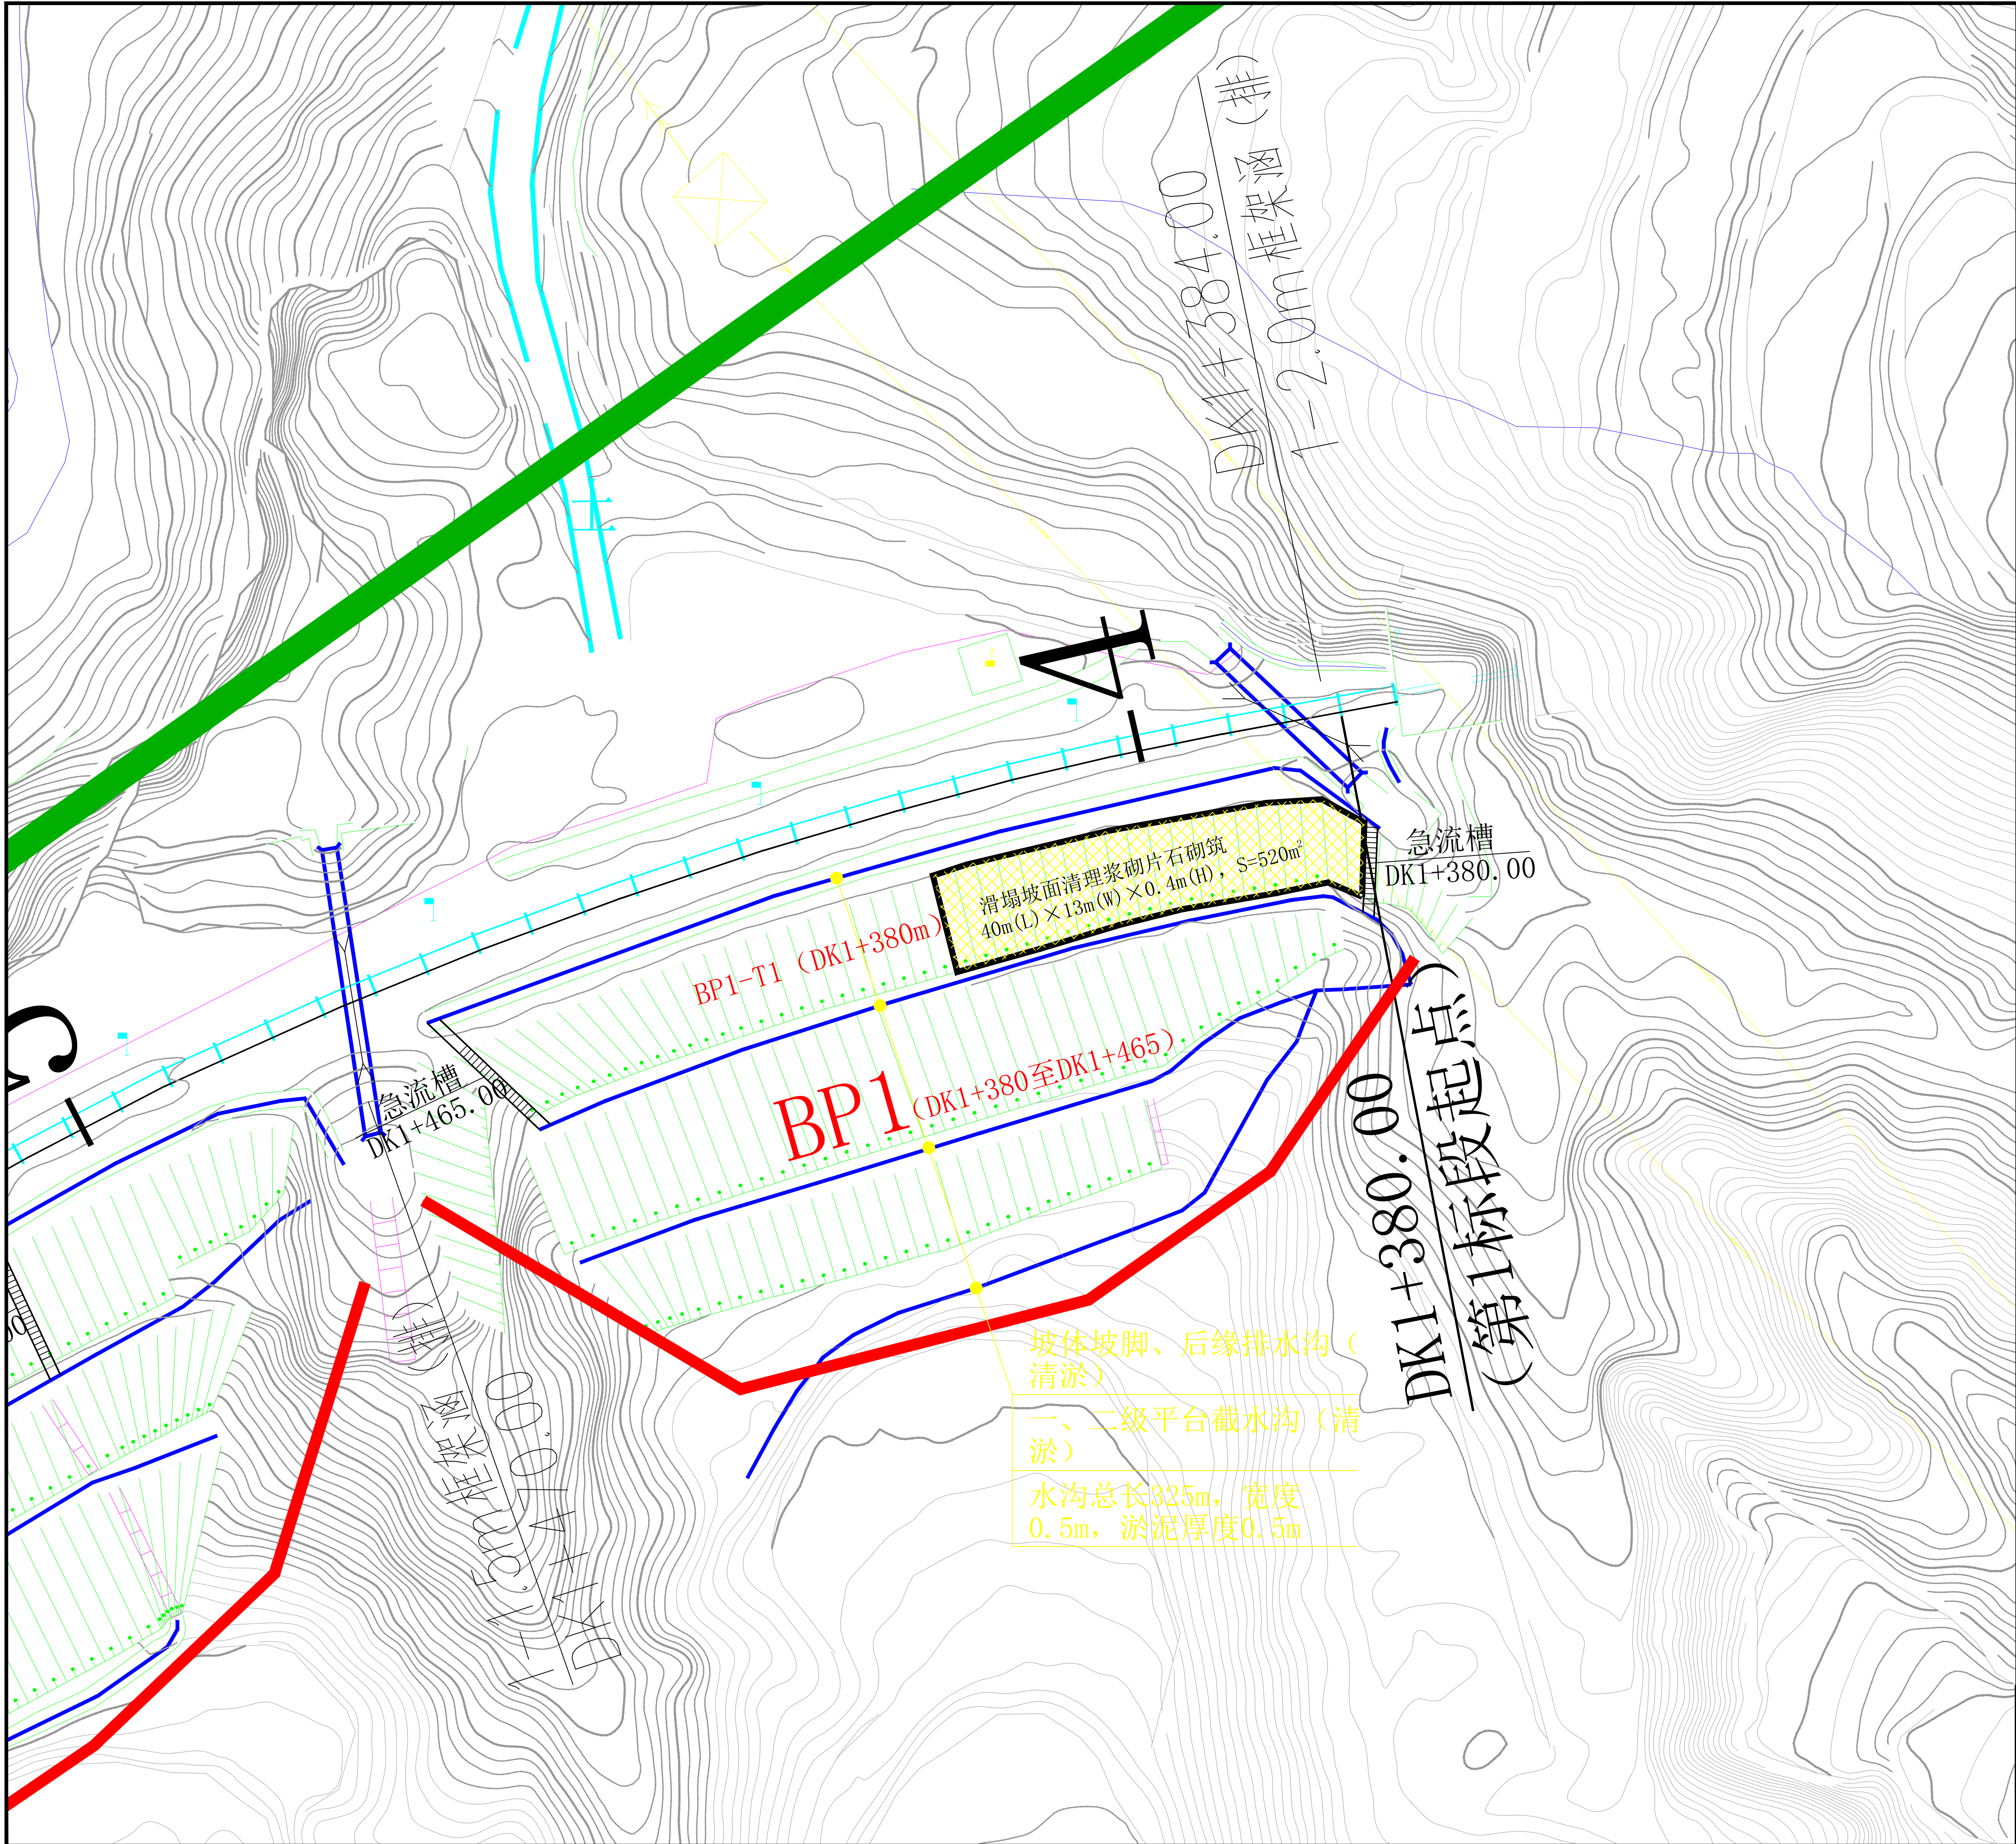

图例:

- BP1 边坡范围及编号
- BP1-T1 塌陷治理区域及编号
- 原状边坡坡线
- 新建截(排)水沟
- 急流槽
- 已有建、构筑物
- 已有截(排)水沟
- 涵洞
- 线路及公里标
- 调查区范围

山西文龙中美环境科技股份有限公司

标记	数量	修改者	批准者	日期	技术专用章	太原煤气化能源发展有限公司铁路沿线边坡维修处治工程
设计	1	和	和	2025.10.10	资质等级 铁路专用线	S1424-1951(1)-01
检查	1	和	和	2025.10.10	总工程师 和	共 2 页 第 1 页
审定	1	和	和	2025.10.10	总工程师 和	规格 A1 比例 1:500
2025年10月编制						山西文龙中美环境科技股份有限公司 (原名: 山西文龙环境工程设计有限公司)