

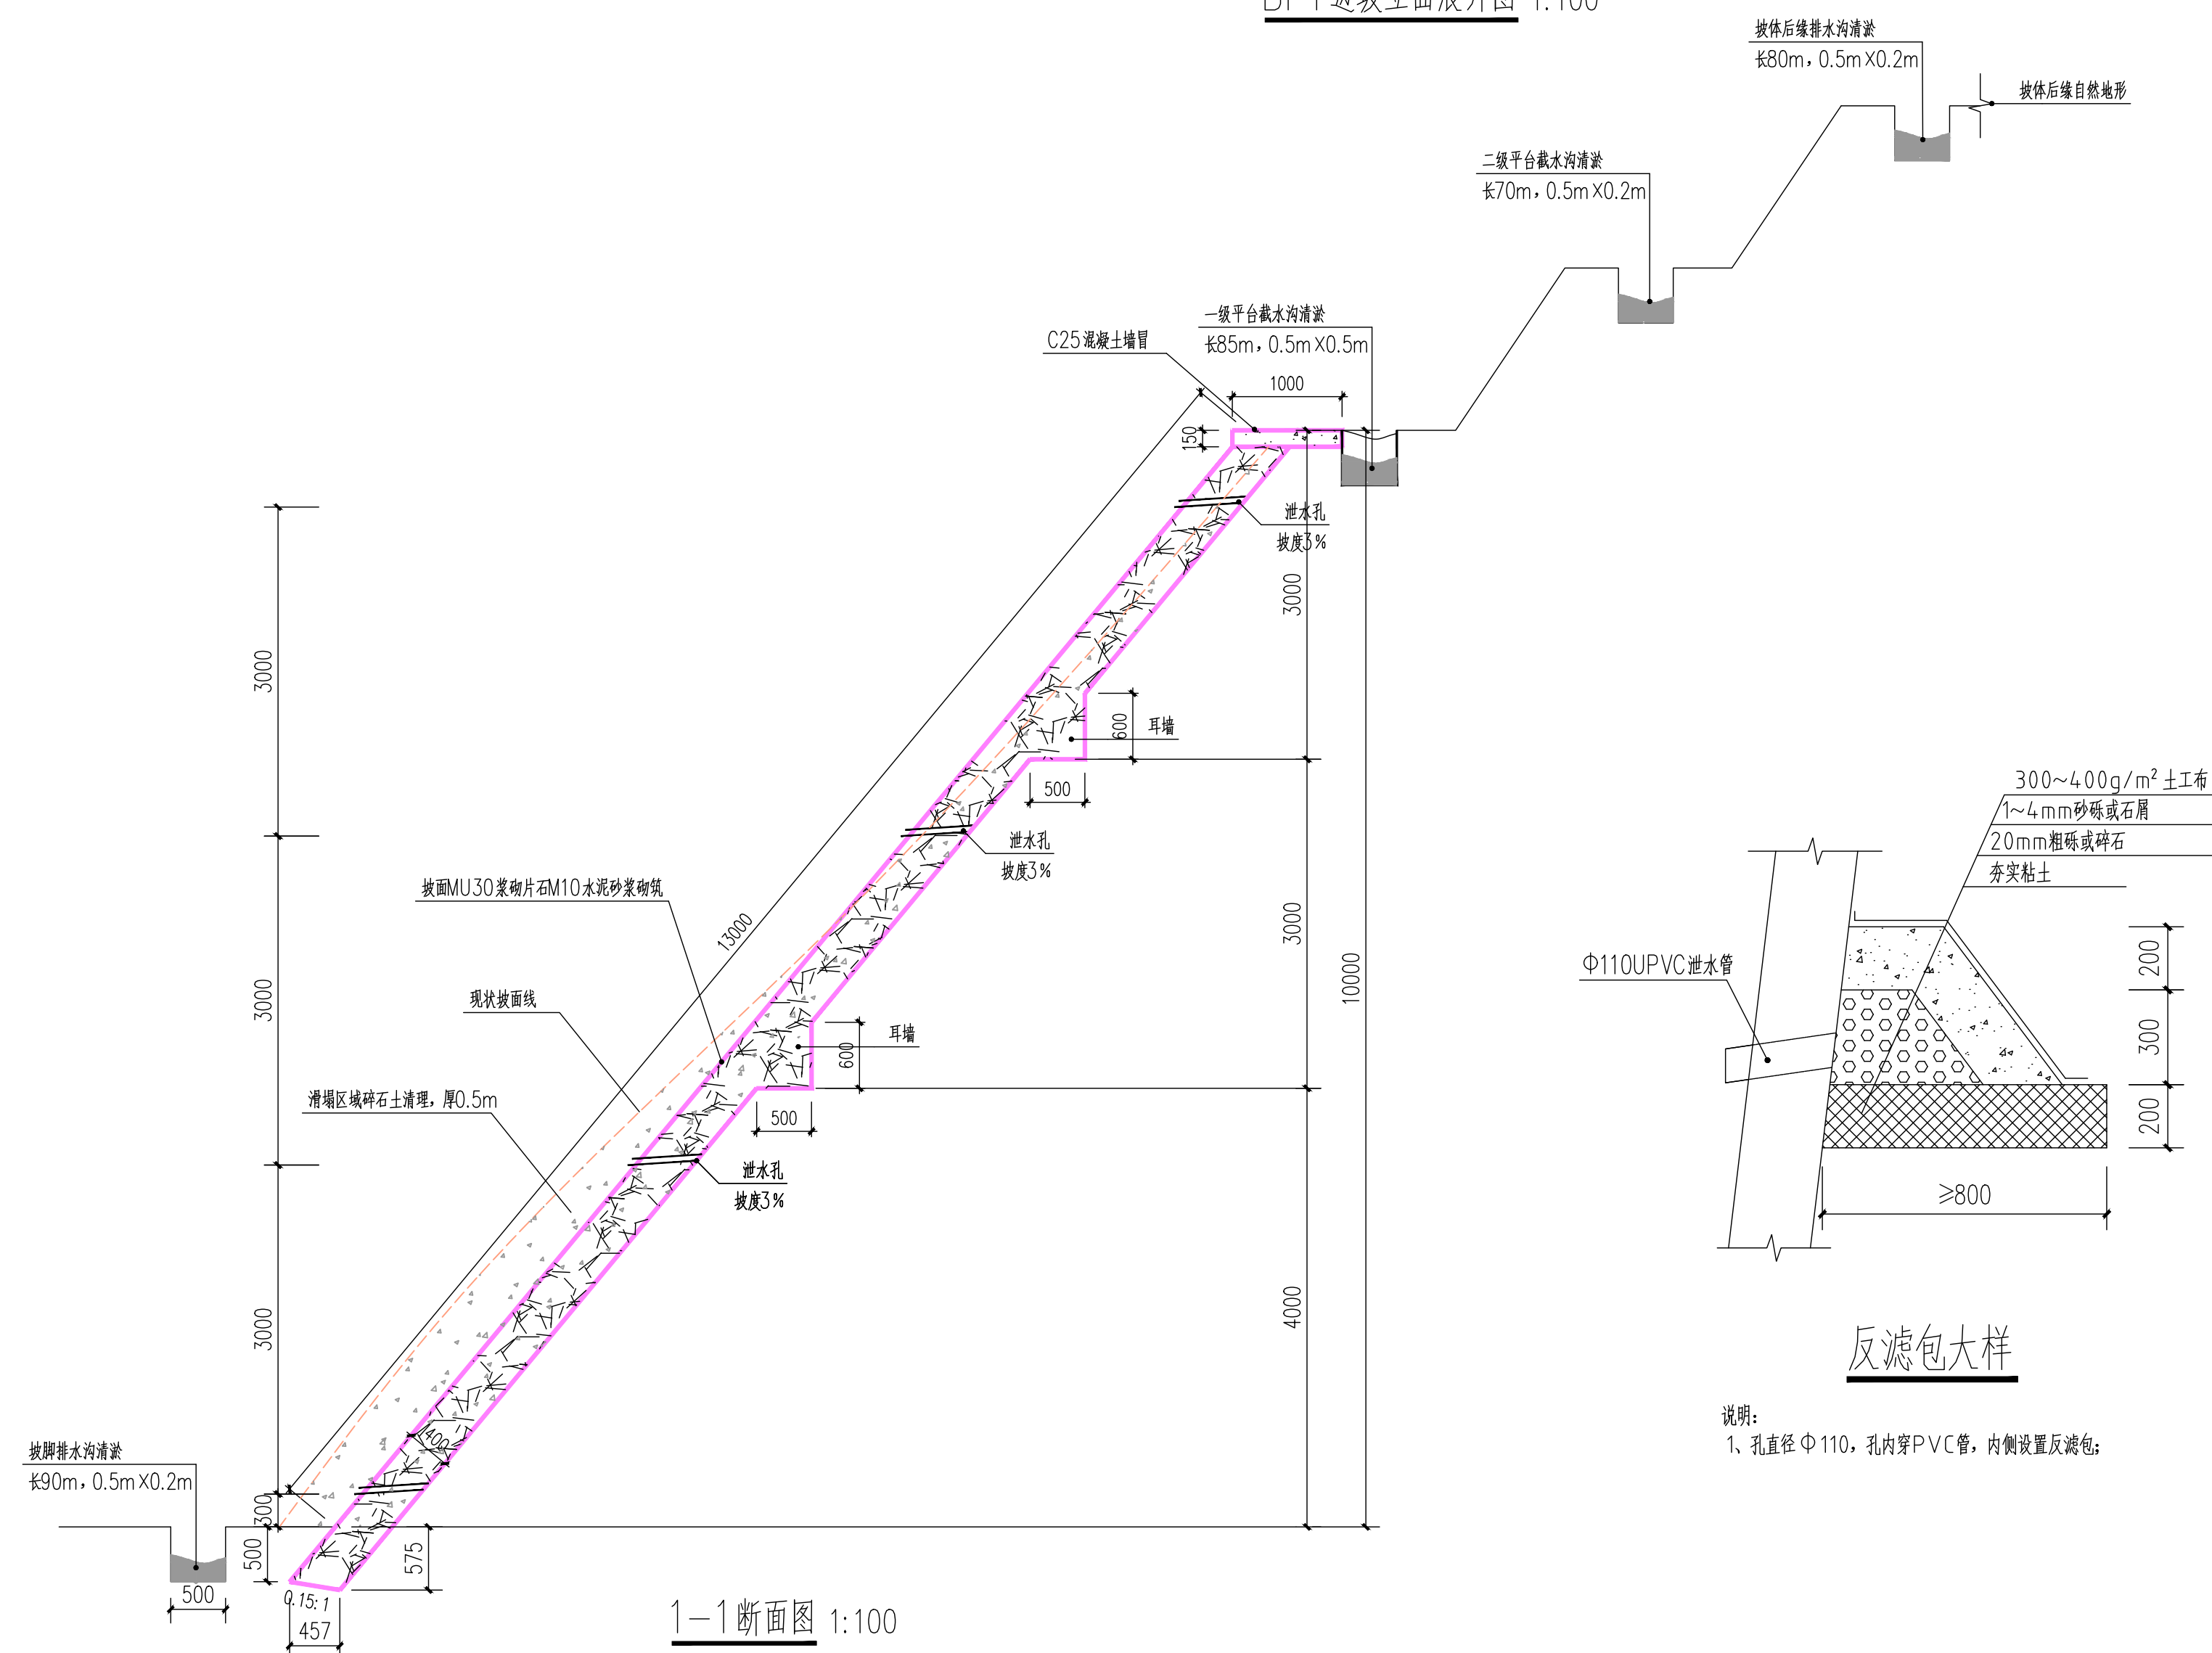


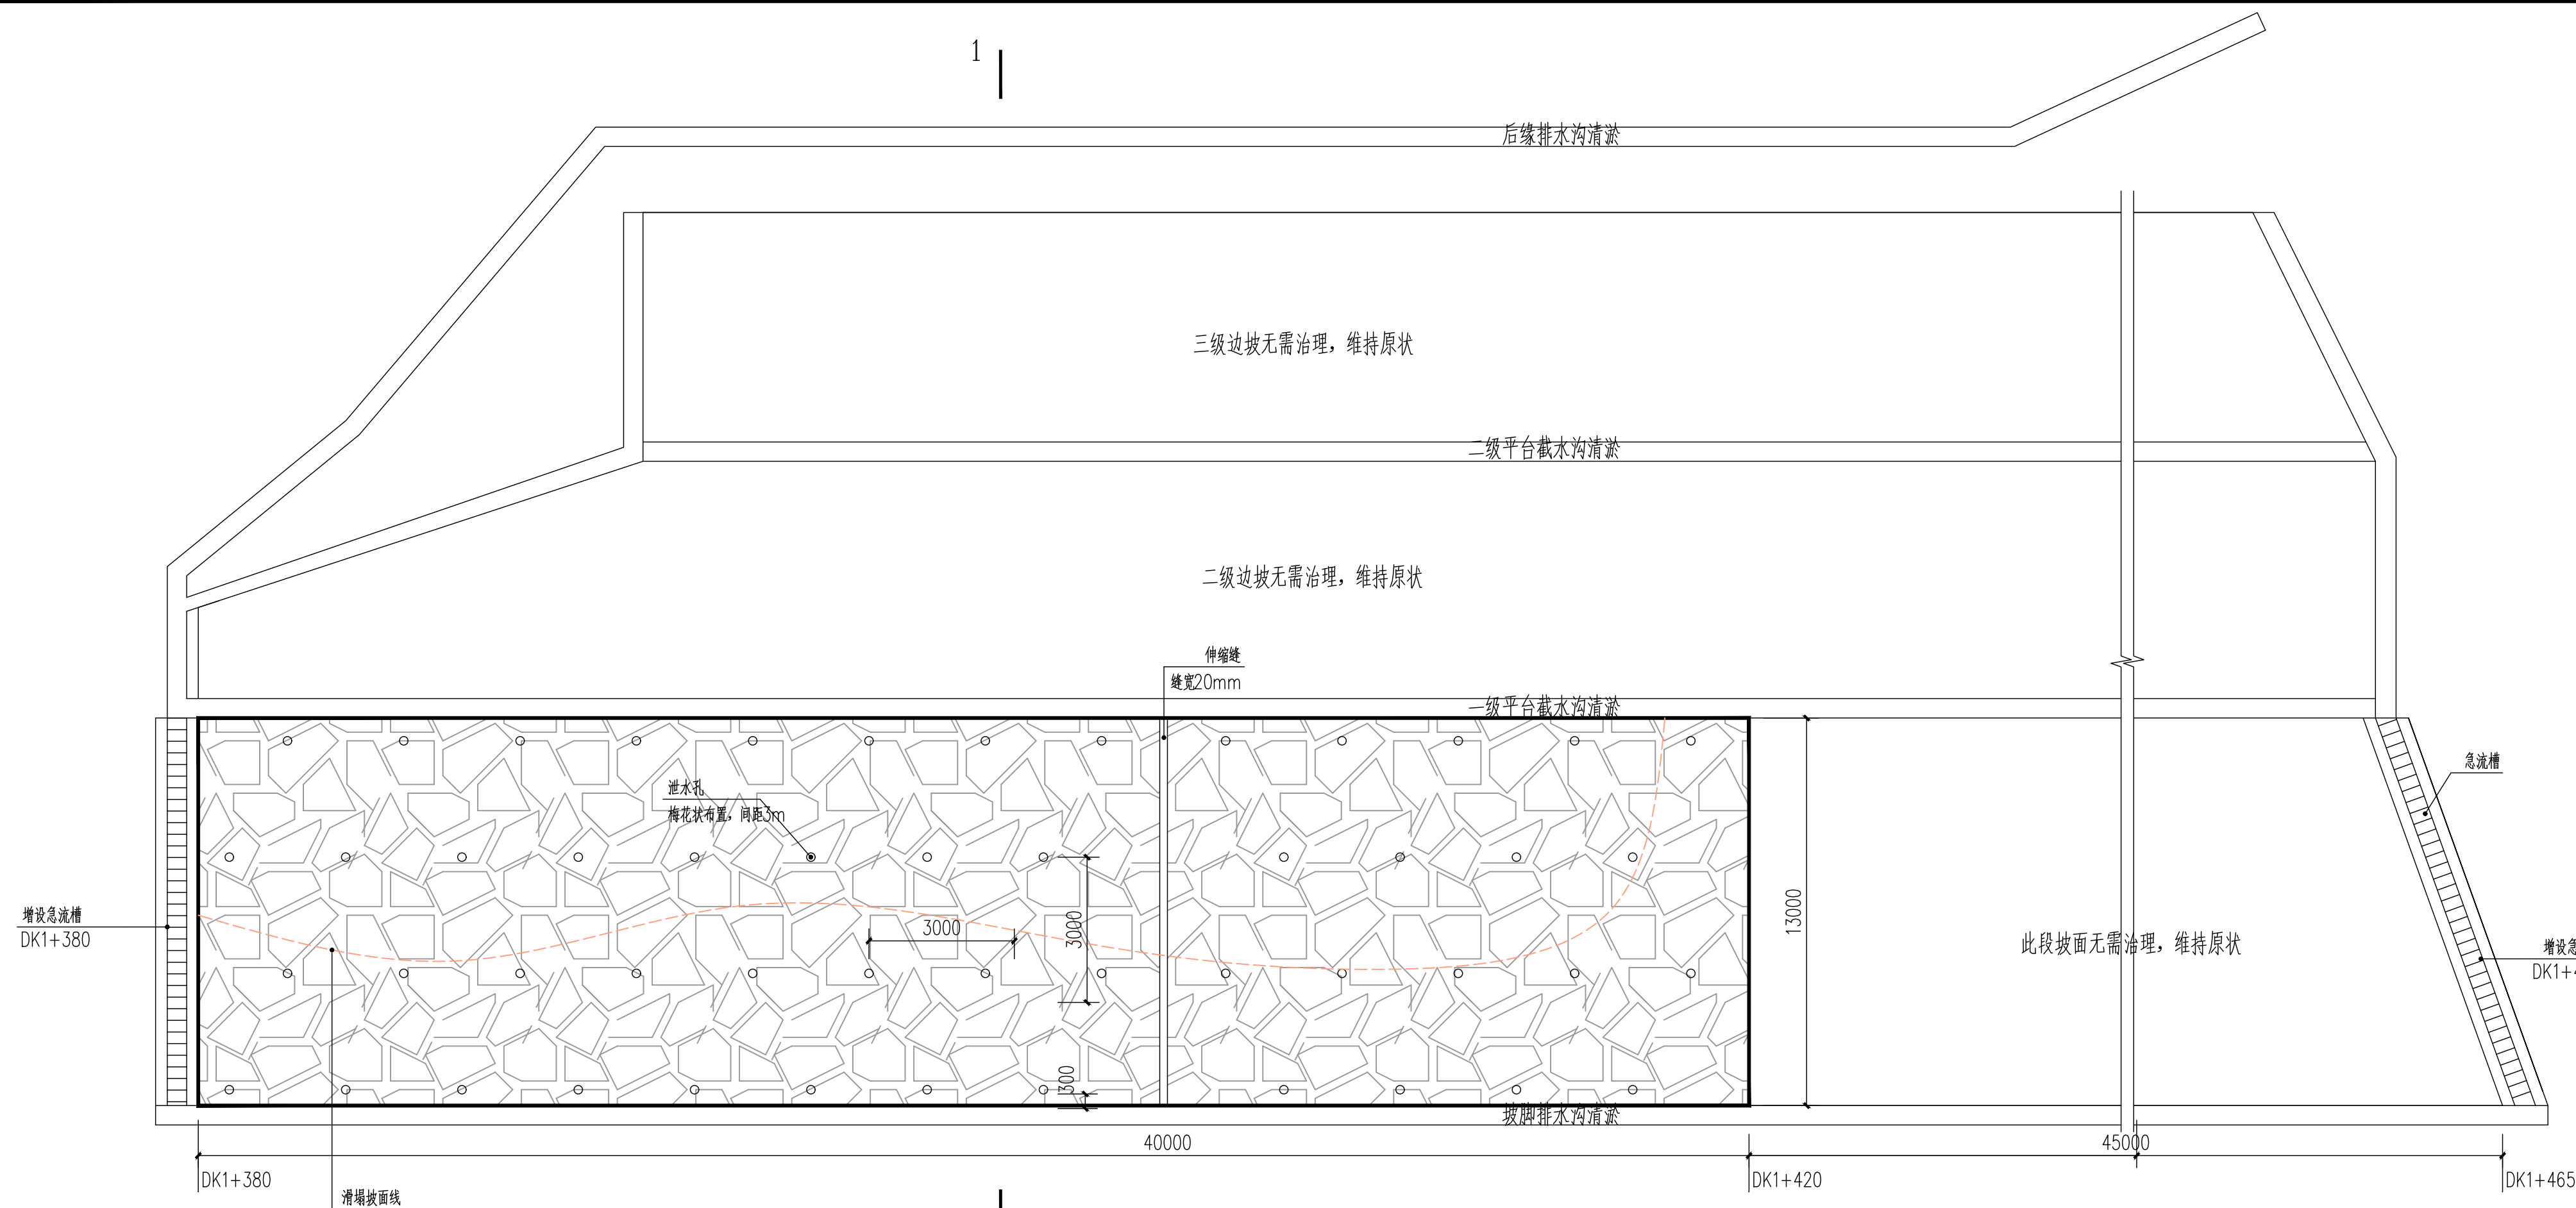

说明





1. 实体护面墙的材料采用M10水泥砂浆砌筑MU30片石，地基承载力不小于150Kpa。
2. 实体护面墙墙身上下预埋PVC管，位置见护面墙坡面布置图，呈梅花形交错布置。孔口大小直径为110mm，泄水孔后用碎石和沙砾作为反滤层，底层泄水孔距边沟顶面0.3m，底层泄水孔下部设置粘土隔水层。
3. 护面墙西侧间距15米处，均设置一道伸缩缝，通到基础底，缝宽20mm，缝内沿墙的内、外、顶三边用沥青麻丝或沥青木板填塞，塞入深度不宜小于200mm。
4. 护面墙施工必须紧贴坡面，墙身起挖部分应用C25混凝土砌筑，不得回填土；当实体护面墙高度为 $3\text{m} \leq H \leq 6\text{m}$ 时，墙背设一个耳墙； $H > 6\text{m}$ 时，墙背设两个耳墙。
5. 护面墙顶部应原土夯实，以免边坡水流冲刷，渗入墙后引起破坏。
6. 护面墙施工时各道工序应紧密衔接，连续施工，严禁爆破，以免坡面长期暴露或爆破震松造成边坡坍塌，护面墙基础应设置在稳定的地基上。
7. 修筑护面墙前，对所防护的边坡，应清除滑塌的片石及碎石土等，凹陷处可挖成错台；平台用M10水泥砂浆砌筑MU30片石，铺砌厚度250mm。
8. 本图尺寸标注均以毫米计。
9. 图中未详按相关规范执行。

山西文龙中美环保科技有限公司					
技术专用章					
太原煤气化龙泉能源发展有限公司铁路沿线边坡维修处治工程					
标记	数量	修改者	批准者	日期	
设计	1份	张彦春	张彦春	2025.10.18	
检查	1份	贾英行	贾英行	2025.10.18	
审定	1份	贾英行	贾英行	2025.10.18	
资质证书 证书编号 S1424-1951(1)-03					
铁路专用线 共 4 页 规格 比例 第 3 页 A4 1:100					
边坡立面图、1-1断面图					山西文龙中美环保科技有限公司 (原名：山西文龙煤矿工程设计有限公司)
2025年10月编制					

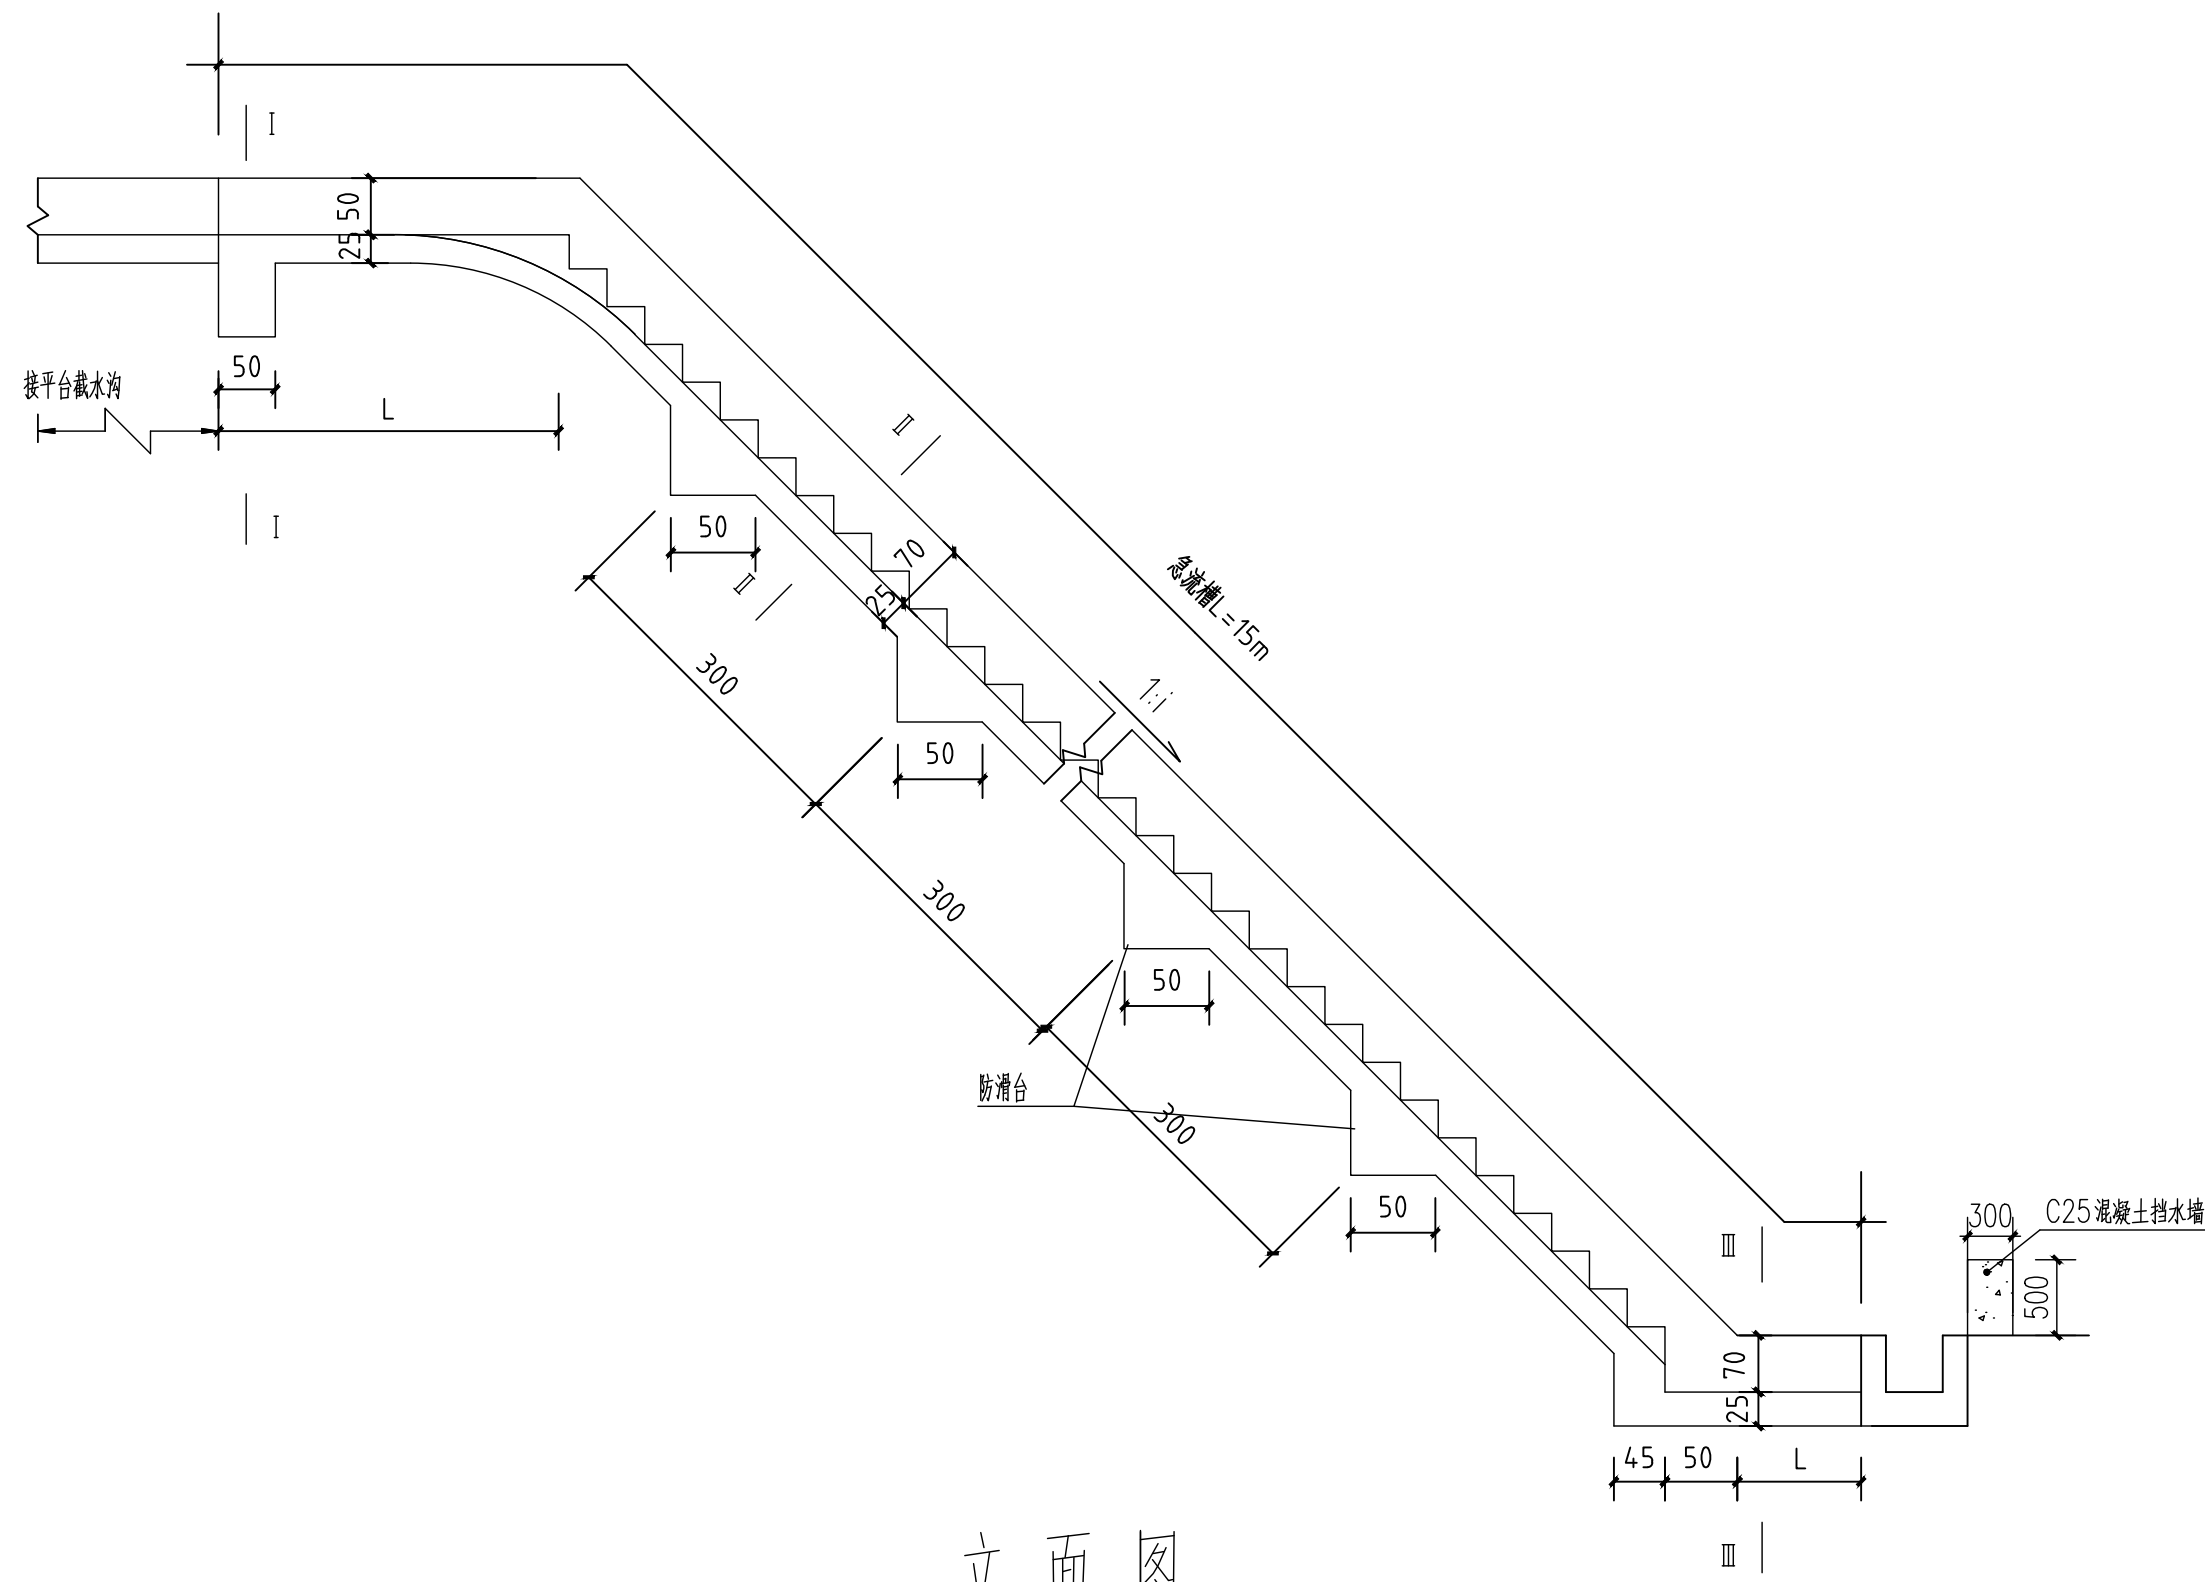

立面图

单位: cm

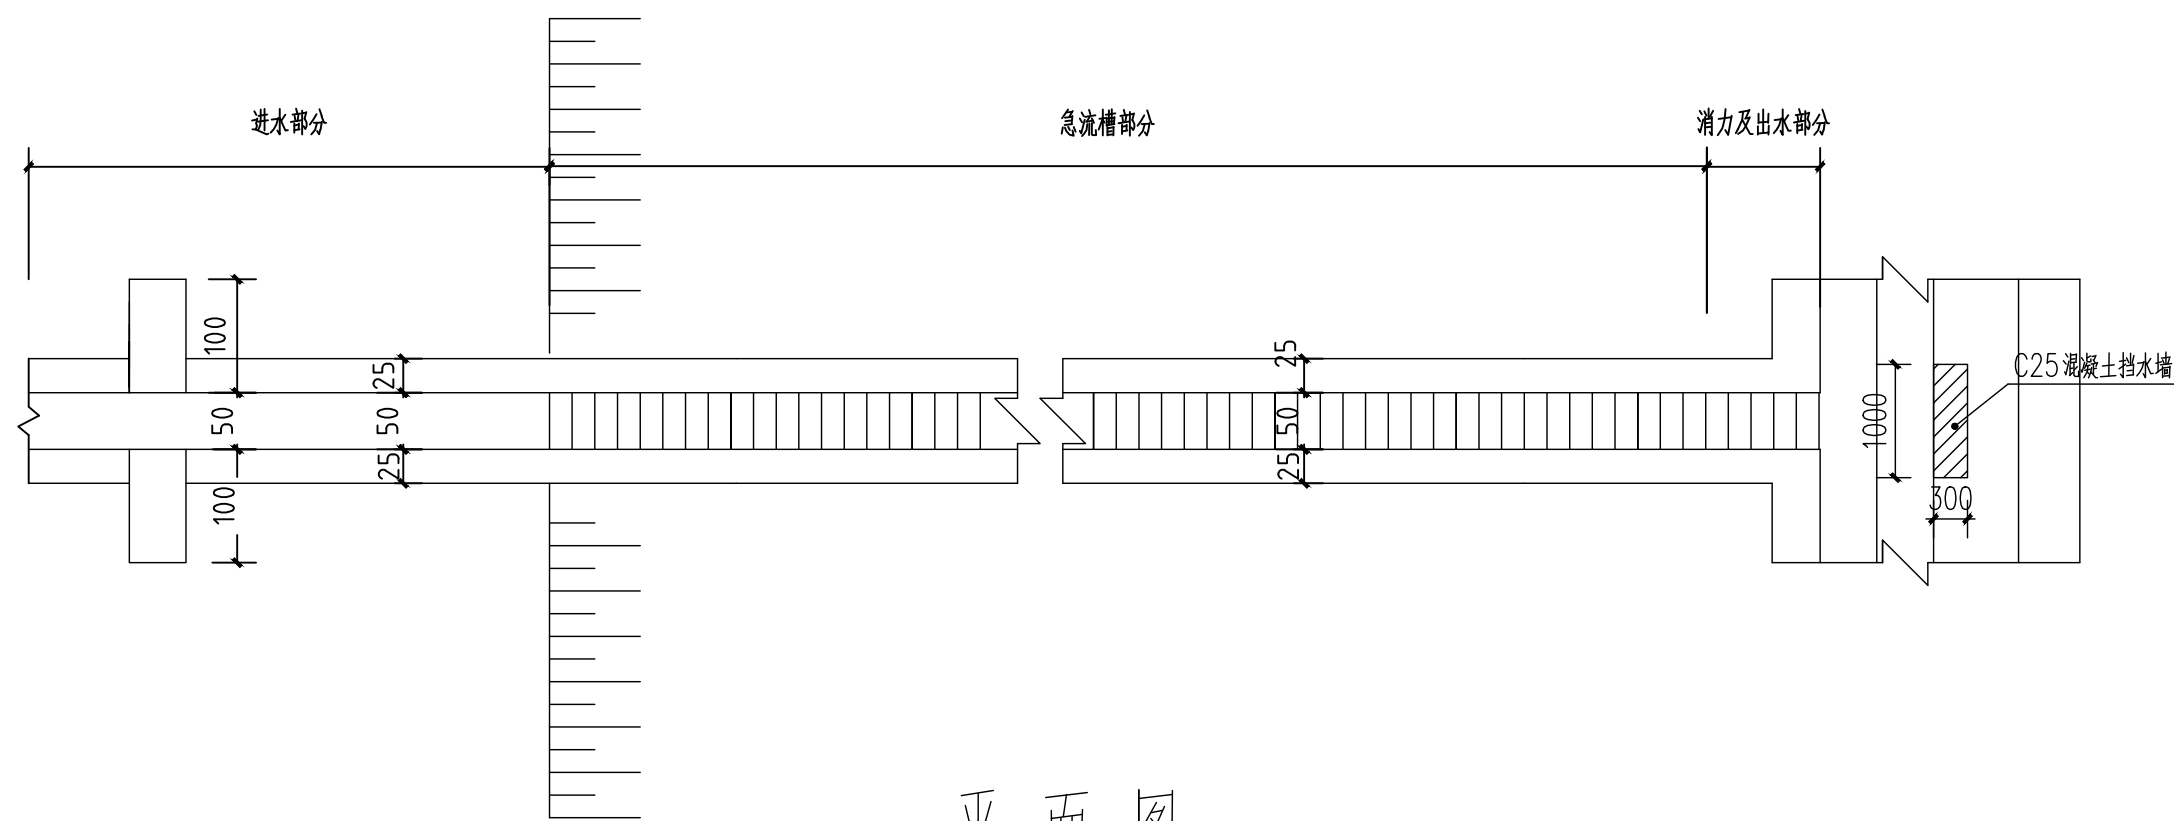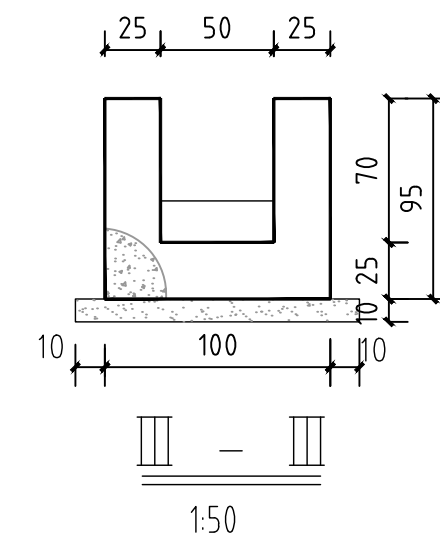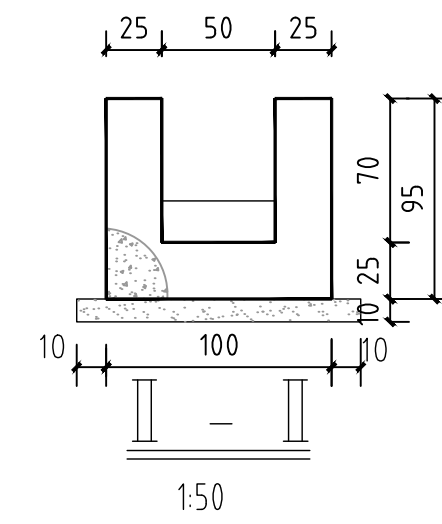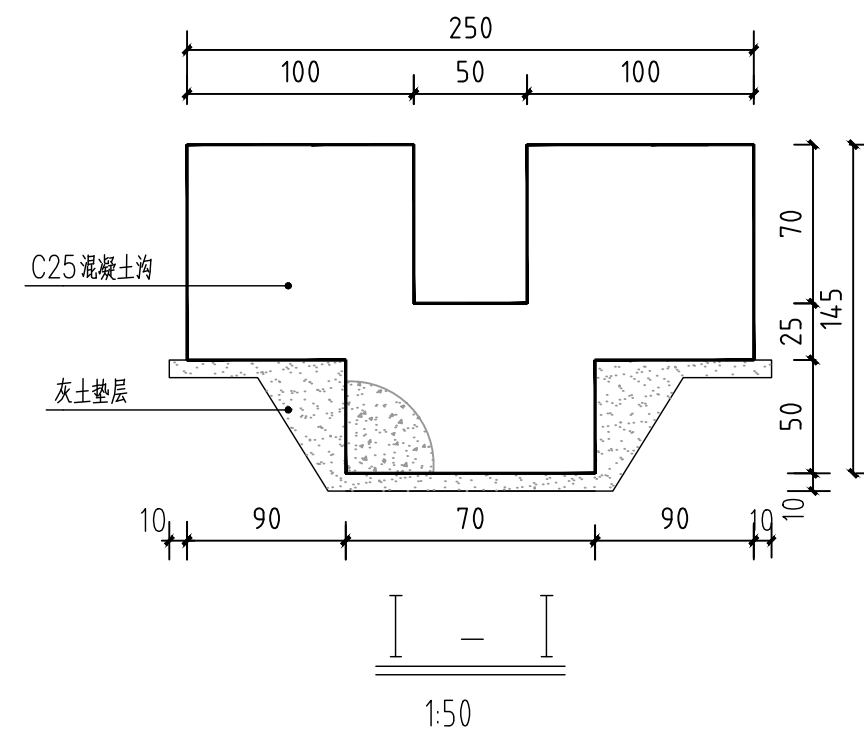

平面图

单位: cm

注:

- 1、一级边坡DK1+380m、DK1+465m处增设急流槽，将一级平台截水沟与坡脚排水沟连接，排至附近排水涵洞。急流槽长15m。
- 2、本图尺寸以厘米计。
- 3、本图适用于截水沟与边沟连接处，或直接排出路基外与自然沟渠相接。
- 4、急流槽采用C25混凝土浇筑。
- 5、基础处理采用10cm厚3:7灰土。

山西文龙中美环能科技股份有限公司									
技术专用章									
标记	数量	修改者	批准者	日期	设计	审核	校核	制图	山西文龙中美环能科技股份有限公司铁路沿线边坡维修处治工程
设计	1	张明	张明	2025.10.10	张明	张明	张明	张明	S1424-1951(1)-04
检查	1	张明	张明	2025.10.10	张明	张明	张明	张明	共 4 页
审定	1	张明	张明	2025.10.10	张明	张明	张明	张明	规格
2025年10月编制					急流槽详图				比例
					山西文龙中美环能科技股份有限公司				1:100