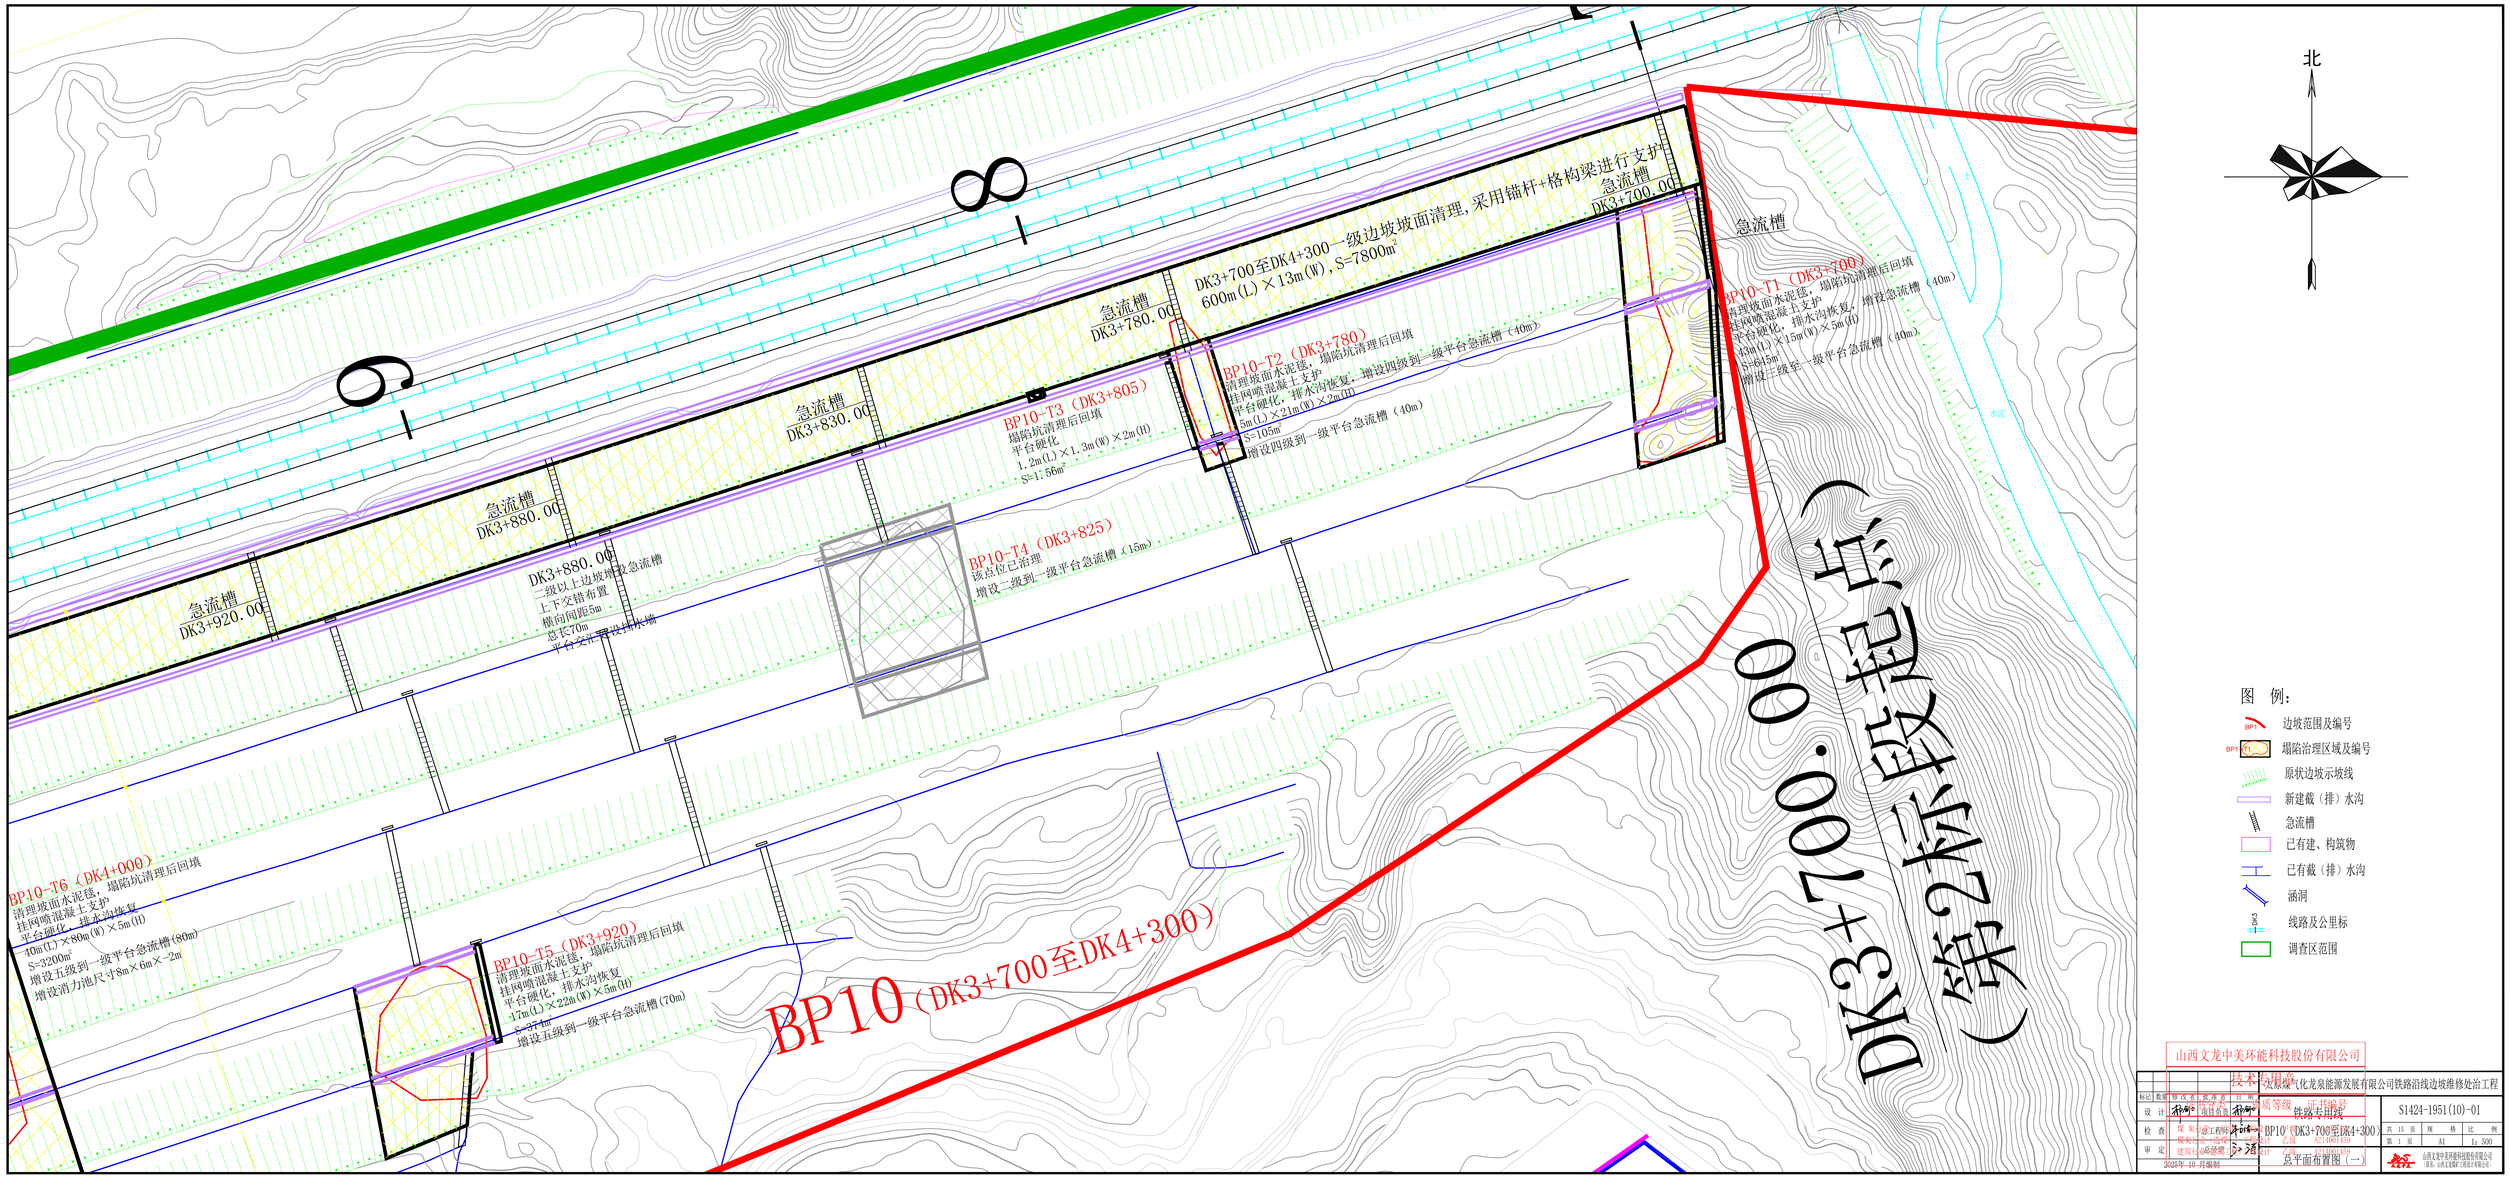

北
图 例：
边坡范围及编号
塌陷治理区域及编号
原状边坡示坡线
新建截（排）水沟
急流槽
已有建、构筑物
已有截（排）水沟
涵洞
线路及公里标
调查区范围
BP10（DK3+700至DK4+300）
DK3+700.00（线路左侧）
急流槽
DK3+700.00
急流槽
DK3+780.00
急流槽
DK3+830.00
急流槽
DK3+880.00
急流槽
DK3+920.00
DK3+700至DK4+300一级边坡坡面清理，采用锚杆+格构梁进行支护
600m(L)×13m(W)，S=7800m²
BP10-T1（DK3+700）
清理坡面水泥毯，塌陷坑清理后回填
挂网喷混凝土支护
平台硬化，排水沟恢复，增设急流槽（40m）
3m(L)×15m(W)×5m(H)
S=615m²
增设二级至一级平台急流槽（40m）
BP10-T2（DK3+780）
清理坡面水泥毯，塌陷坑清理后回填
挂网喷混凝土支护
平台硬化，排水沟恢复，增设四级到一级平台急流槽（40m）
5m(L)×21m(W)×2m(H)
S=105m²
增设四级到一级平台急流槽（40m）
BP10-T3（DK3+805）
塌陷坑清理后回填
平台硬化
1.2m(L)×1.3m(W)×2m(H)
S=1.56m²
BP10-T4（DK3+825）
该点位已治理
增设二级到一级平台急流槽（15m）
DK3+880.00
一级以上边坡增设急流槽
上下交错布置
横向间距5m
总长70m
平台处二级设挡水墙
BP10-T5（DK3+920）
清理坡面水泥毯，塌陷坑清理后回填
挂网喷混凝土支护
平台硬化，排水沟恢复
17m(L)×22m(W)×5m(H)
S=374m²
增设五级到一级平台急流槽（70m）
BP10-T6（DK4+000）
清理坡面水泥毯，塌陷坑清理后回填
挂网喷混凝土支护
平台硬化，排水沟恢复
40m(L)×80m(W)×5m(H)
S=3200m²
增设五级到一级平台急流槽（80m）
增设消力池尺寸8m×6m×-2m
水渠
山西文龙中美环能科技股份有限公司
技术与服务
资质等级
项目名称 大同煤矿集团云冈煤化龙泉能源发展有限公司铁路沿线边坡维修处治工程
铁路专用线
BP10（DK3+700至DK4+300）
总平面布置图（一）
S1424-1951(10)-01
2025年10月编制