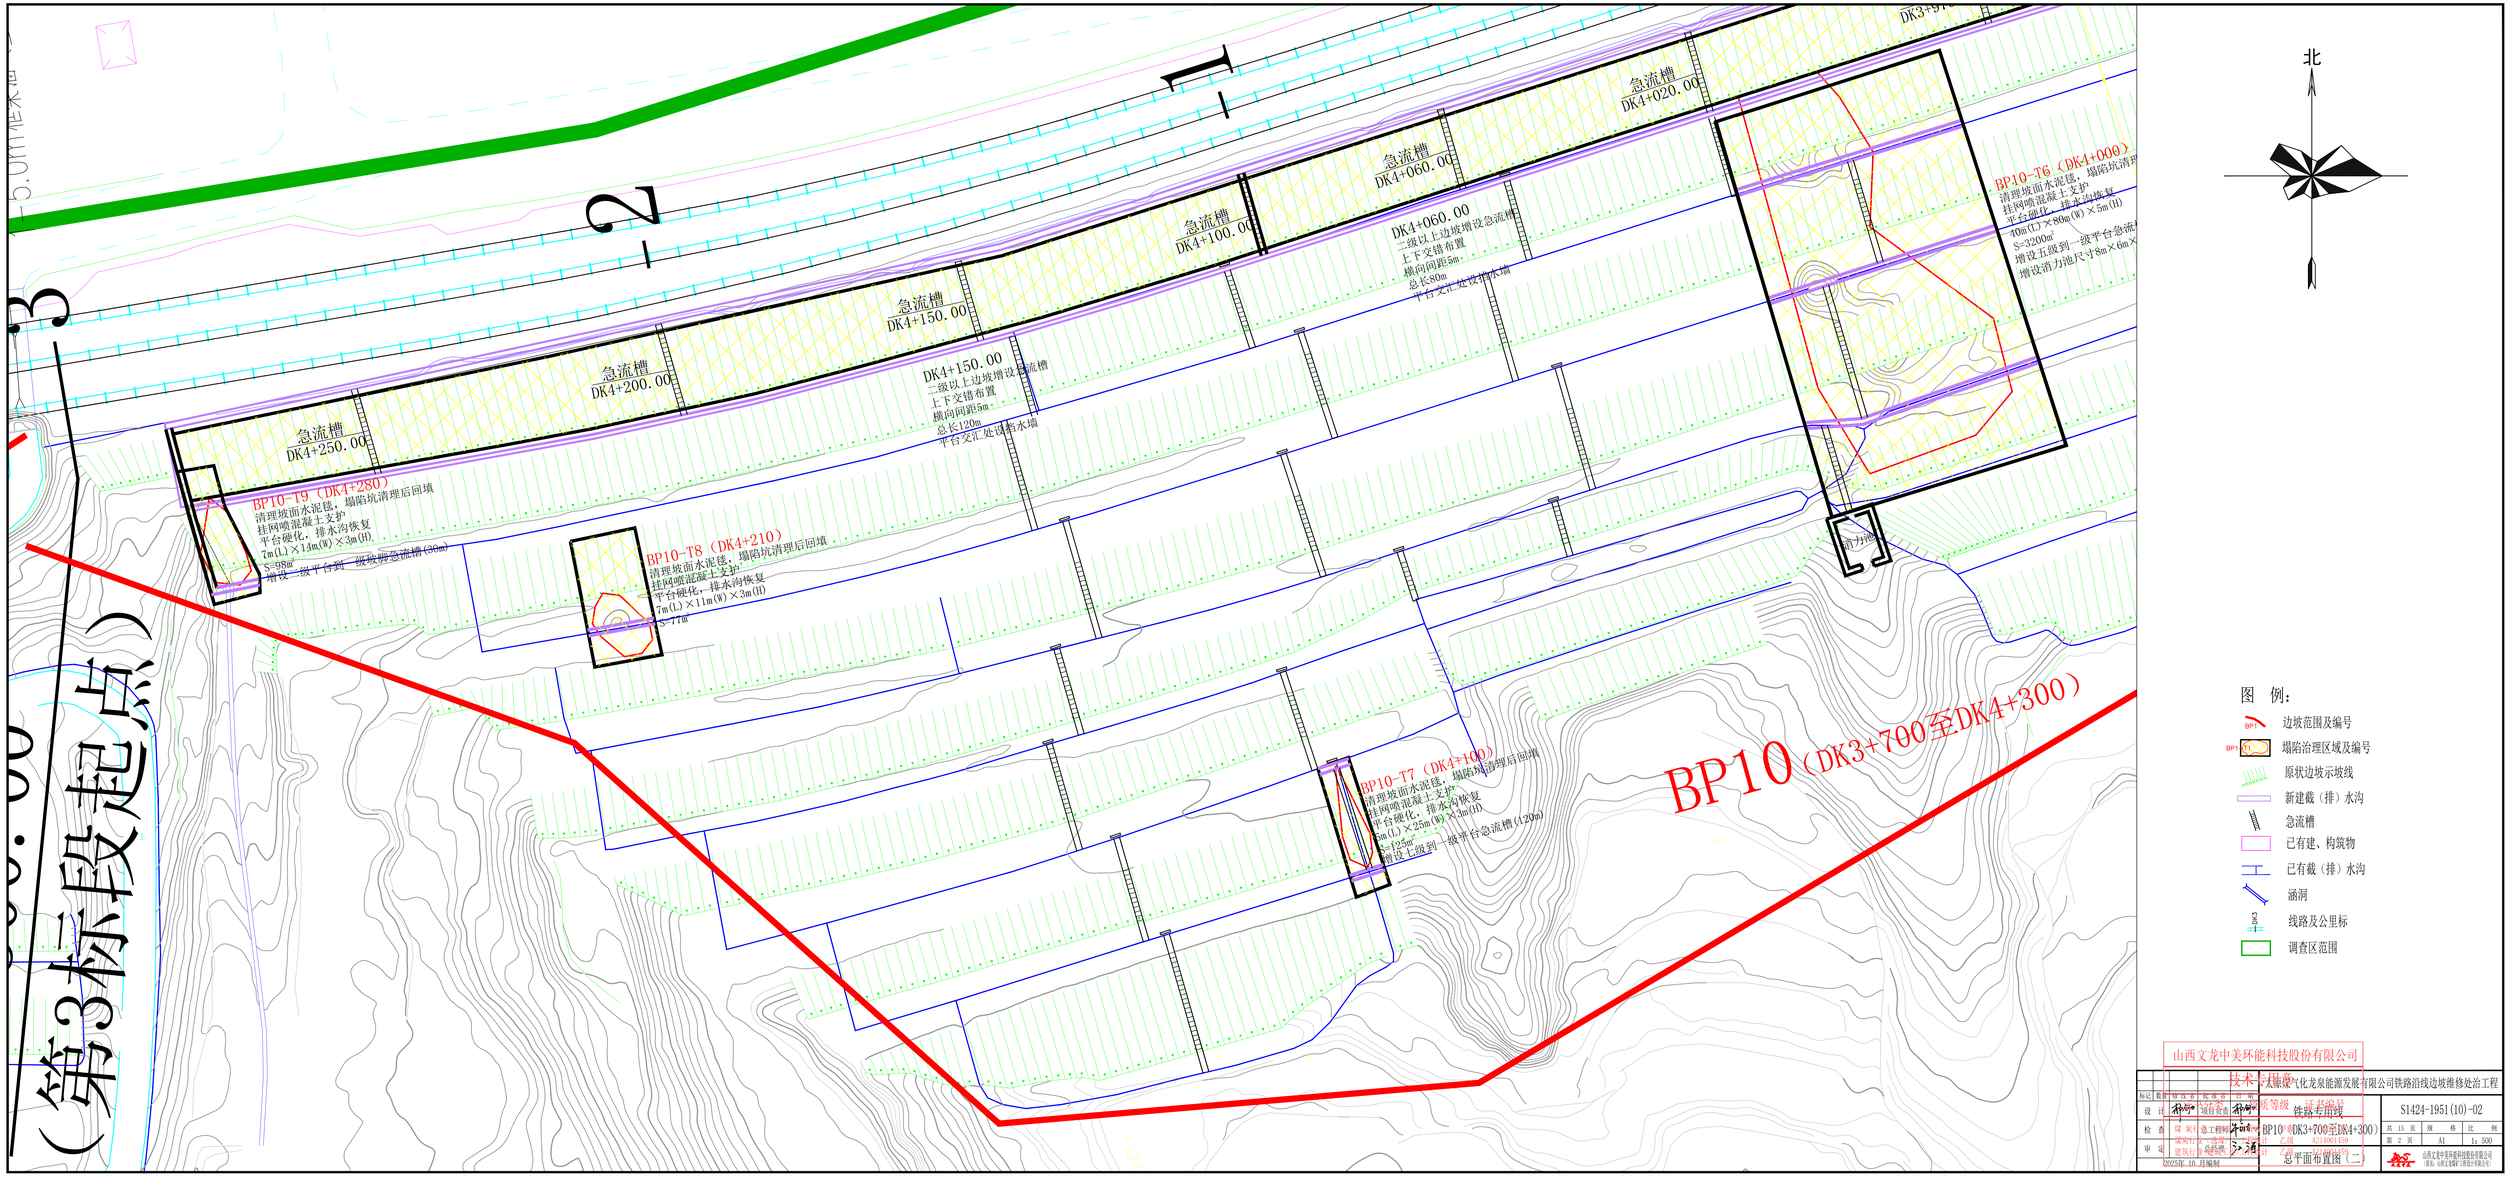
（第3标段起点）
BP10（DK3+700至DK4+300）
急流槽 DK4+250.00
急流槽 DK4+200.00
急流槽 DK4+150.00
急流槽 DK4+100.00
急流槽 DK4+060.00
急流槽 DK4+020.00
DK4+150.00 二级以上边坡增设急流槽 上下交错布置 横向间距5m，总长120m 平台交汇处设排水墙
DK4+060.00 二级以上边坡增设急流槽 上下交错布置 横向间距5m，总长80m 平台交汇处设排水墙
BP10-T9（DK4+280） 清理坡面水泥毯，塌陷坑清理后回填 挂网喷混凝土支护 平台硬化，排水沟恢复 7m(L)×14m(W)×3m(H) S=98m² 增设一级平台到一级坡脚急流槽(30m)
BP10-T8（DK4+210） 清理坡面水泥毯，塌陷坑清理后回填 挂网喷混凝土支护 平台硬化，排水沟恢复 7m(L)×11m(W)×3m(H) S=77m²
BP10-T7（DK4+100） 清理坡面水泥毯，塌陷坑清理后回填 挂网喷混凝土支护 平台硬化，排水沟恢复 5m(L)×25m(W)×3m(H) S=125m² 增设七级到一级平台急流槽(120m)
BP10-T6（DK4+000） 清理坡面水泥毯，塌陷坑清理 挂网喷混凝土支护 平台硬化，排水沟恢复 40m(L)×80m(W)×5m(H) S=3200m² 增设五级到一级平台急流槽 增设消力池尺寸8m×6m×
北
图 例：
边坡范围及编号
塌陷治理区域及编号
原状边坡示坡线
新建截（排）水沟
急流槽
已有建、构筑物
已有截（排）水沟
涵洞
线路及公里标
调查区范围
山西文龙中美环能科技股份有限公司
技术专用章
资质等级 甲级
证书编号 A111001439
山西文龙中美环能科技股份有限公司铁路沿线边坡维修处治工程
铁路专用线
BP10（DK3+700至DK4+300）
总平面布置图（二）
S1424-1951(10)-02
共 15 页 第 5 页
A1 1:500
2025年.10.月编制