
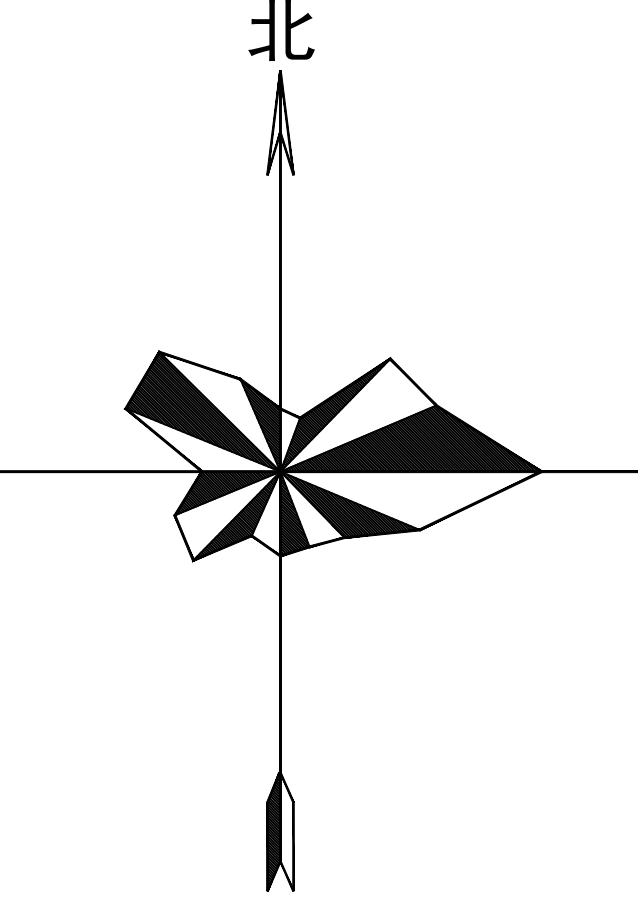


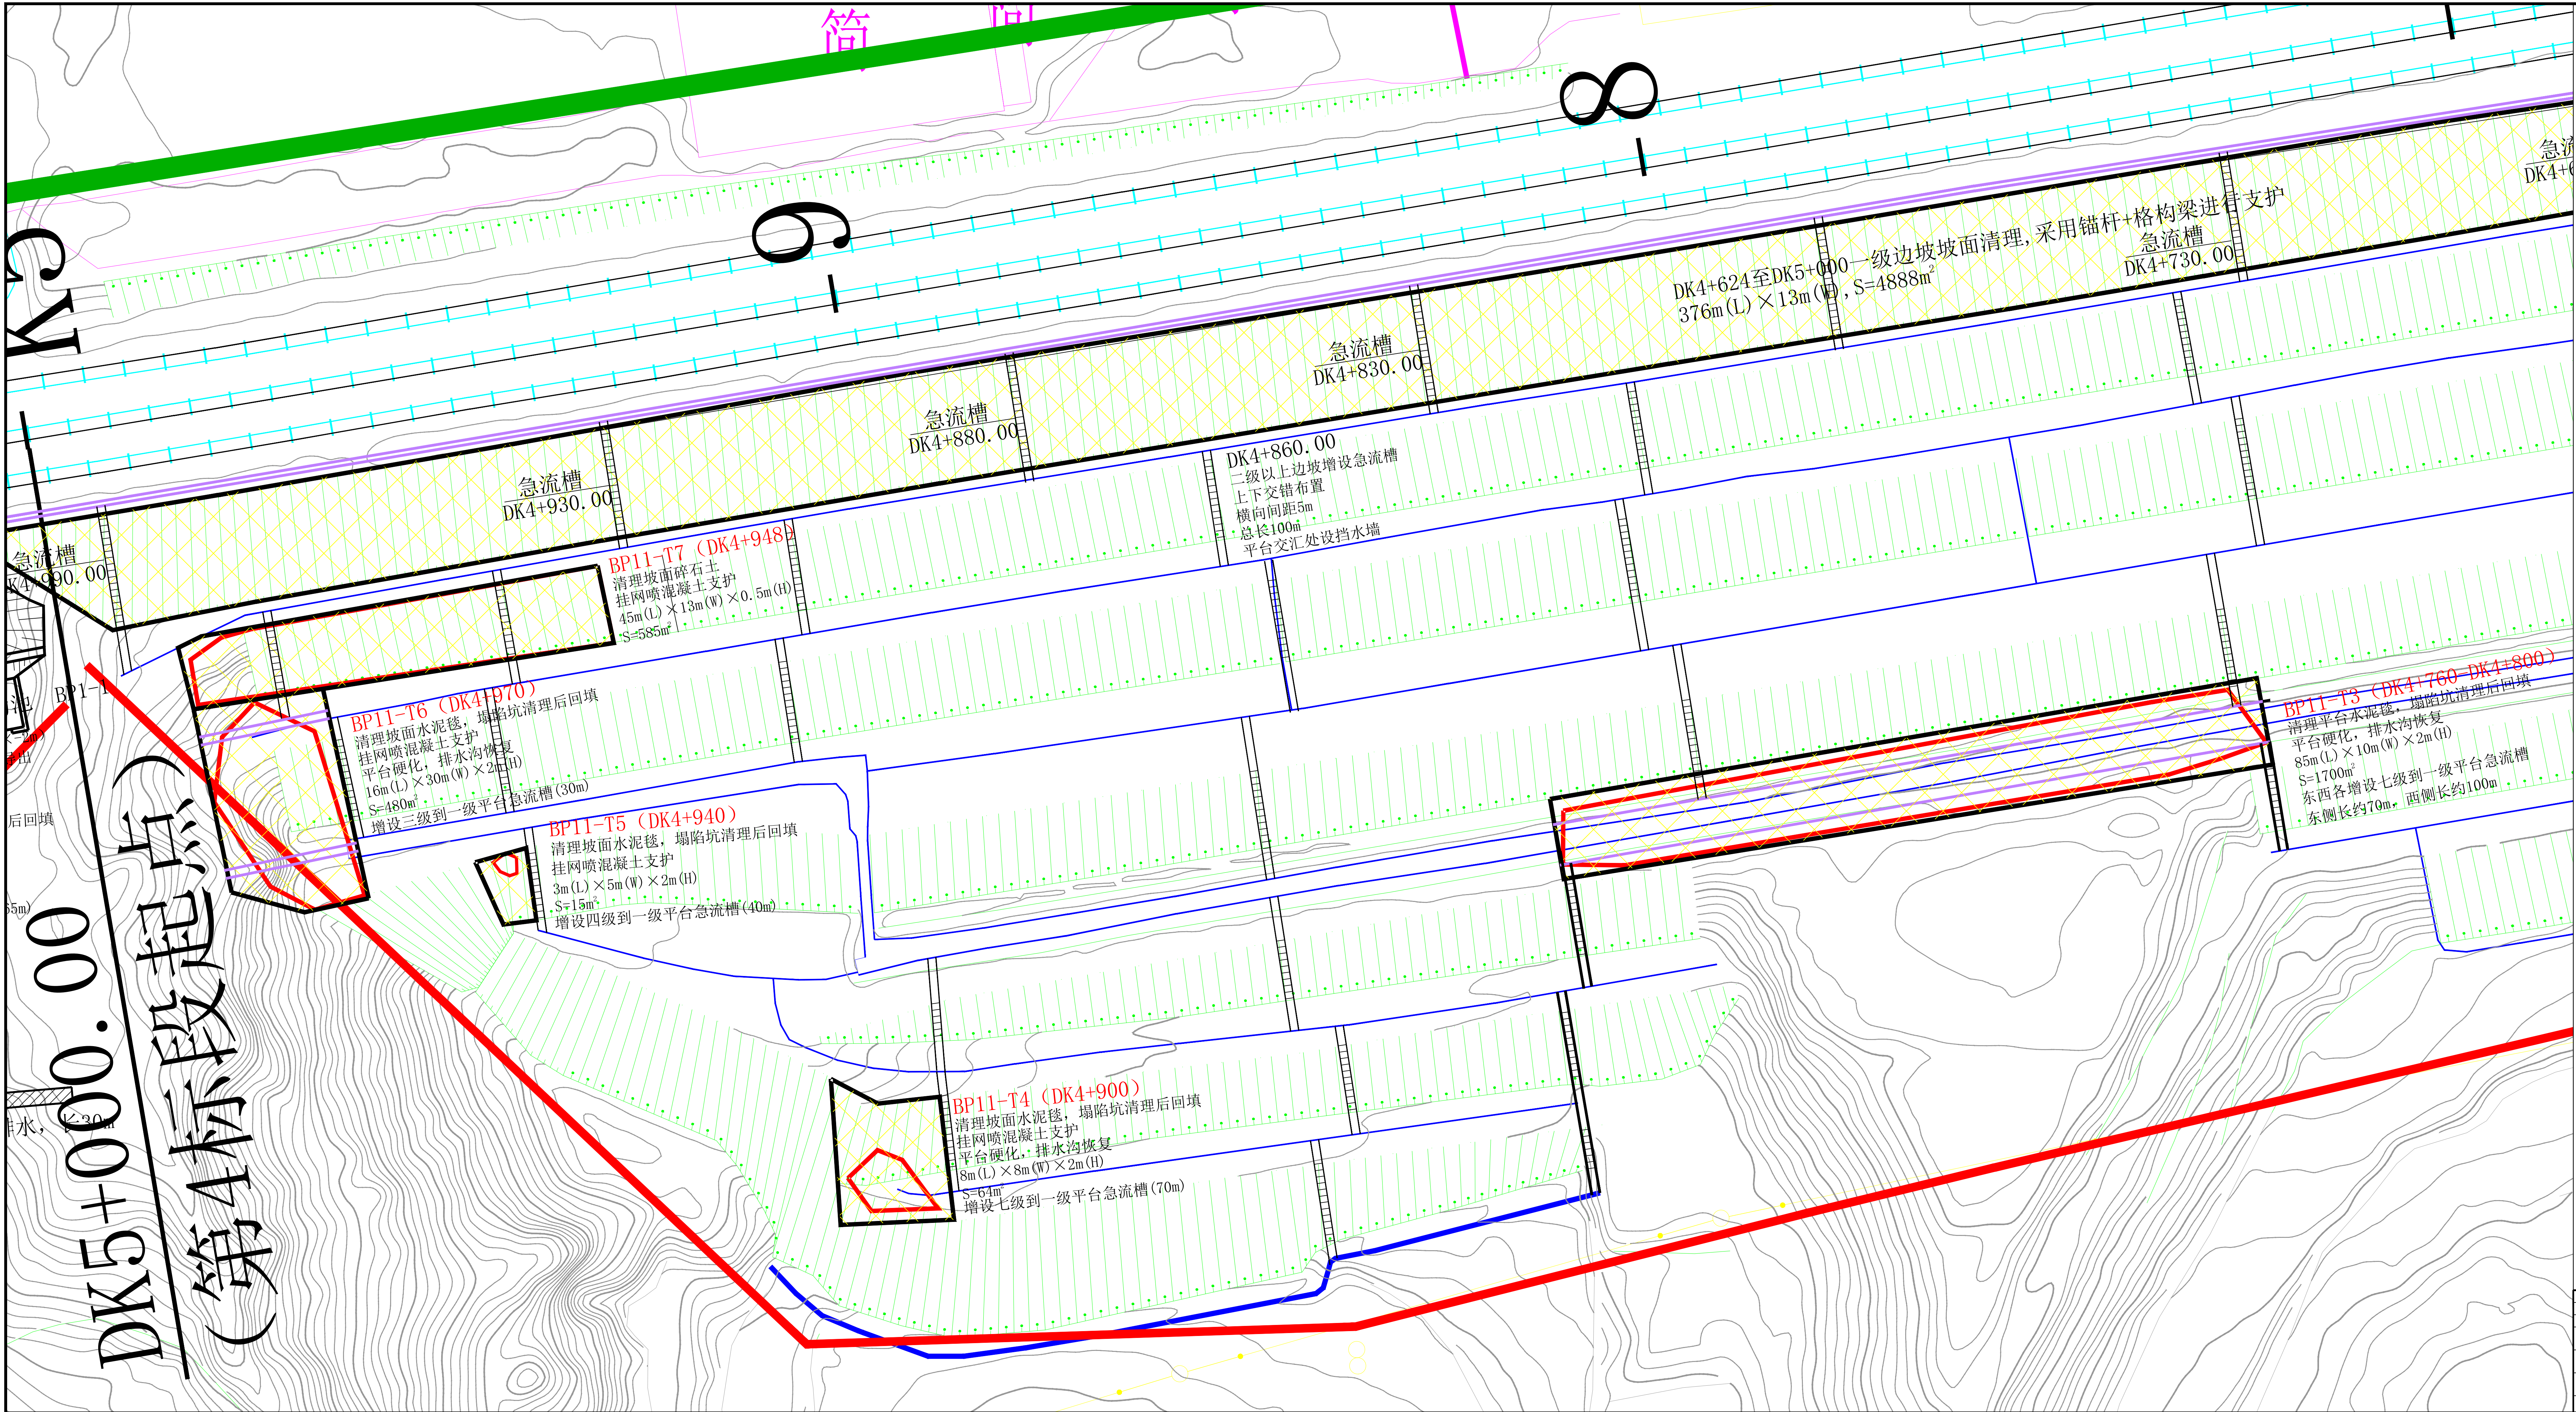

图例:

- 边坡范围及编号
- 崩塌治理区域及编号
- 原状边坡示坡线
- 新建截(排)水沟
- 急流槽
- 已有建、构筑物
- 已有截(排)水沟
- 涵洞
- 线路及公里标
- 调查区范围

山西文龙中美环能科技股份有限公司

标记	数量	修改者	审核者	日期	技术负责人	太原煤化工龙泉能源发展有限公司铁路沿线边坡维修处治工程
设计	审核	项目负责	审核	审核	资质证书编号	S1424-1951 (11)-02
检查	审核	总工程师	审核	审核	铁路专用线	
审定	审核	总工程师	审核	审核	BP11 (DK4+300至DK5+000)	共 13 页 规格 比例
		审核	审核	审核	总平面布置图 (一)	第 2 页 A1 1:500
		审核	审核	审核		山西文龙中美环能科技股份有限公司 (盖章: 山西文龙中美环能科技股份有限公司)