

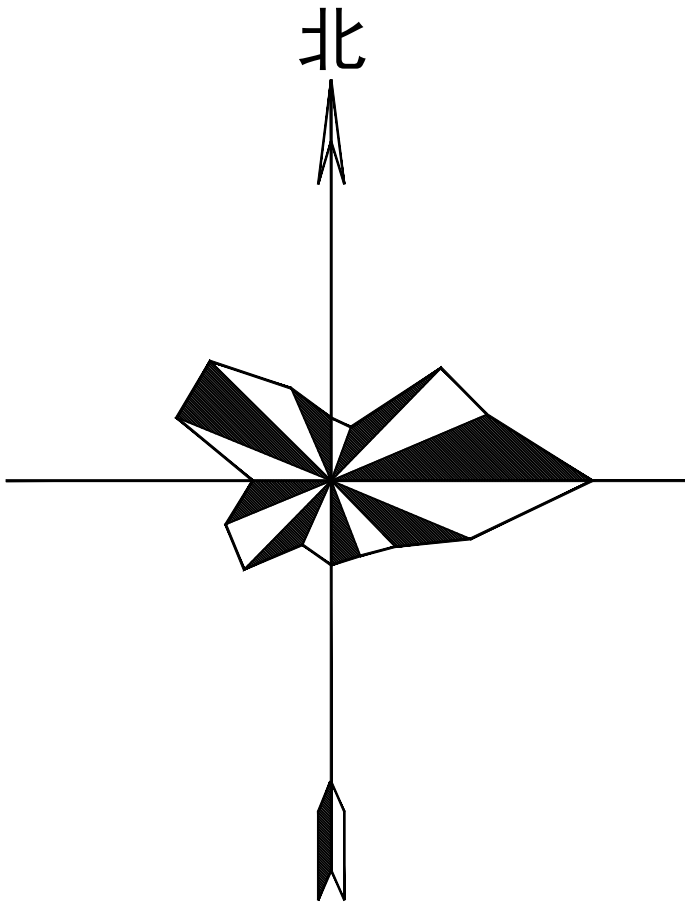
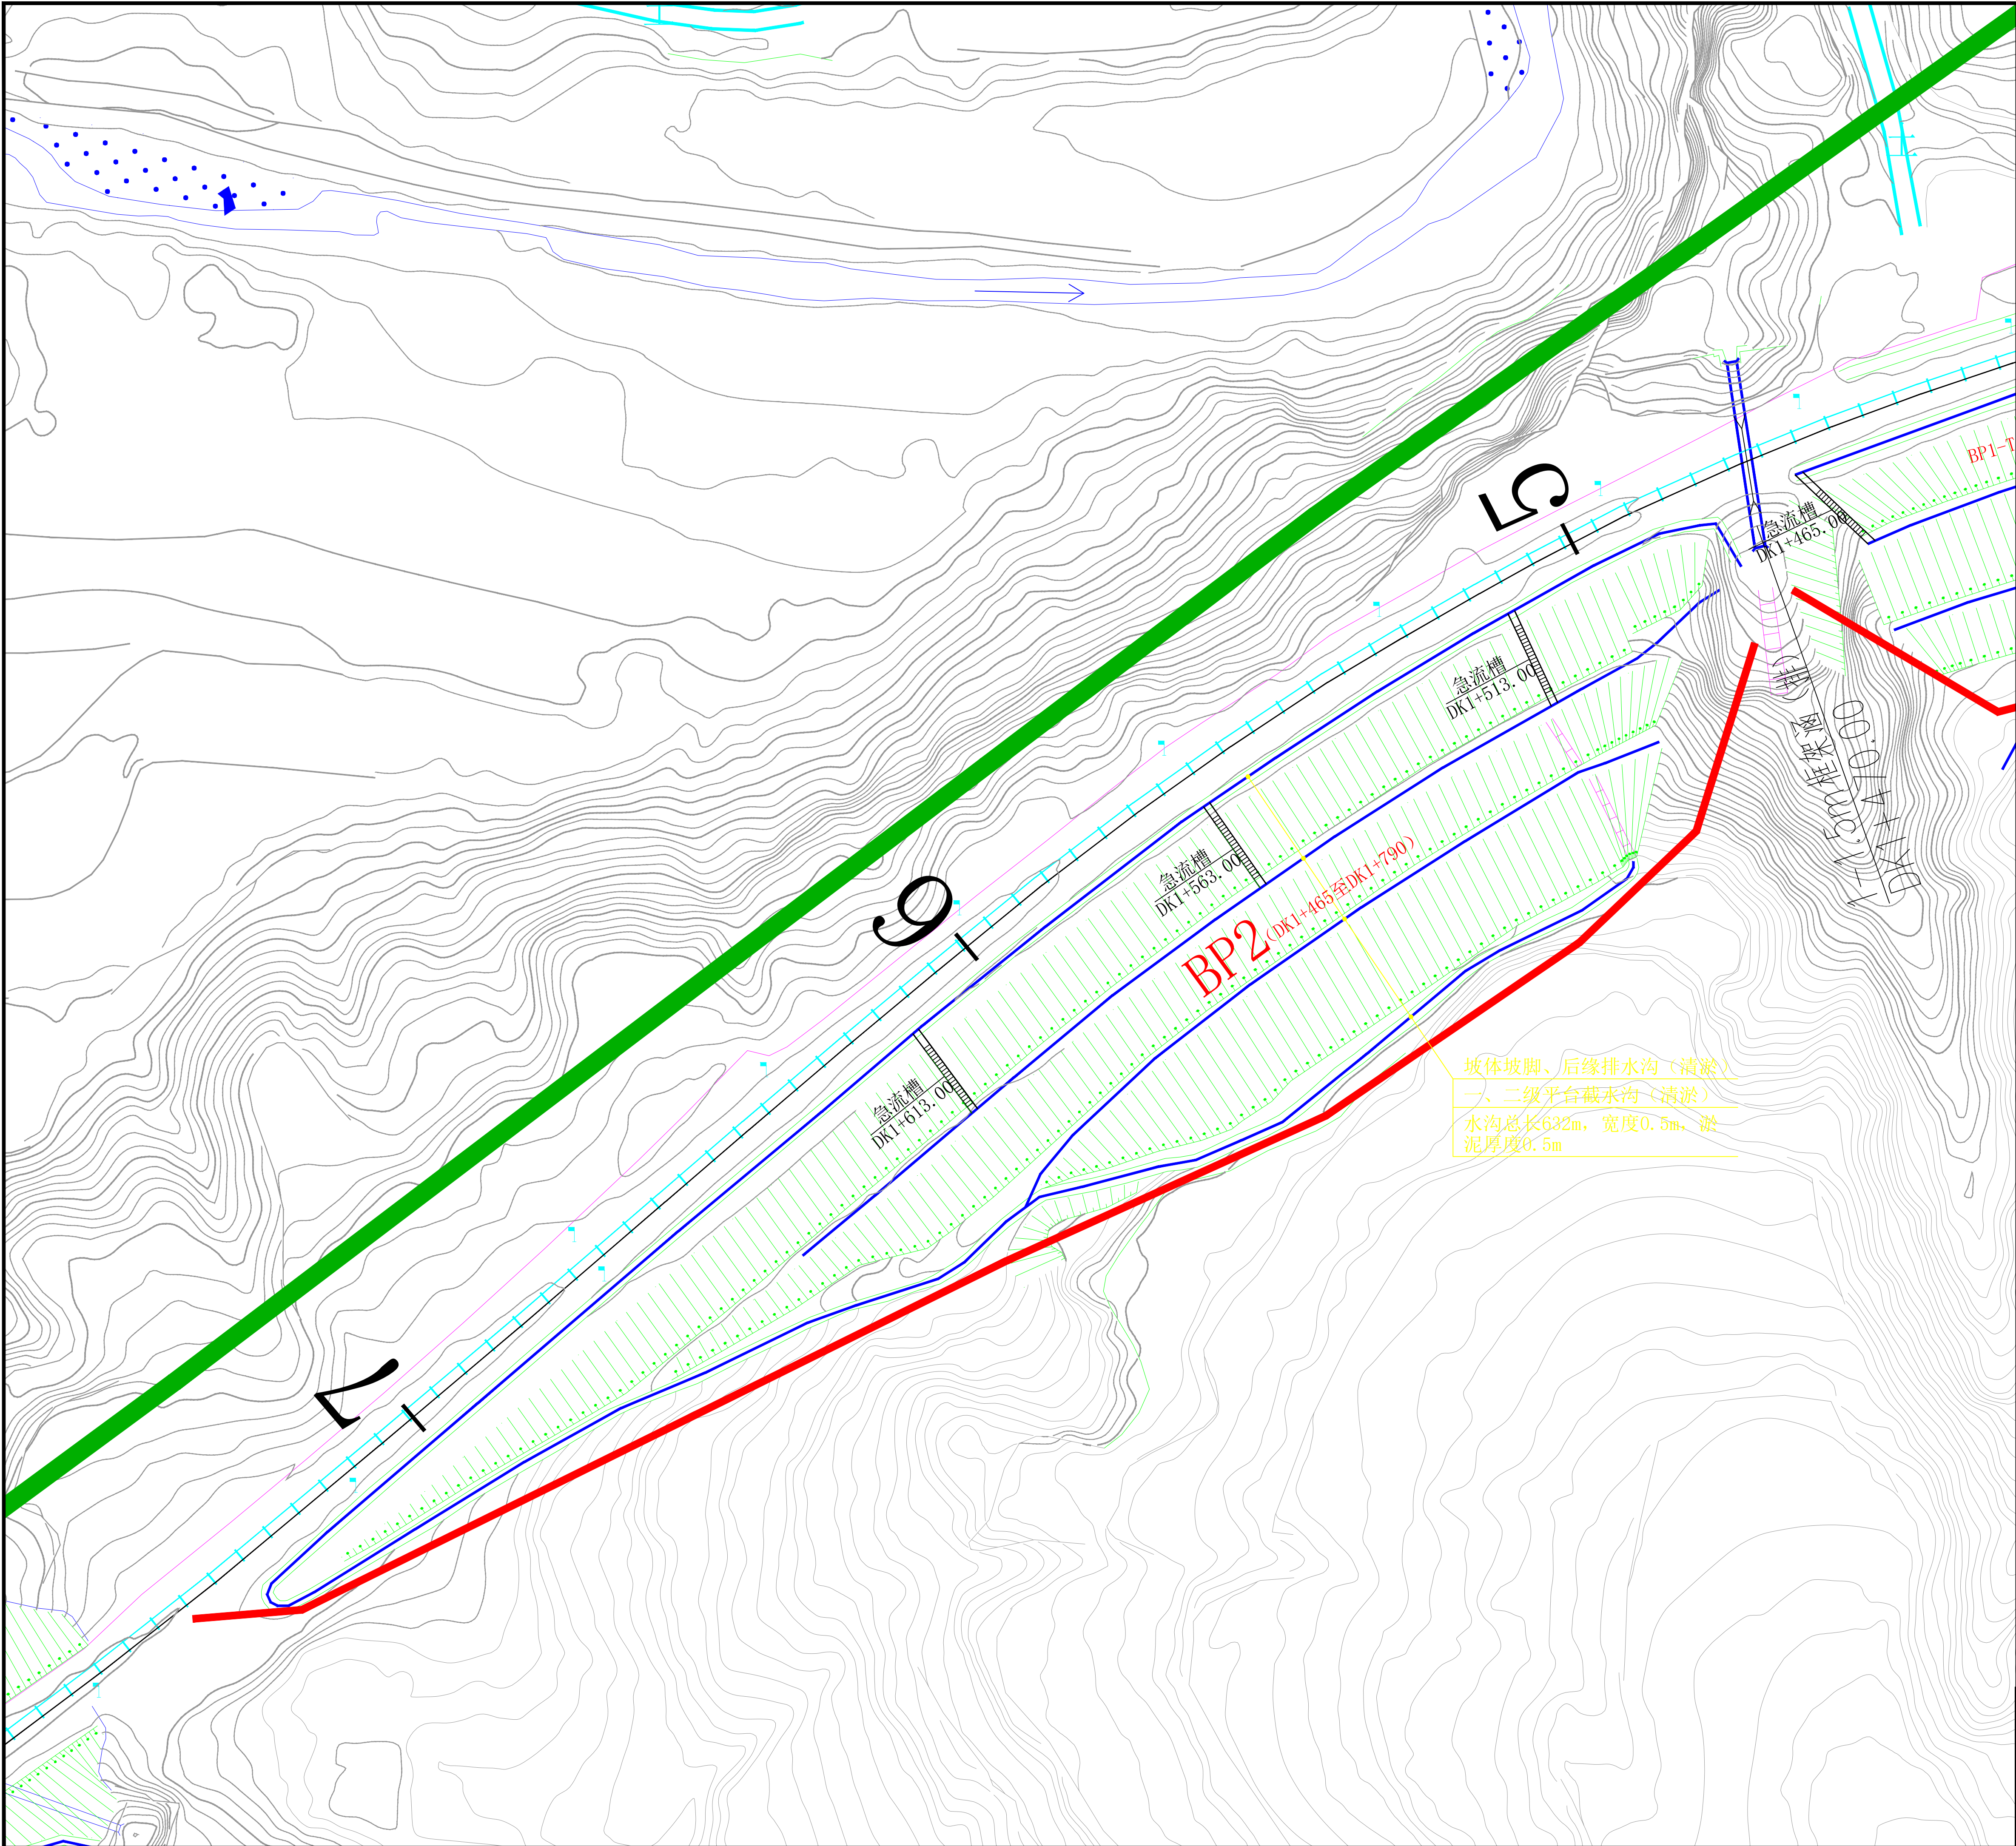


图 例:

- BP1 边坡范围及编号
- BP1 塌陷治理区域及编号
- 原状边坡示坡线
- 新建截(排)水沟
- 急流槽
- 已有建、构筑物
- 已有截(排)水沟
- 涵洞
- 线路及公里标
- 调查区范围

山西文龙中美环能科技股份有限公司									
太原燃气化龙泉能源发展有限公司铁路沿线边坡维修处治工程									
技术专用章									
标记	数量	修改者	批准者	日期	证书等级	证书编号	S1424-1951(2)-01		
设计	1	张明	张明	2025.10	铁路专用线	BP2 (DK1+465至DK1+790)	共 3 页	规 格	比 例
检查	1	煤炭行业工程	煤炭行业工程	2025.10	乙级	A214001459	第 1 页	A1	1: 500
审定	1	建筑行业工程	建筑行业工程	2025.10	乙级	A214001459	山西文龙中美环能科技股份有限公司		
2025年 10 月编制							总平面布置图		