
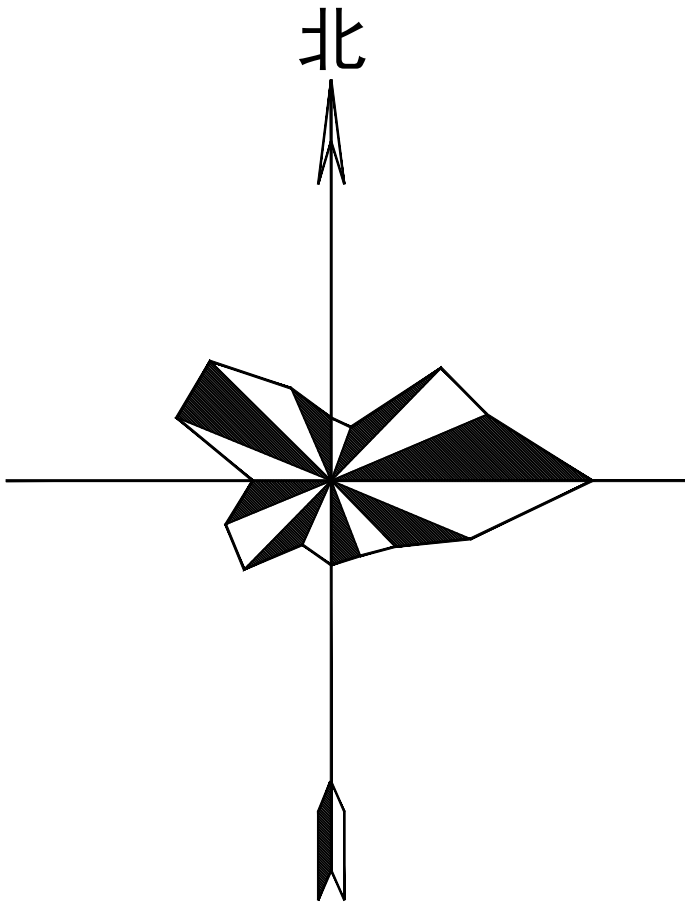


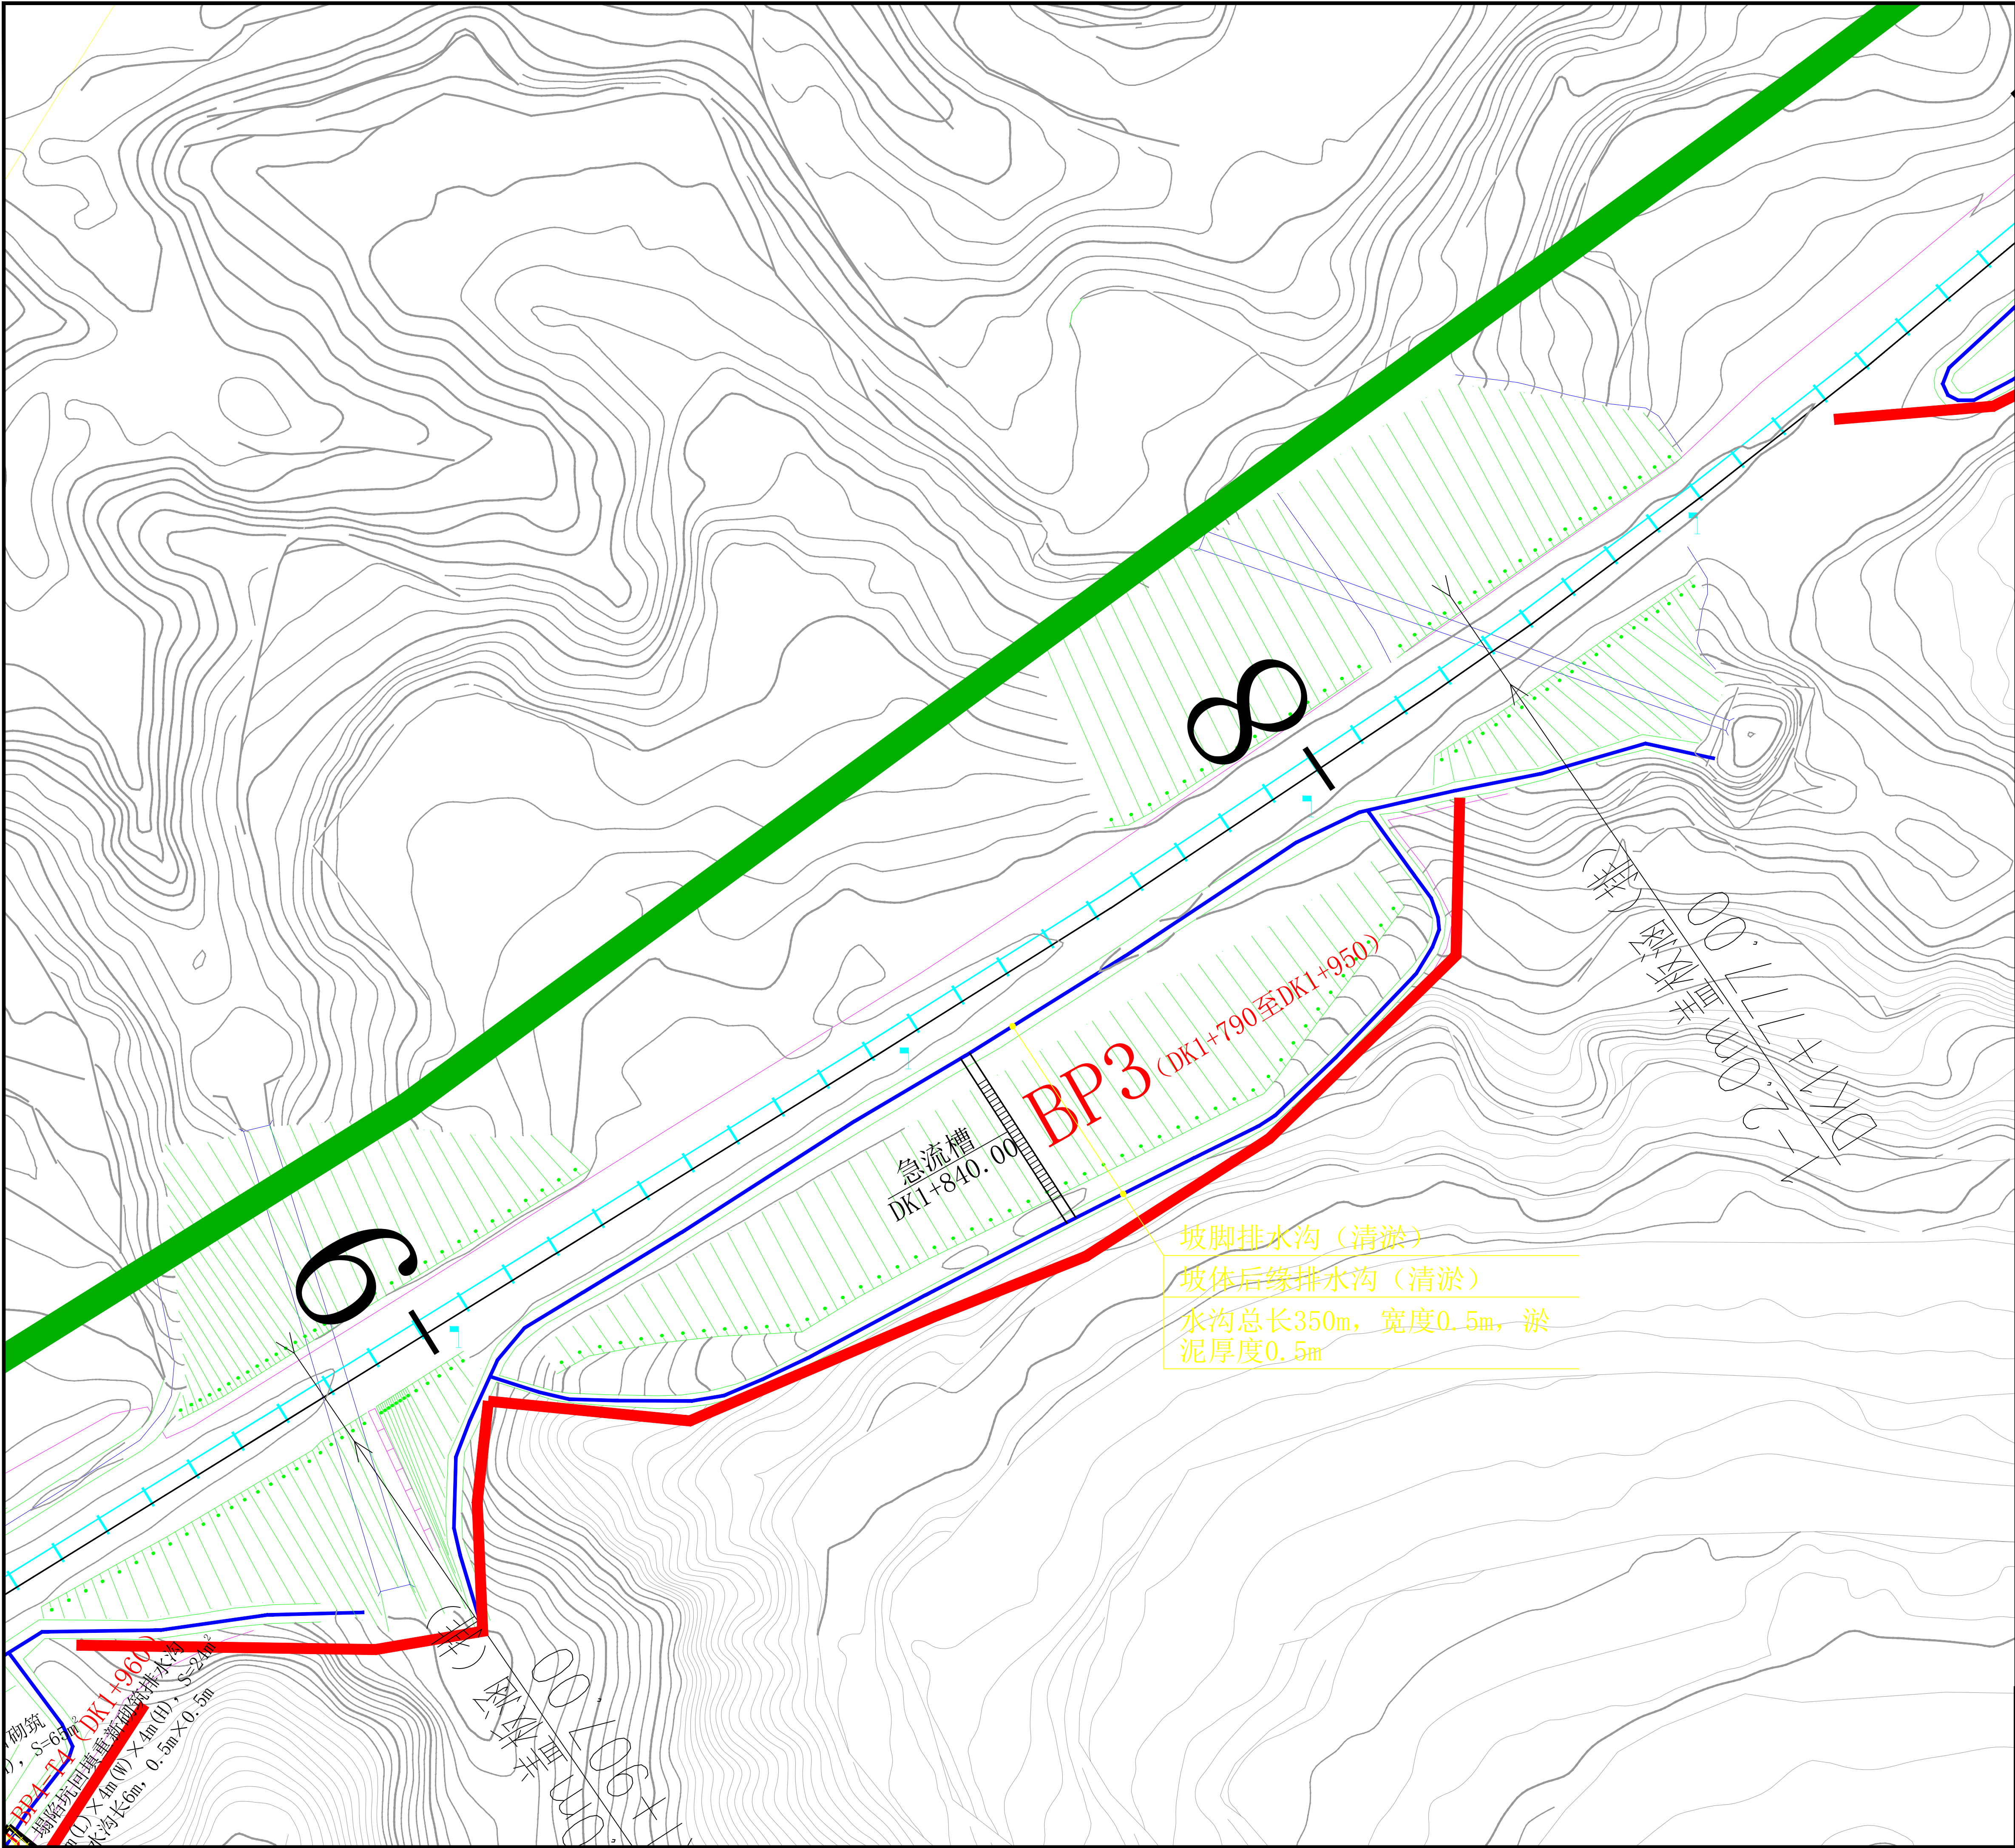

图例：

- BP1 边坡范围及编号
- BP1 塌陷治理区域及编号
- 原状边坡坡线
- 新建截（排）水沟
- 急流槽
- 已有建、构筑物
- 已有截（排）水沟
- 涵洞
- 线路及公里标
- 调查区范围

山西文龙中美环能科技股份有限公司									
技术负责人									
太原煤气化龙泉能源发展有限公司铁路沿线边坡维修处治工程									
标记	数量	修改者	批准者	日期	证书编号	资质等级	证书编号	S1424-1951(3)-01	
设计		设计	项目负责	设计	设计	设计	设计	铁路专用线	
检查		检查	检查	检查	检查	检查	检查	BP3 (DK1+790至DK1+950)	
审定		审定	审定	审定	审定	审定	审定	共 3 页 规格 比 例	
2023年 10 月编制								第 1 页 A1 1: 500	
总平面图								山西文龙中美环能科技股份有限公司	
								(原名：山西文龙煤矿工程股份有限公司)	