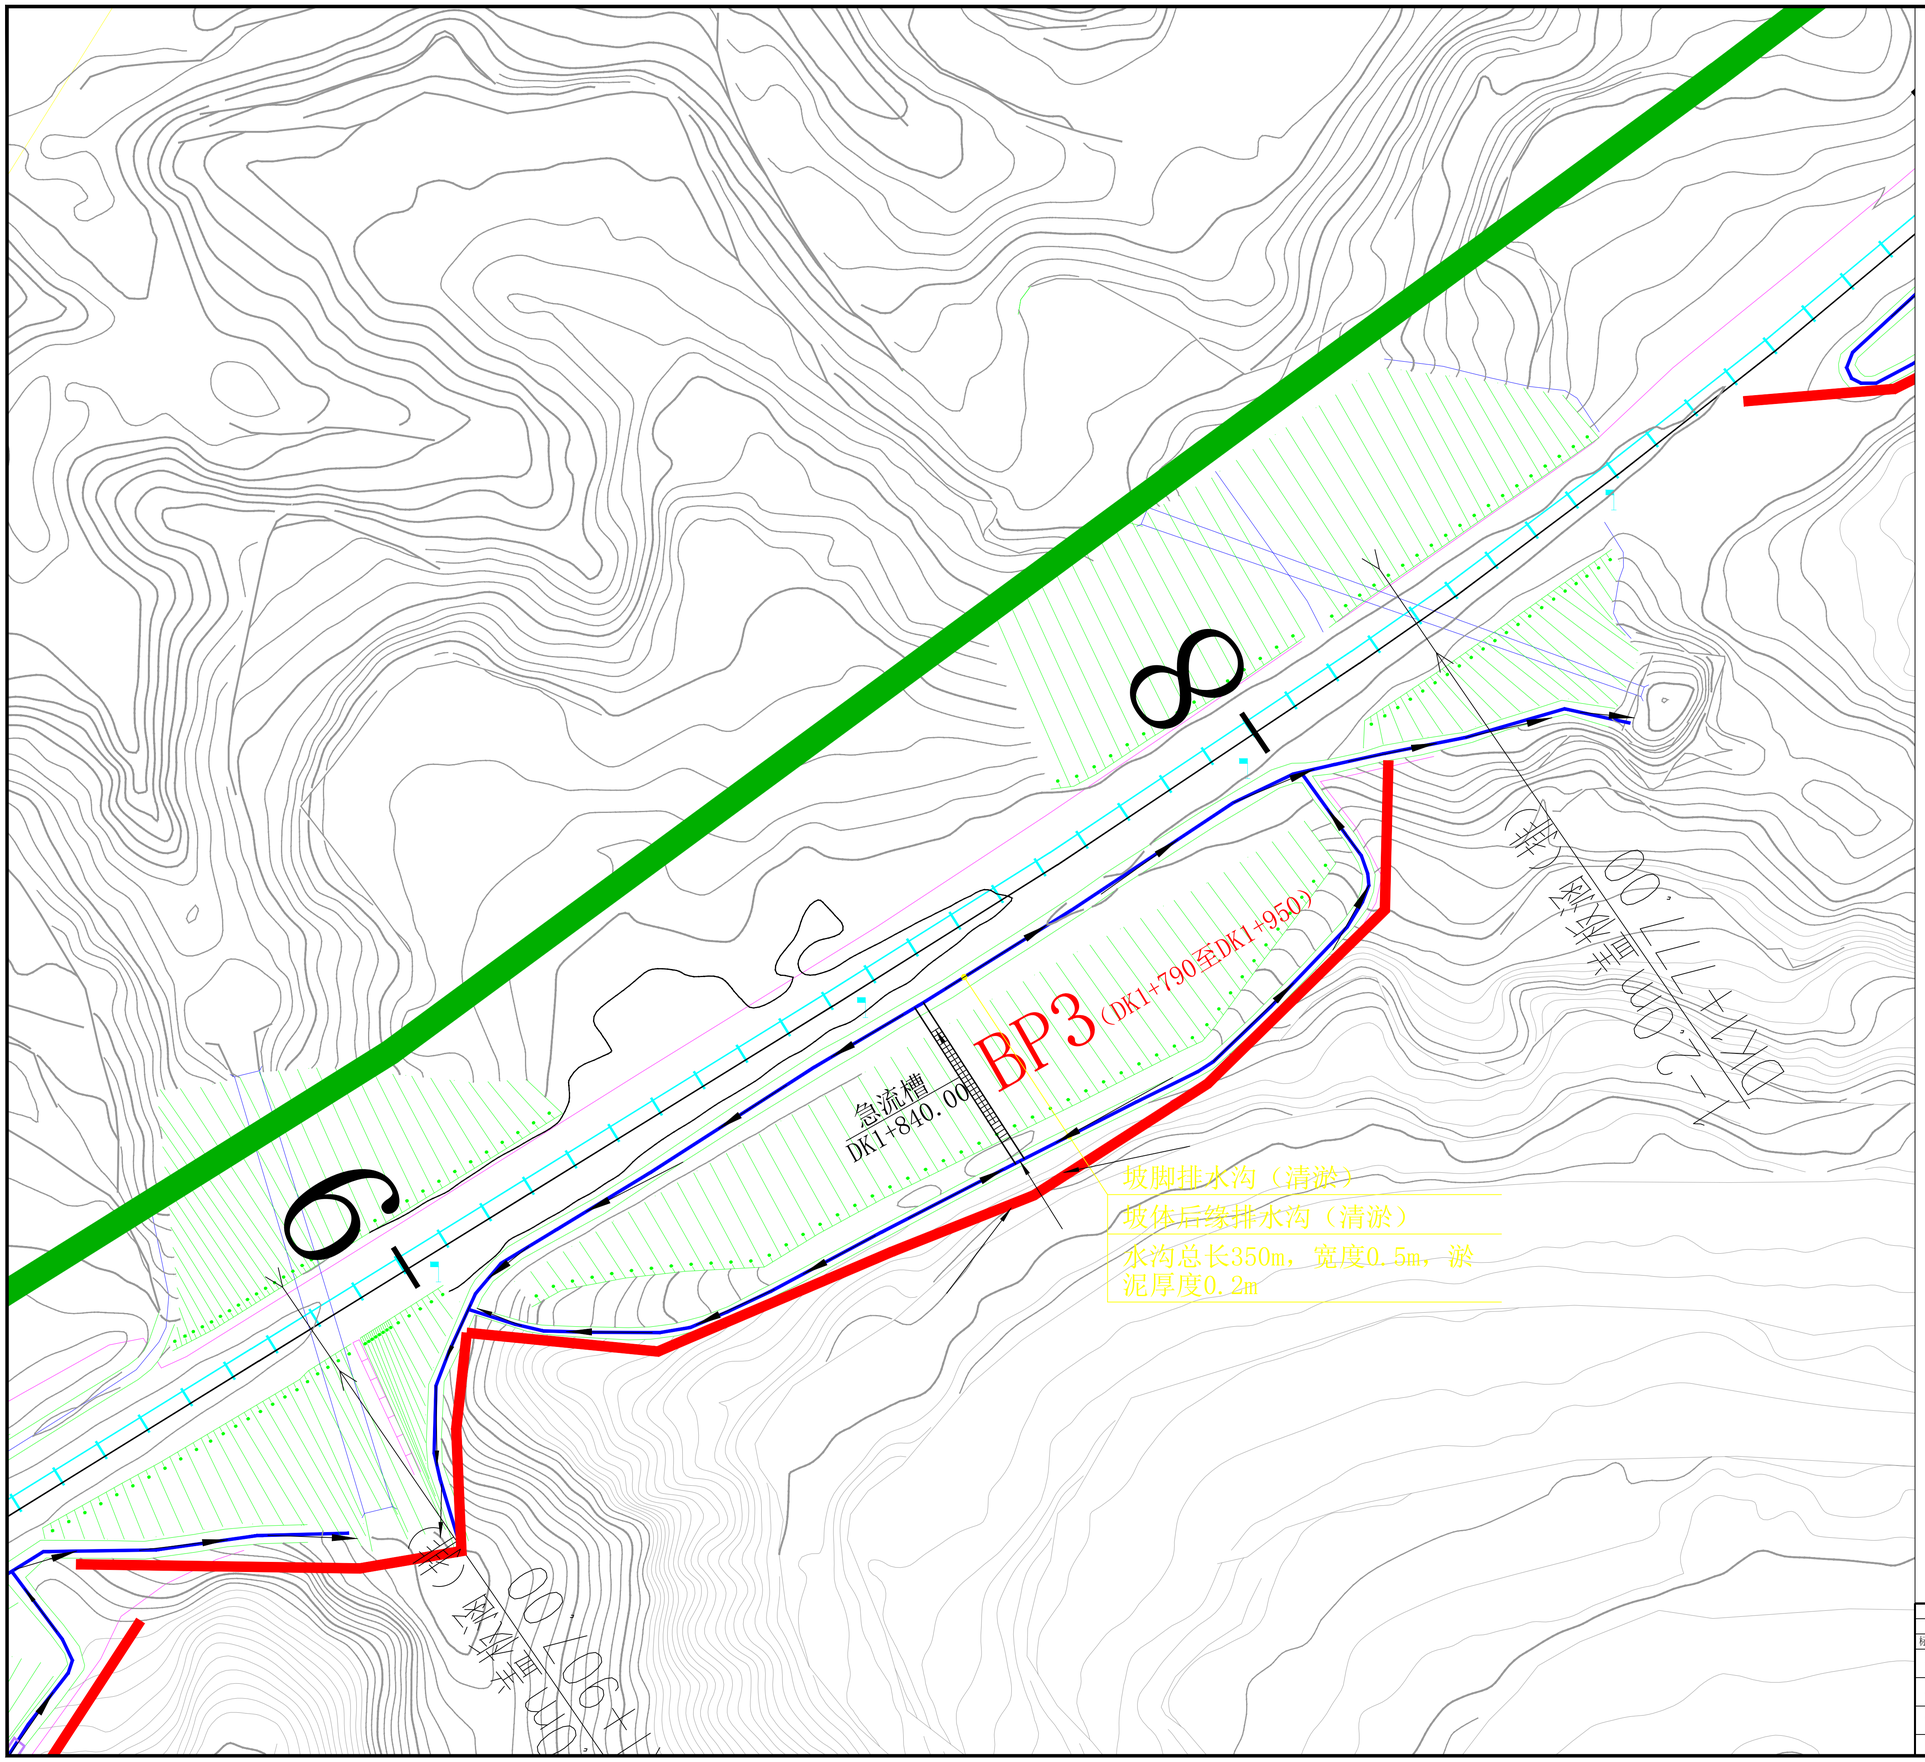


图 例：

- 新建截（排）水沟
- 急流槽
- 已有截（排）水沟
- 涵洞
- 排水方向

说明：

1、排水系统设置遵循“分级拦截、分段疏导、快速排出、防止冲刷”的原则。

2、截水沟：坡顶、平台设置截水沟，拦截坡顶及平台上方及平台汇集的地表水流，防止水流直接冲刷边坡坡面，避免雨水渗入坡体。坡顶截水沟设置在坡顶以外3-5米处，各分级平台排水沟设置在平台的外侧。

3、急流槽：平台间设置急流槽，快速疏导坡面汇水。急流槽设置在坡面汇水集中处、平台转角处或相随陡峭处。

4、排水措施以已有排水沟清淤疏通为主，上下平台间增设急流槽连通。

5、急流槽布设位置可根据现场实际情况进行调整。

6、其他未尽事项严格按现行国家规范标准执行。

山西文龙中美环能科技股份有限公司
技术专用章

标记	数量	修改者	批准者	日期	太原煤气化龙泉能源发展有限公司铁路沿线边坡维修处治工程		
设计			批准分类		资质等级	证书编号	S1424-1951(3)-02
检查			项目负责人		铁路专用线		
审定			总工程师		BP3（DK1+790至DK1+950）		共 3 页 规 格 比 例
			总经理		排水系统平面布置图		第 2 页 A1 1：500

2025年 10 月编制

山西文龙中美环能科技股份有限公司（原名：山西文龙煤矿工程设计有限公司）