

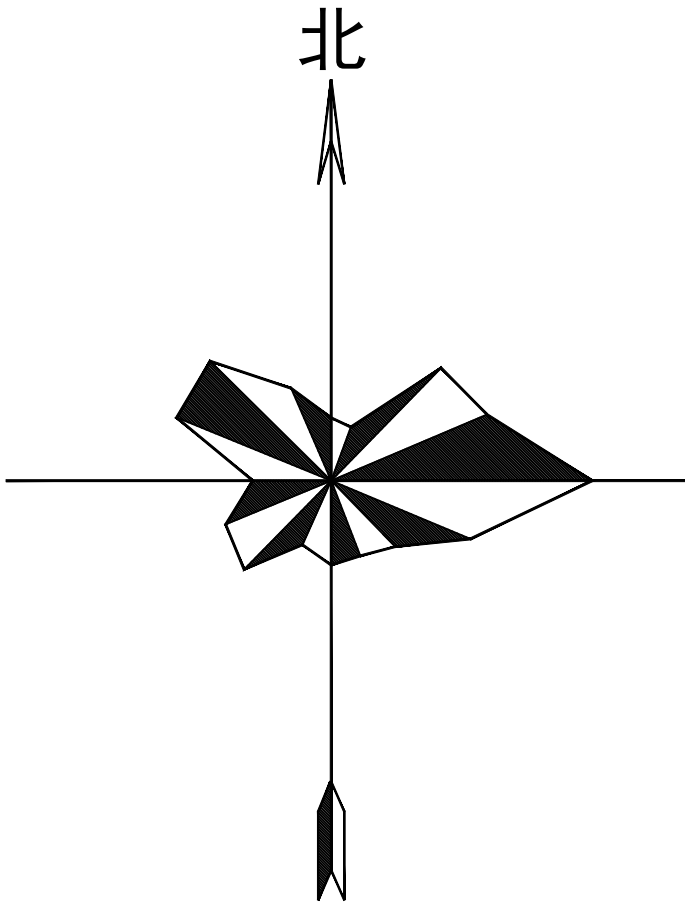
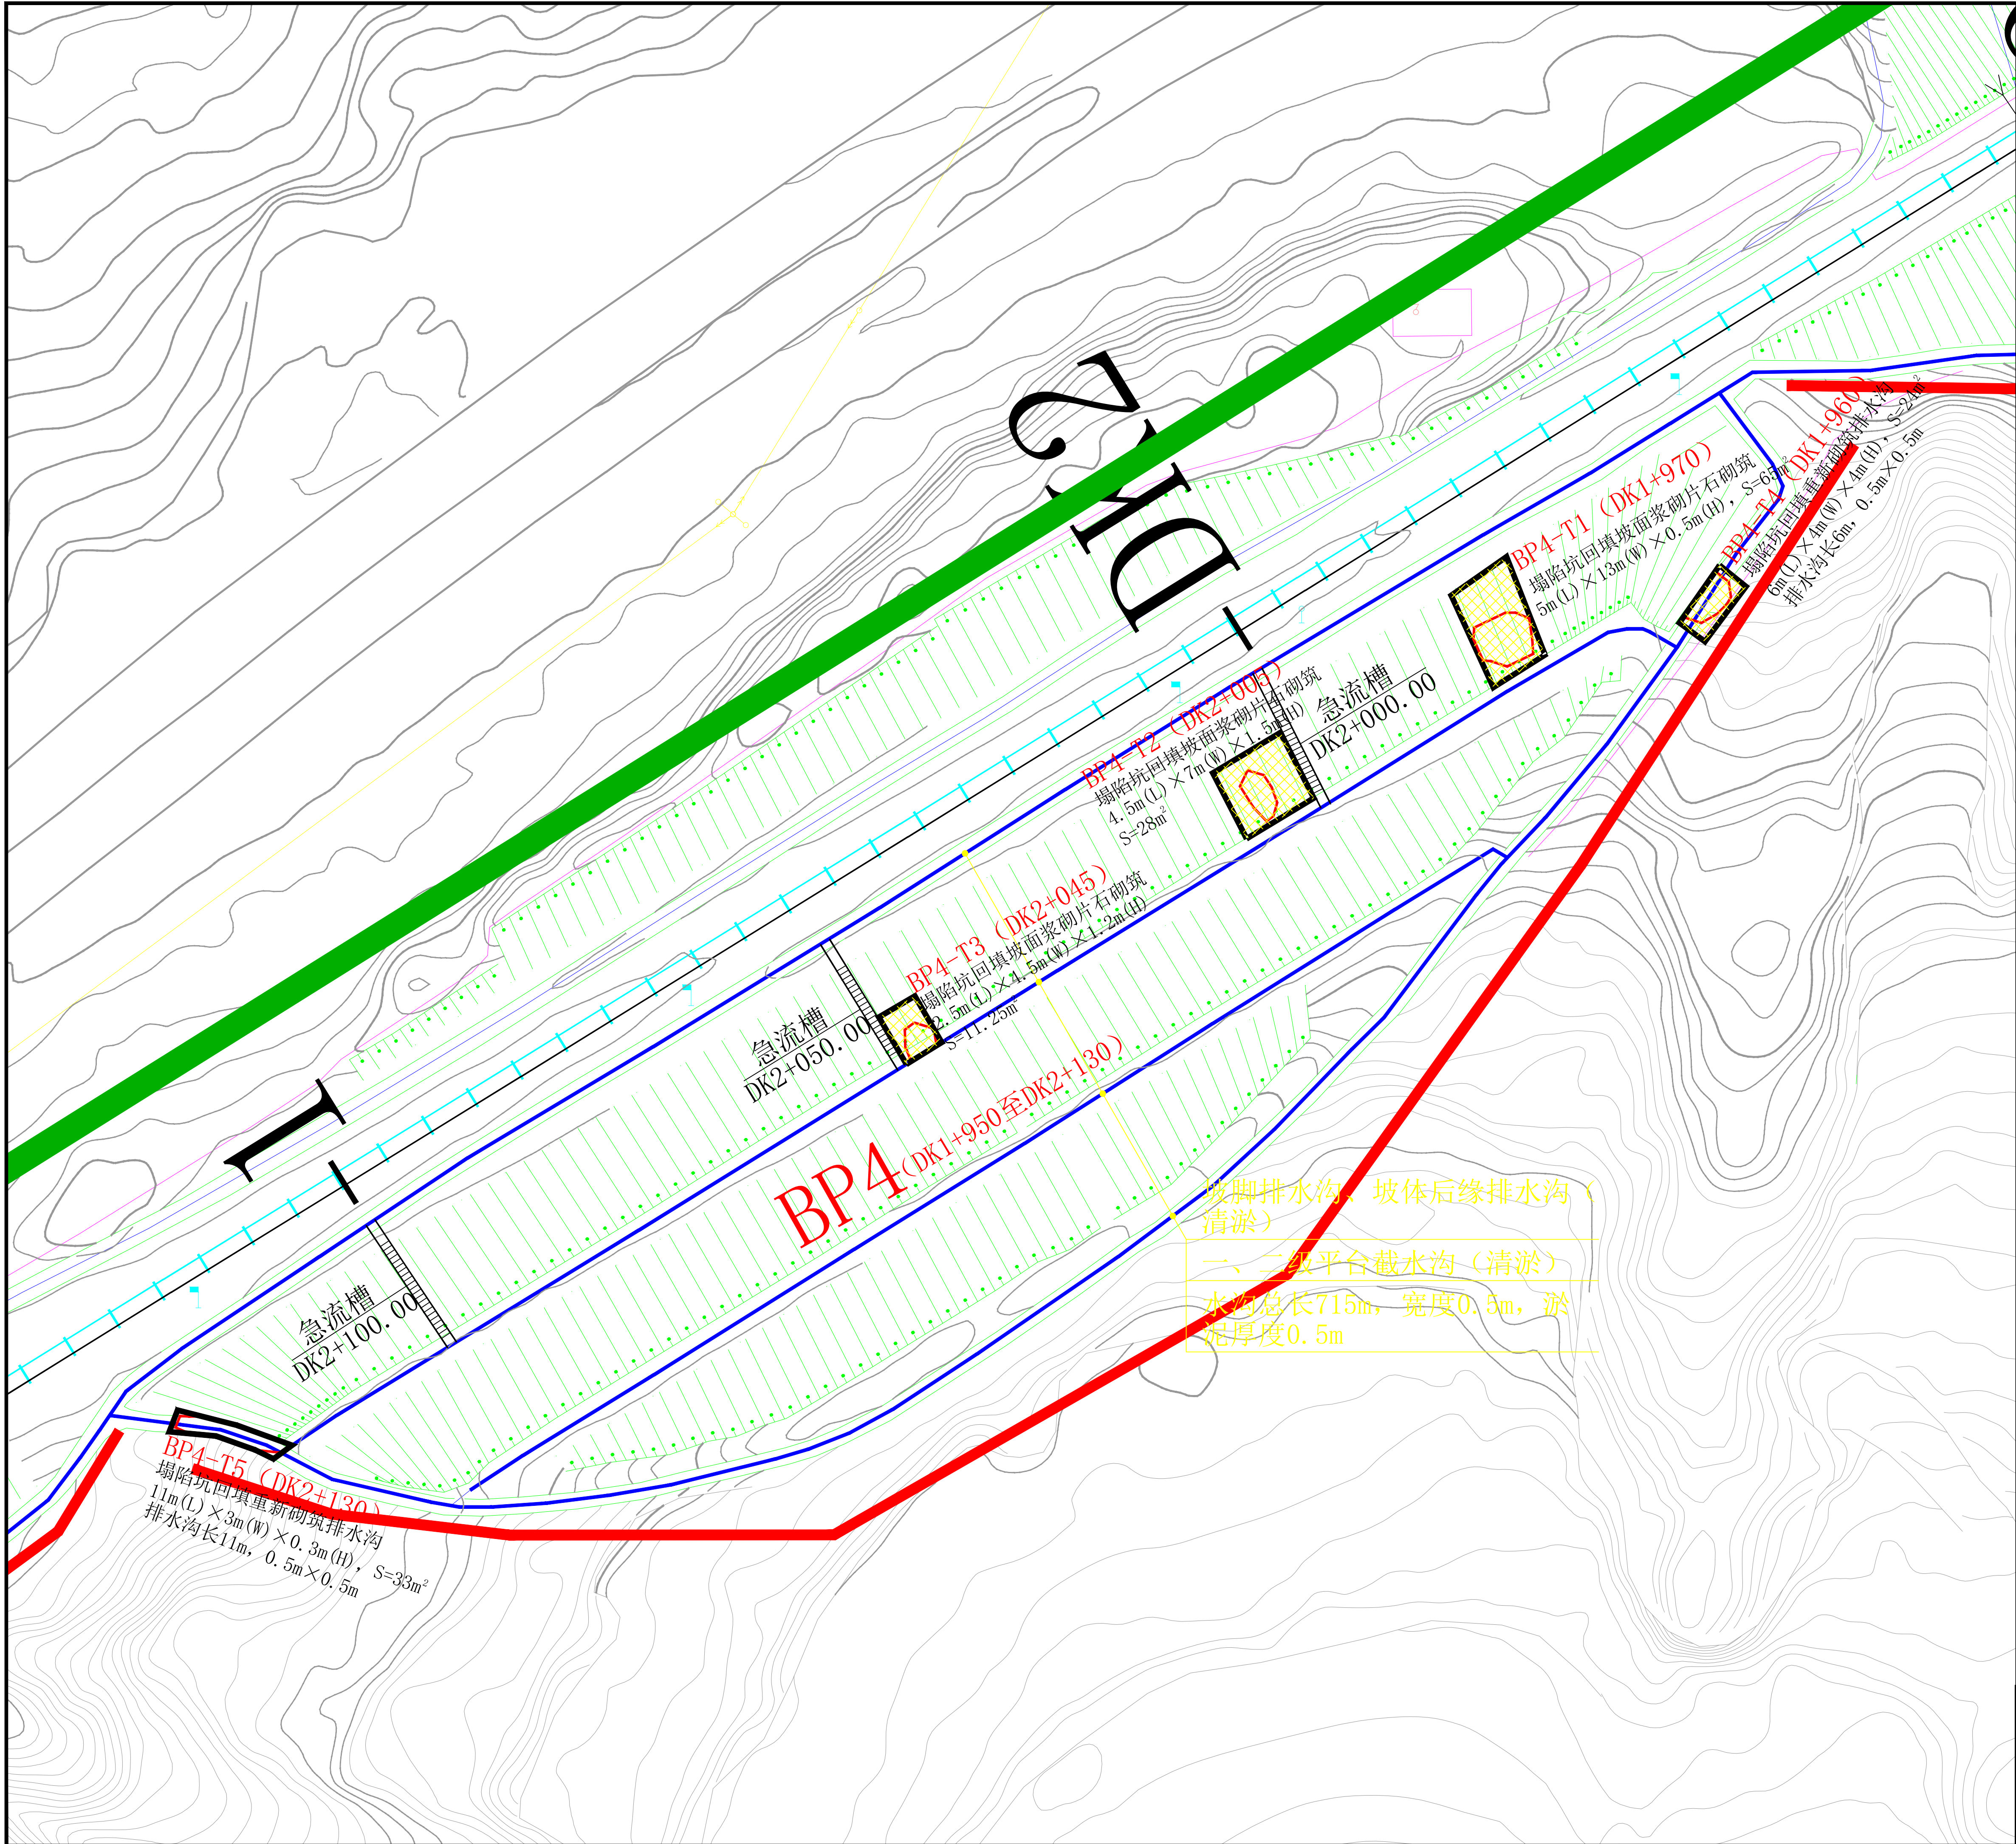


图 例:

- 边坡范围及编号
- 塌陷治理区域及编号
- 原状边坡示坡线
- 新建截（排）水沟
- 急流槽
- 已有建、构筑物
- 已有截（排）水沟
- 涵洞
- 线路及公里标
- 调查区范围

山西文龙中美环能科技股份有限公司									
技术专用章									
太原煤气化龙泉能源发展有限公司铁路沿线边坡维修处治工程									
标记	数量	修 改 者	数 量	日 期	修 改 等 级	证 书 编 号	S1424-1951(4)-01		
设 计	1	张 彬	1	2025.07.10	初 审	铁路专用线			
检 查	1	张 彬	1	2025.07.10	校 对	BP4 (DK1+950至DK2+130)	共 5 页	规 格	比 例
审 定	1	张 彬	1	2025.07.10	已 校	BP4总平面布置图	第 1 页	A1	1: 500
2025年 10 月 编制							 山西文龙中美环能科技股份有限公司 (原名: 山西文龙煤矿工程设计有限公司)		