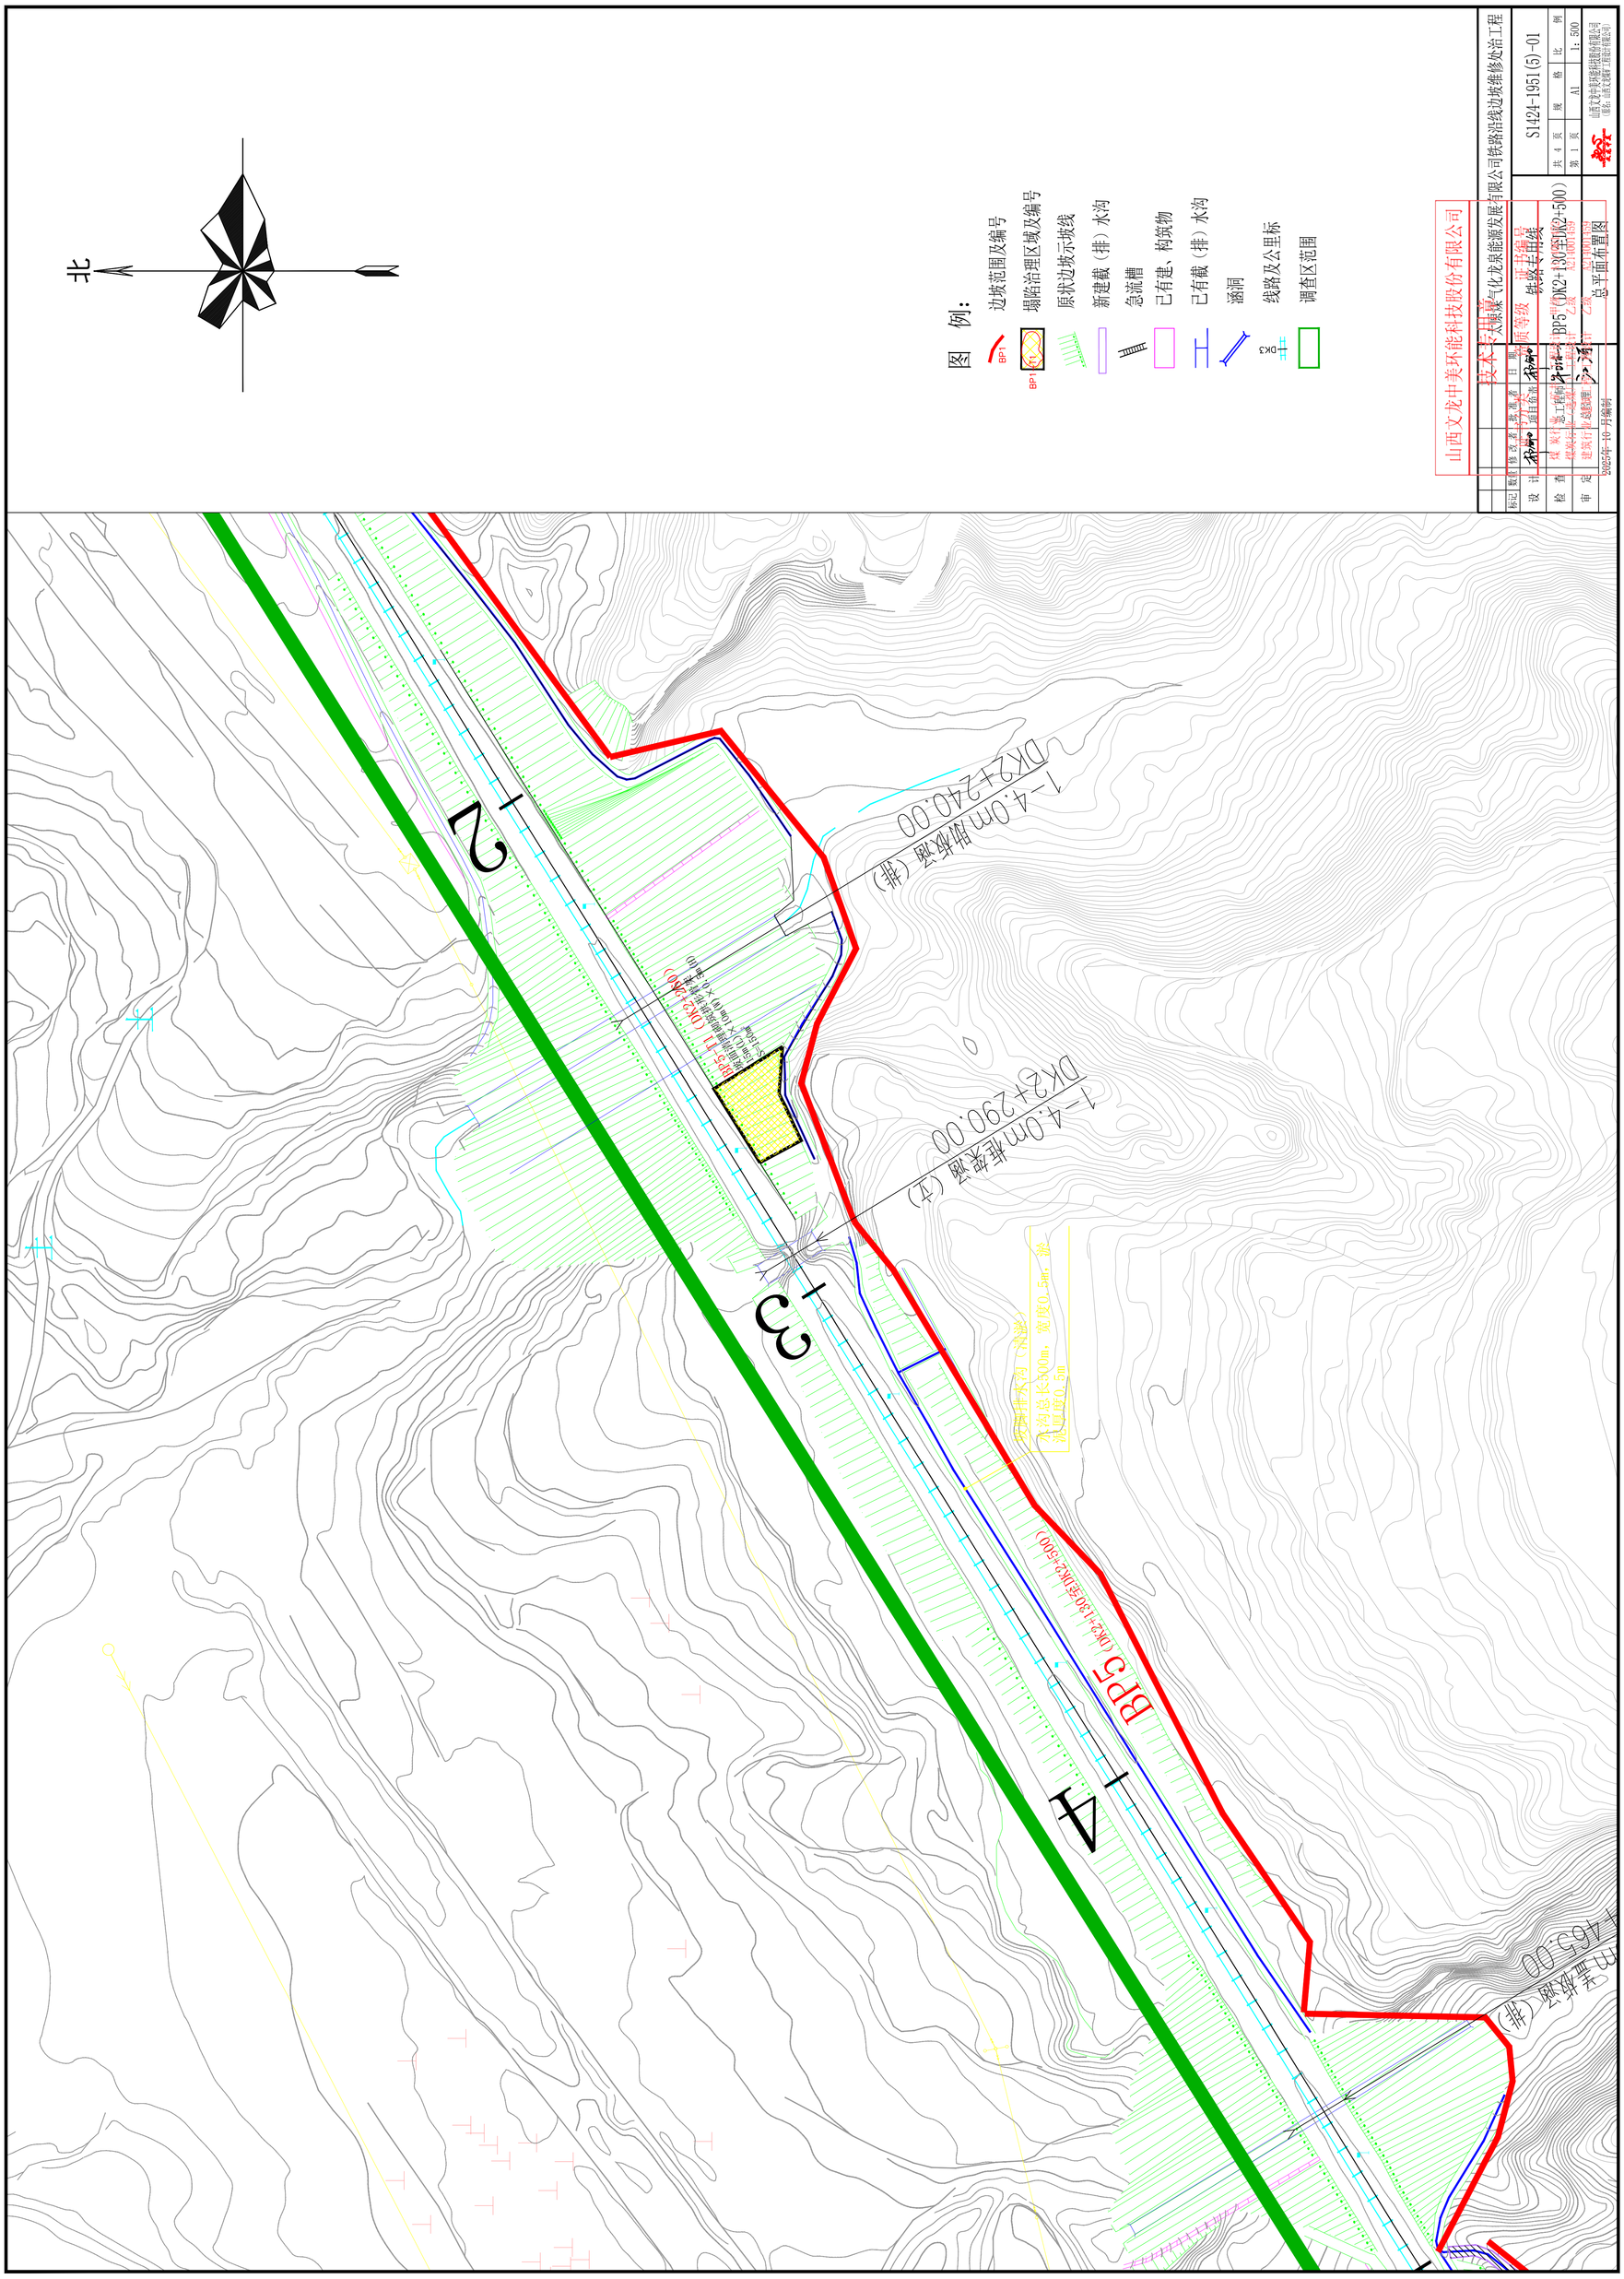

北
图 例:
边坡范围及编号
塌陷治理区域及编号
原状边坡示坡线
新建截（排）水沟
急流槽
已有建、构筑物
已有截（排）水沟
涵洞
线路及公里标
调查区范围
山西文龙中美环能科技股份有限公司
技术专用章
大源煤气化龙泉能源发展有限公司铁路沿线边坡维修处治工程
S1424-1951(5)-01
共 4 页
第 1 页
1:500
A1
总平面布置图
2025年10月编制
BP5
1-4.0m 拱桥涵（排）
DK2+240.00
1-4.0m 桩柴涵（立）
DK2+290.00