


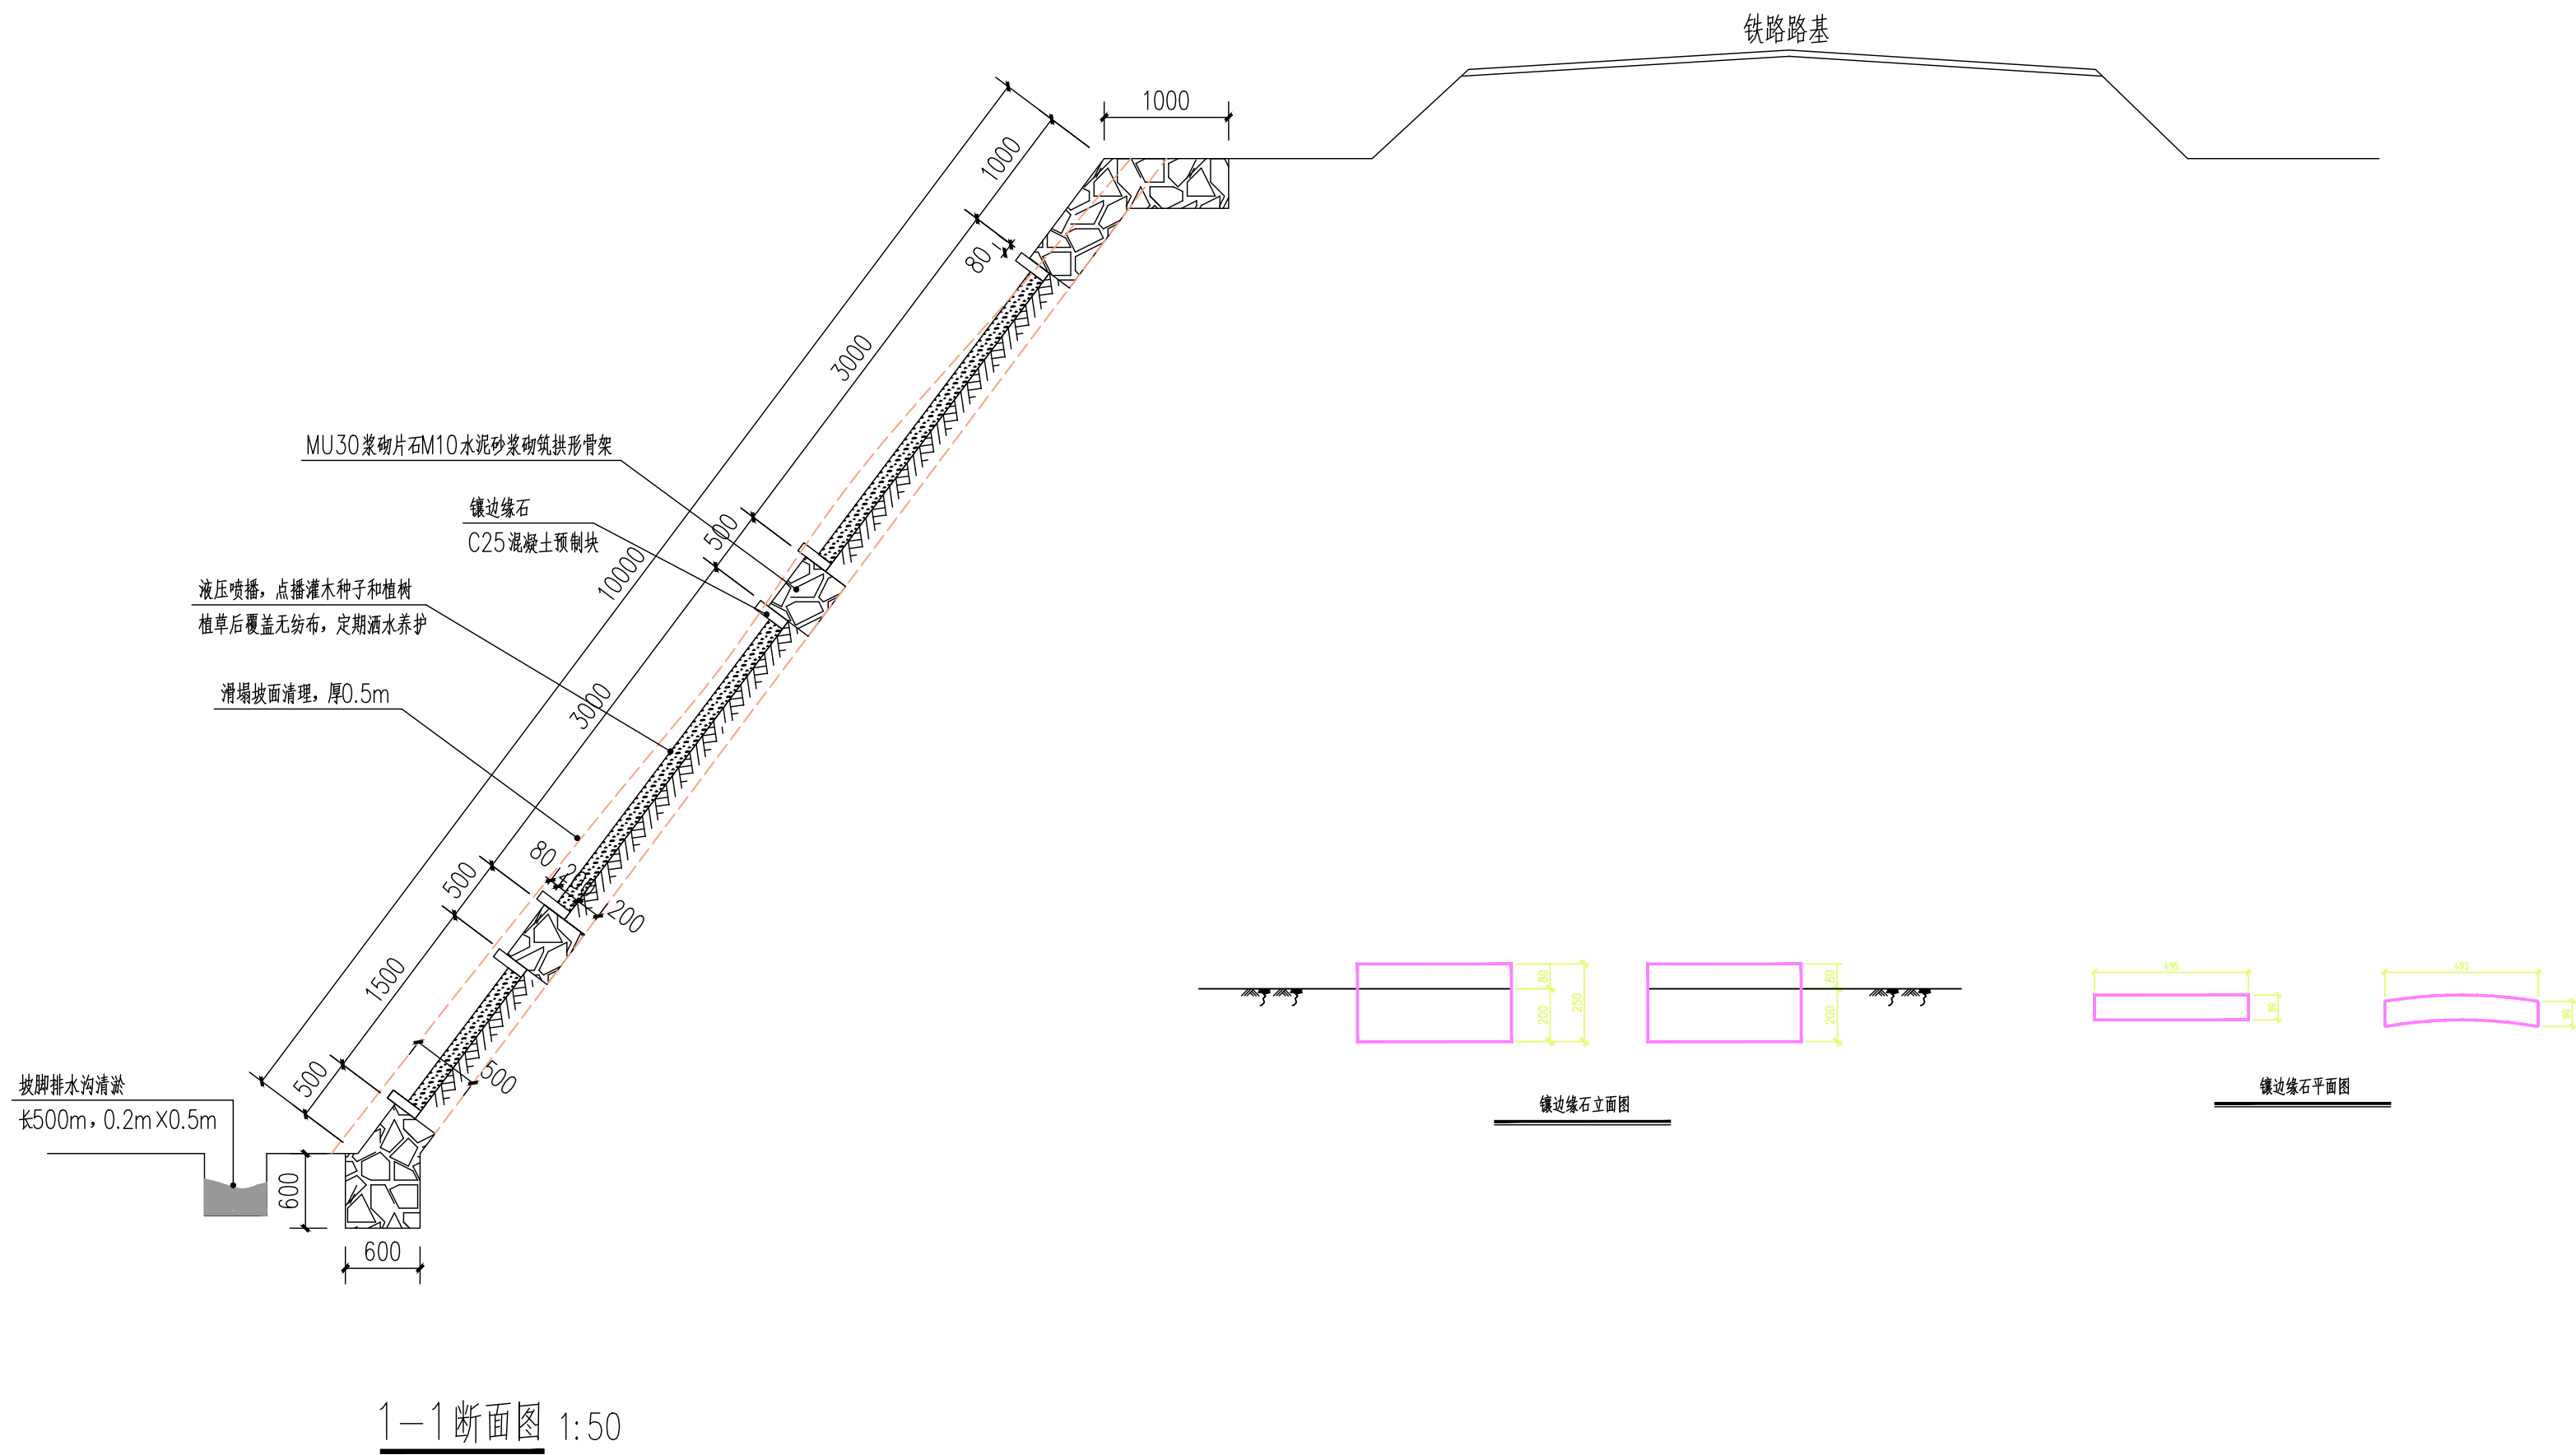

说明

- 1、本图尺寸均以mm计。
- 2、本断面为DK2+260-DK2+275段拱形骨架砌体滑塌重新修筑；
- 3、滑塌面层片石及碎石土清理，厚度500mm，重新采用M10砂浆砌筑MU30片石砌筑拱形骨架，厚度400mm，嵌入土层200mm；
- 4、液压喷播坡面，点播灌木种子和植树，植草后覆盖无纺布，定期洒水养护；
- 5、坡体坡脚排水沟目前存在淤堵，清淤后可正常排水，清除排水沟内淤泥，总长度500m，淤泥厚度0.2m，宽度0.5m。

山西文龙中美环能科技股份有限公司										太原煤气化龙泉能源发展有限公司铁路沿线边坡维修处治工程									
技术专用章										铁路专用线									
标记	数量	修改者	批准者	日期	审核等级	证书编号	S1424-1951(5)-04												
设计	1	张	张	2025.10	乙级	BP5-DK2+130至DK2+500	共 4 页												
检查	1	张	张	2025.10	乙级	421400139	第 4 页												
审定	1	张	张	2025.10	乙级	421400139	1-1断面图												
2025年10月编制										山西文龙中美环能科技股份有限公司 (原名：山西文龙煤矿工程设计有限公司)									