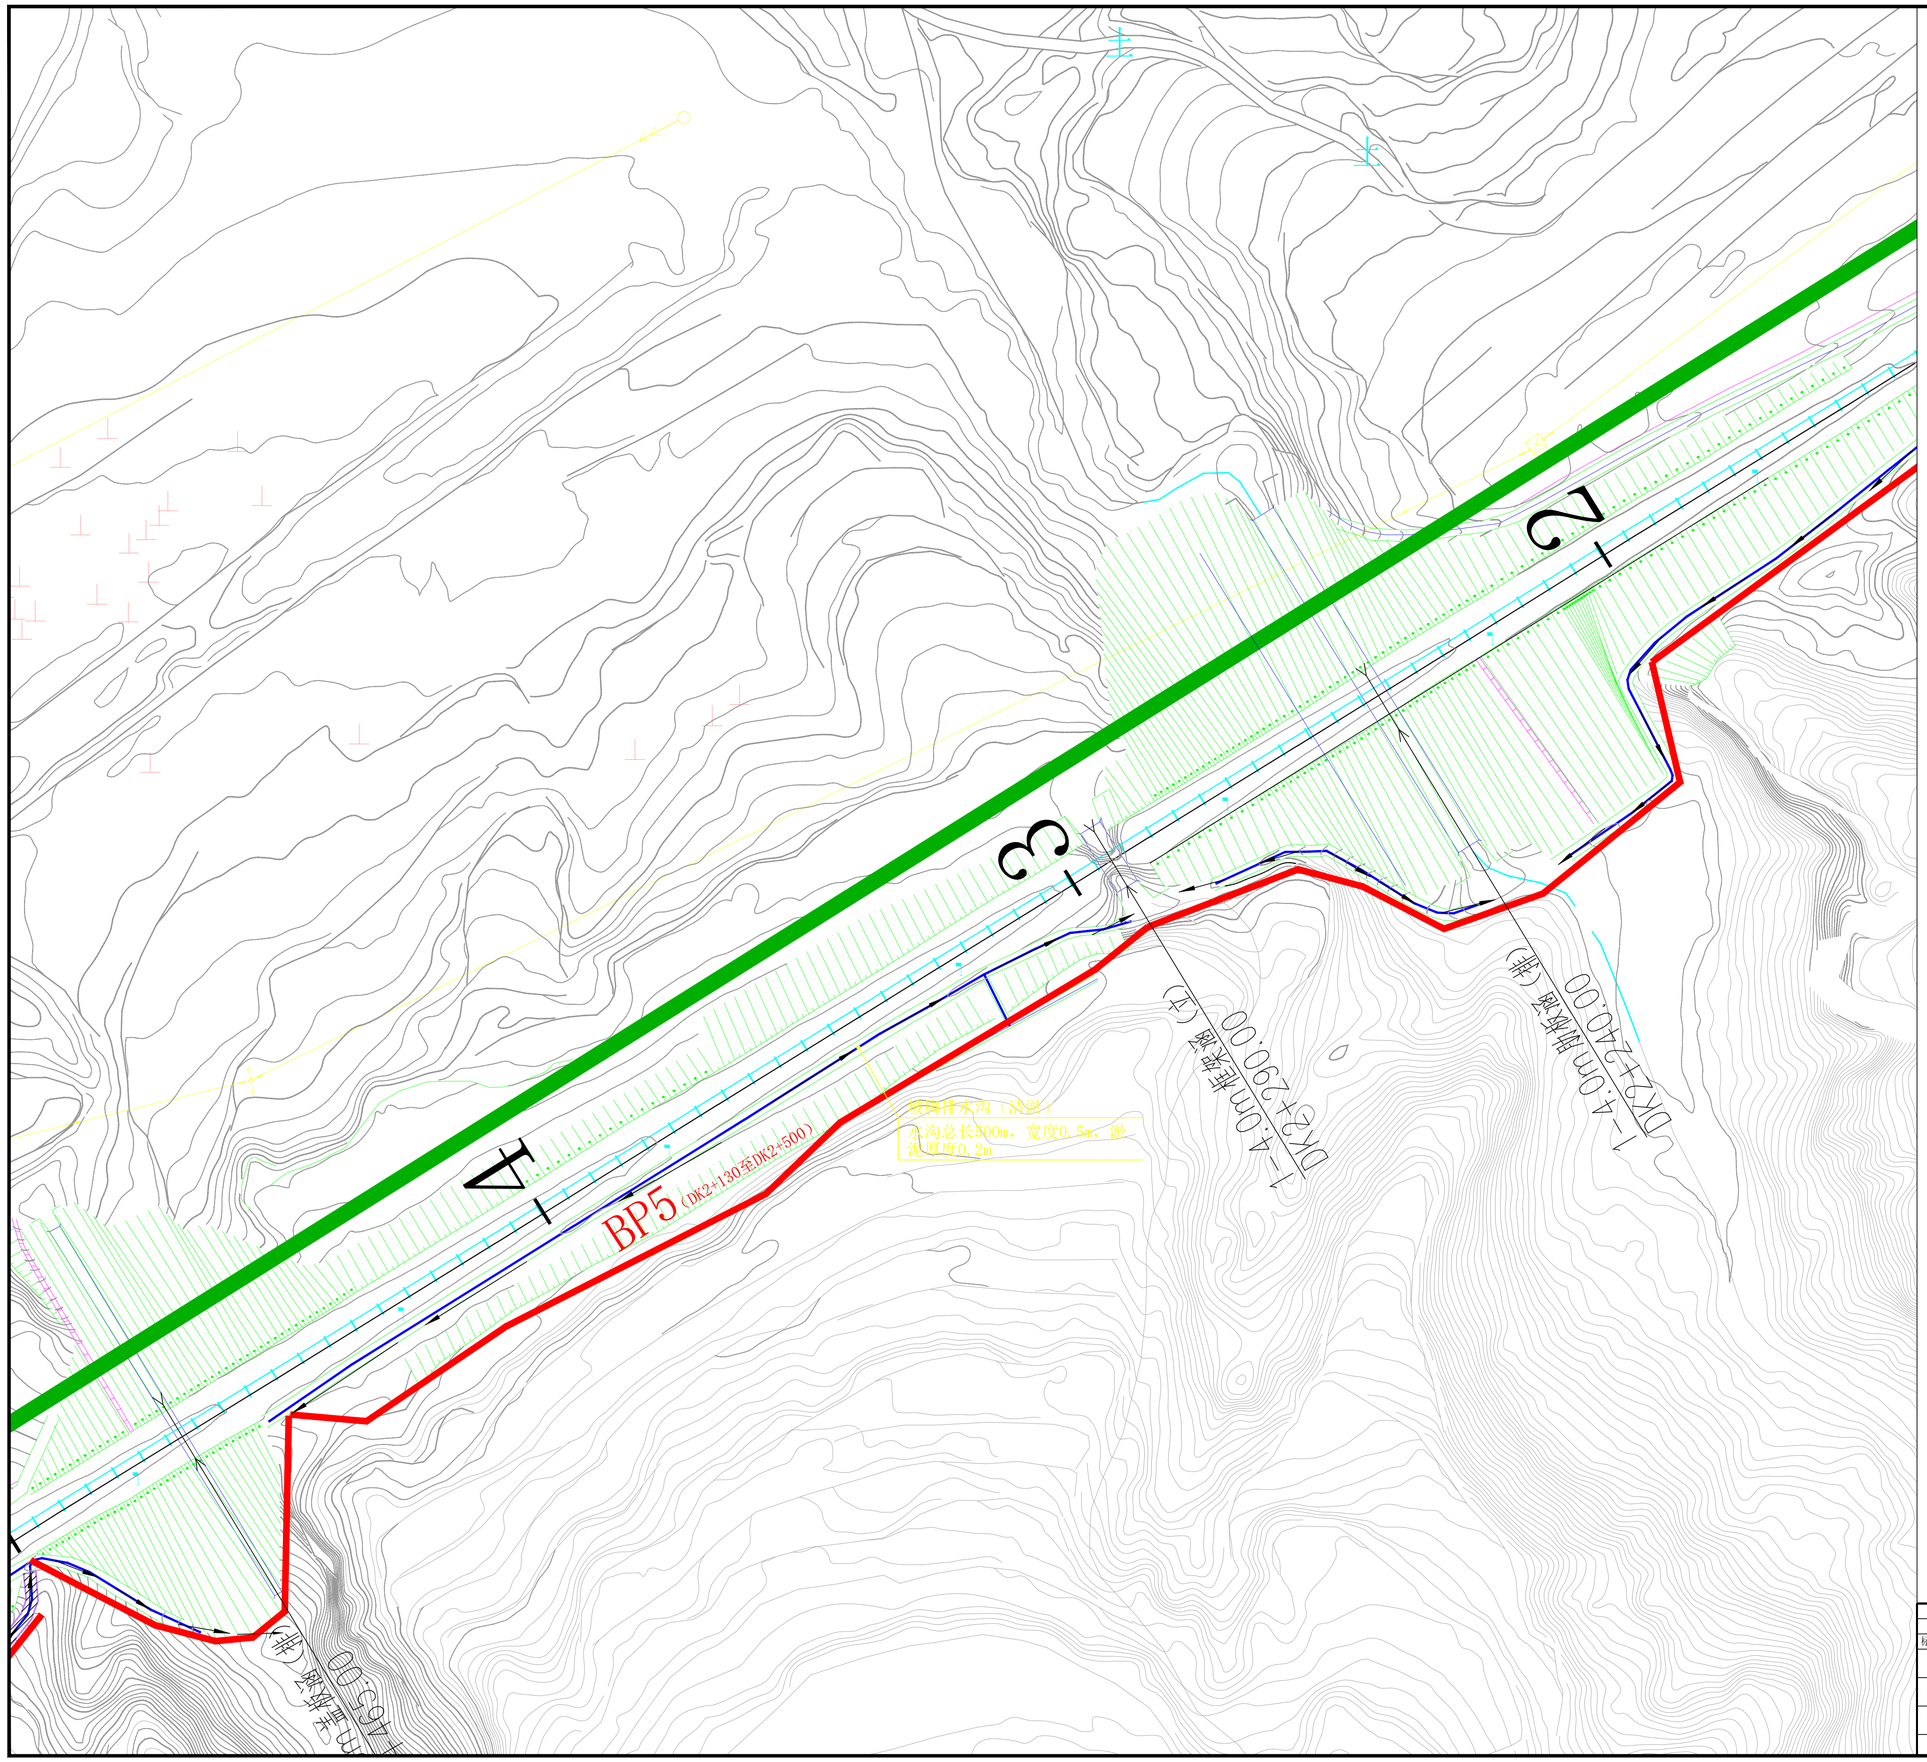

说明：

1、排水系统设置遵循“分级拦截、分段疏导、快速排出、防止冲刷”的原则。

2、截水沟：坡顶、平台设置截水沟，拦截坡顶及平台上方及平台汇集的地表水流，防止水流直接冲刷边坡坡面，避免雨水渗入坡体。坡顶截水沟设置在坡顶以外3-5米处，各分级平台排水沟设置在平台的外侧。

3、急流槽：平台间设置急流槽，快速疏导坡面汇水。急流槽设置在坡面汇水集中处、平台转角处或相随陡峭处。

4、排水措施以已有排水沟清淤疏通为主，上下平台间增设急流槽连通。

5、急流槽布设位置可根据现场实际情况进行调整。

6、其他未尽事项严格按现行国家规范标准执行。

山西文龙中美环能科技股份有限公司

技术专用章

资质等级 证书编号

标记	数量	修改者	批准者	日期
设计		项目负责		
检查		煤炭总工程师		
审定		总经理		

2025年 10 月编制

太原煤气化龙泉能源发展有限公司铁路沿线边坡维修处治工程

铁路专用线

BP5（DK2+130至DK2+500）

排水系统平面布置图

S1424-1951(5)-02			
共 4 页 第 2 页	规格 A1	比例 1:500	

山西文龙中美环能科技股份有限公司
（原名：山西文龙煤矿工程设计有限公司）