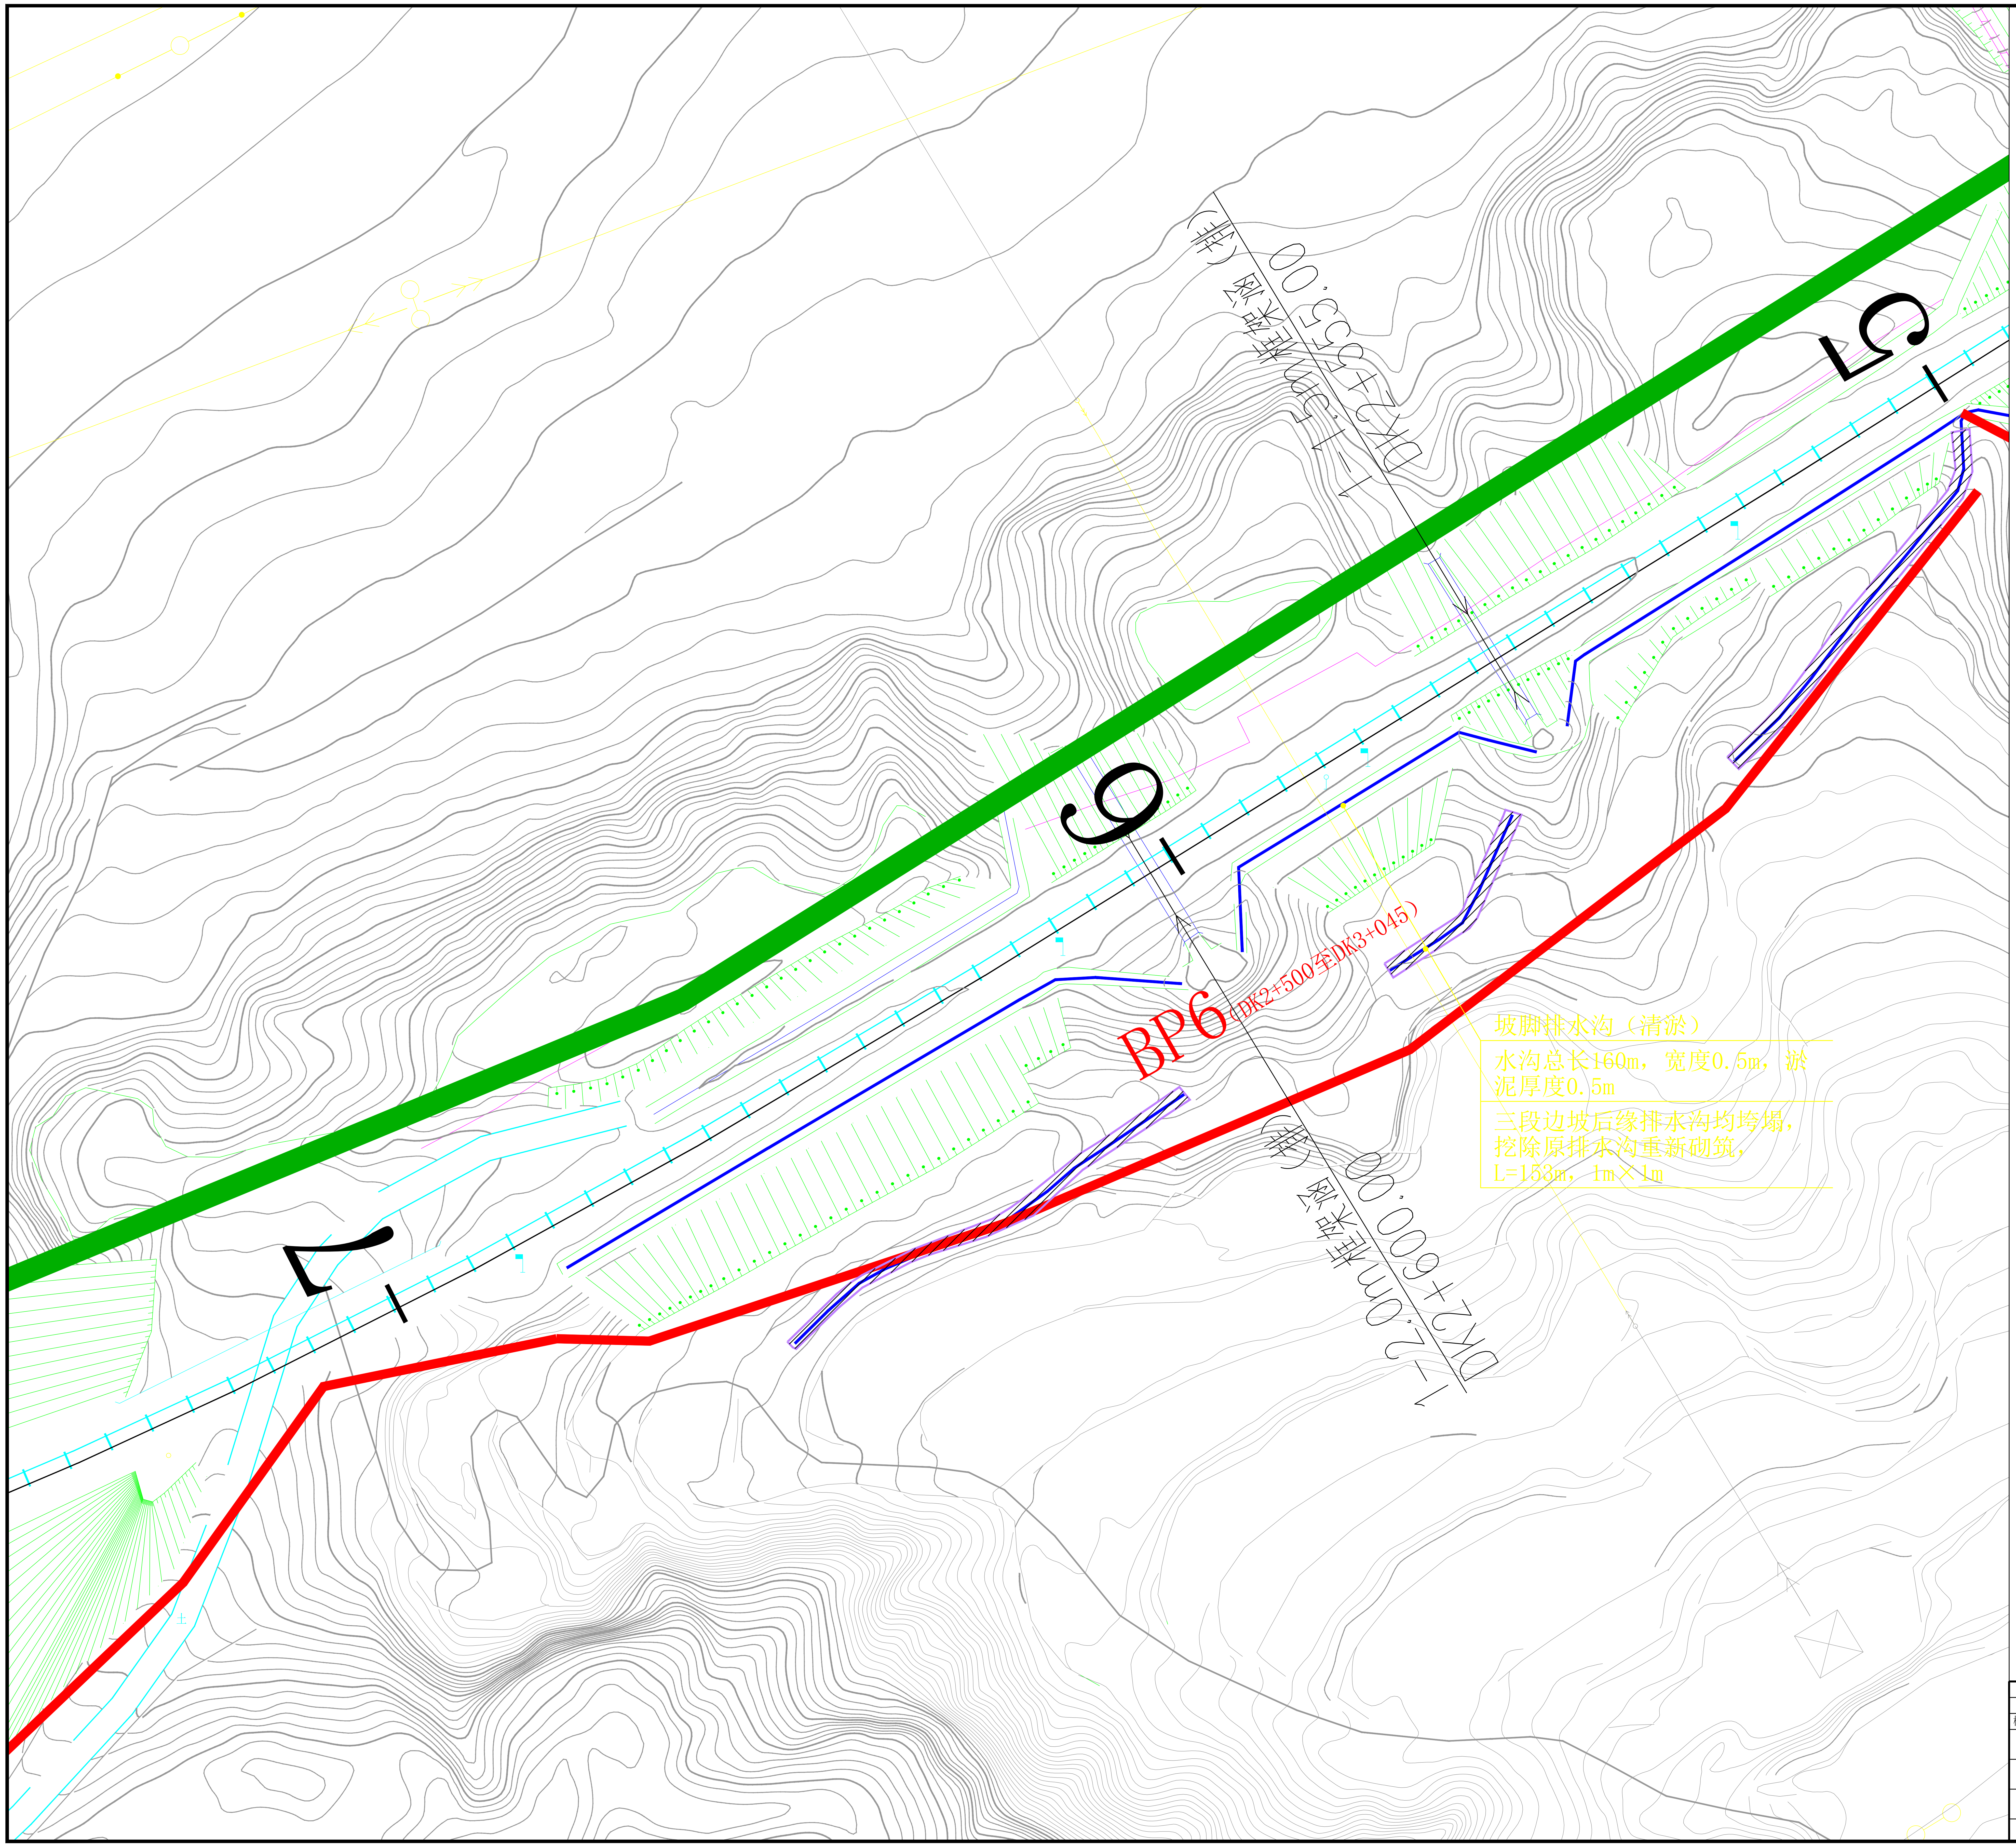

坡脚排水沟（清淤）

水沟总长160m，宽度0.5m，淤泥厚度0.5m

三段边坡后缘排水沟均垮塌，挖除原排水沟重新砌筑，L=153m，1m×1m

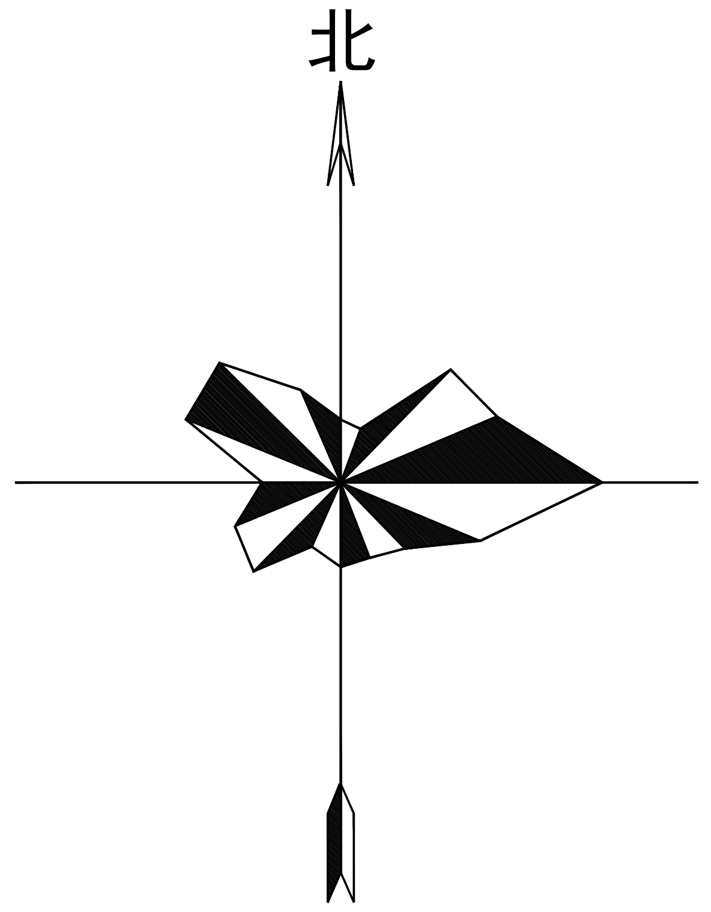

图 例：

BP1	边坡范围及编号
BP1—T1	塌陷治理区域及编号
	原状边坡示坡线
	新建截（排）水沟
	急流槽
	已有建、构筑物
	已有截（排）水沟
	涵洞
DK3	线路及公里标
	调查区范围

山西文龙中美环能科技股份有限公司
技术专用章

证书分类	资质等级	证书编号
煤炭行业（矿井）工程设计	甲级	A214001452
煤炭行业（选煤厂）工程设计	乙级	A214001459
建筑行业(建筑工程)工程设计	乙级	A214001459

标记	数量	修改者	批准者	日期	太原煤气化龙泉能源发展有限公司铁路沿线边坡维修处治工程	
设 计	郝剑	项目负责	郝剑		铁路专用线	S1424-1951(6)-01
检 查		总工程师			BP6（DK2+500至DK3+045）	共 3 页 规格 比例
审 定		总经理	沙涵			第 1 页 A1 1：500
2025年 10 月编制					总平面布置图	山西文龙中美环能科技股份有限公司 （原名：山西文龙煤矿工程设计有限公司）