

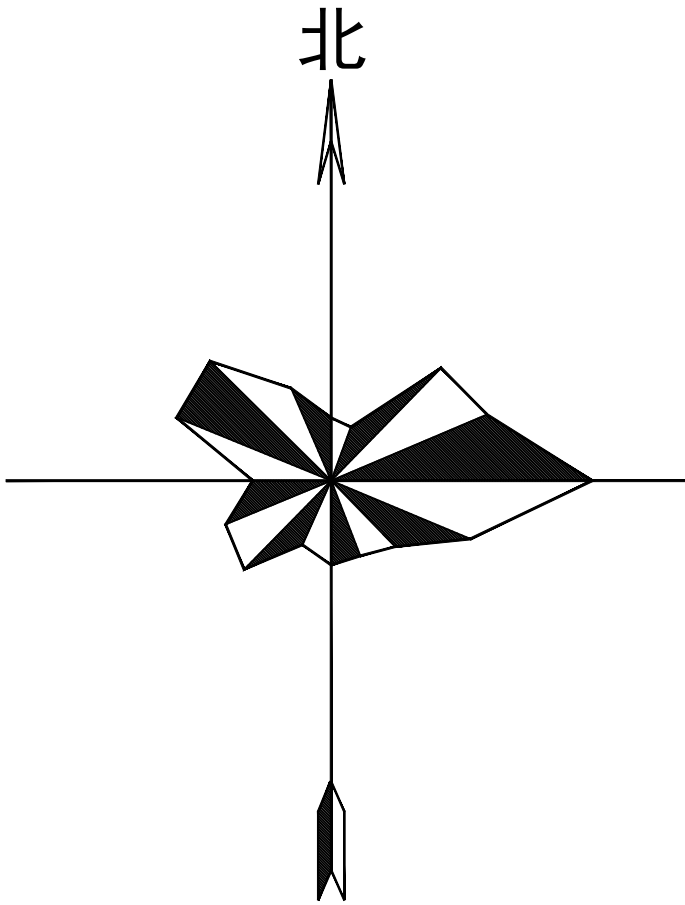
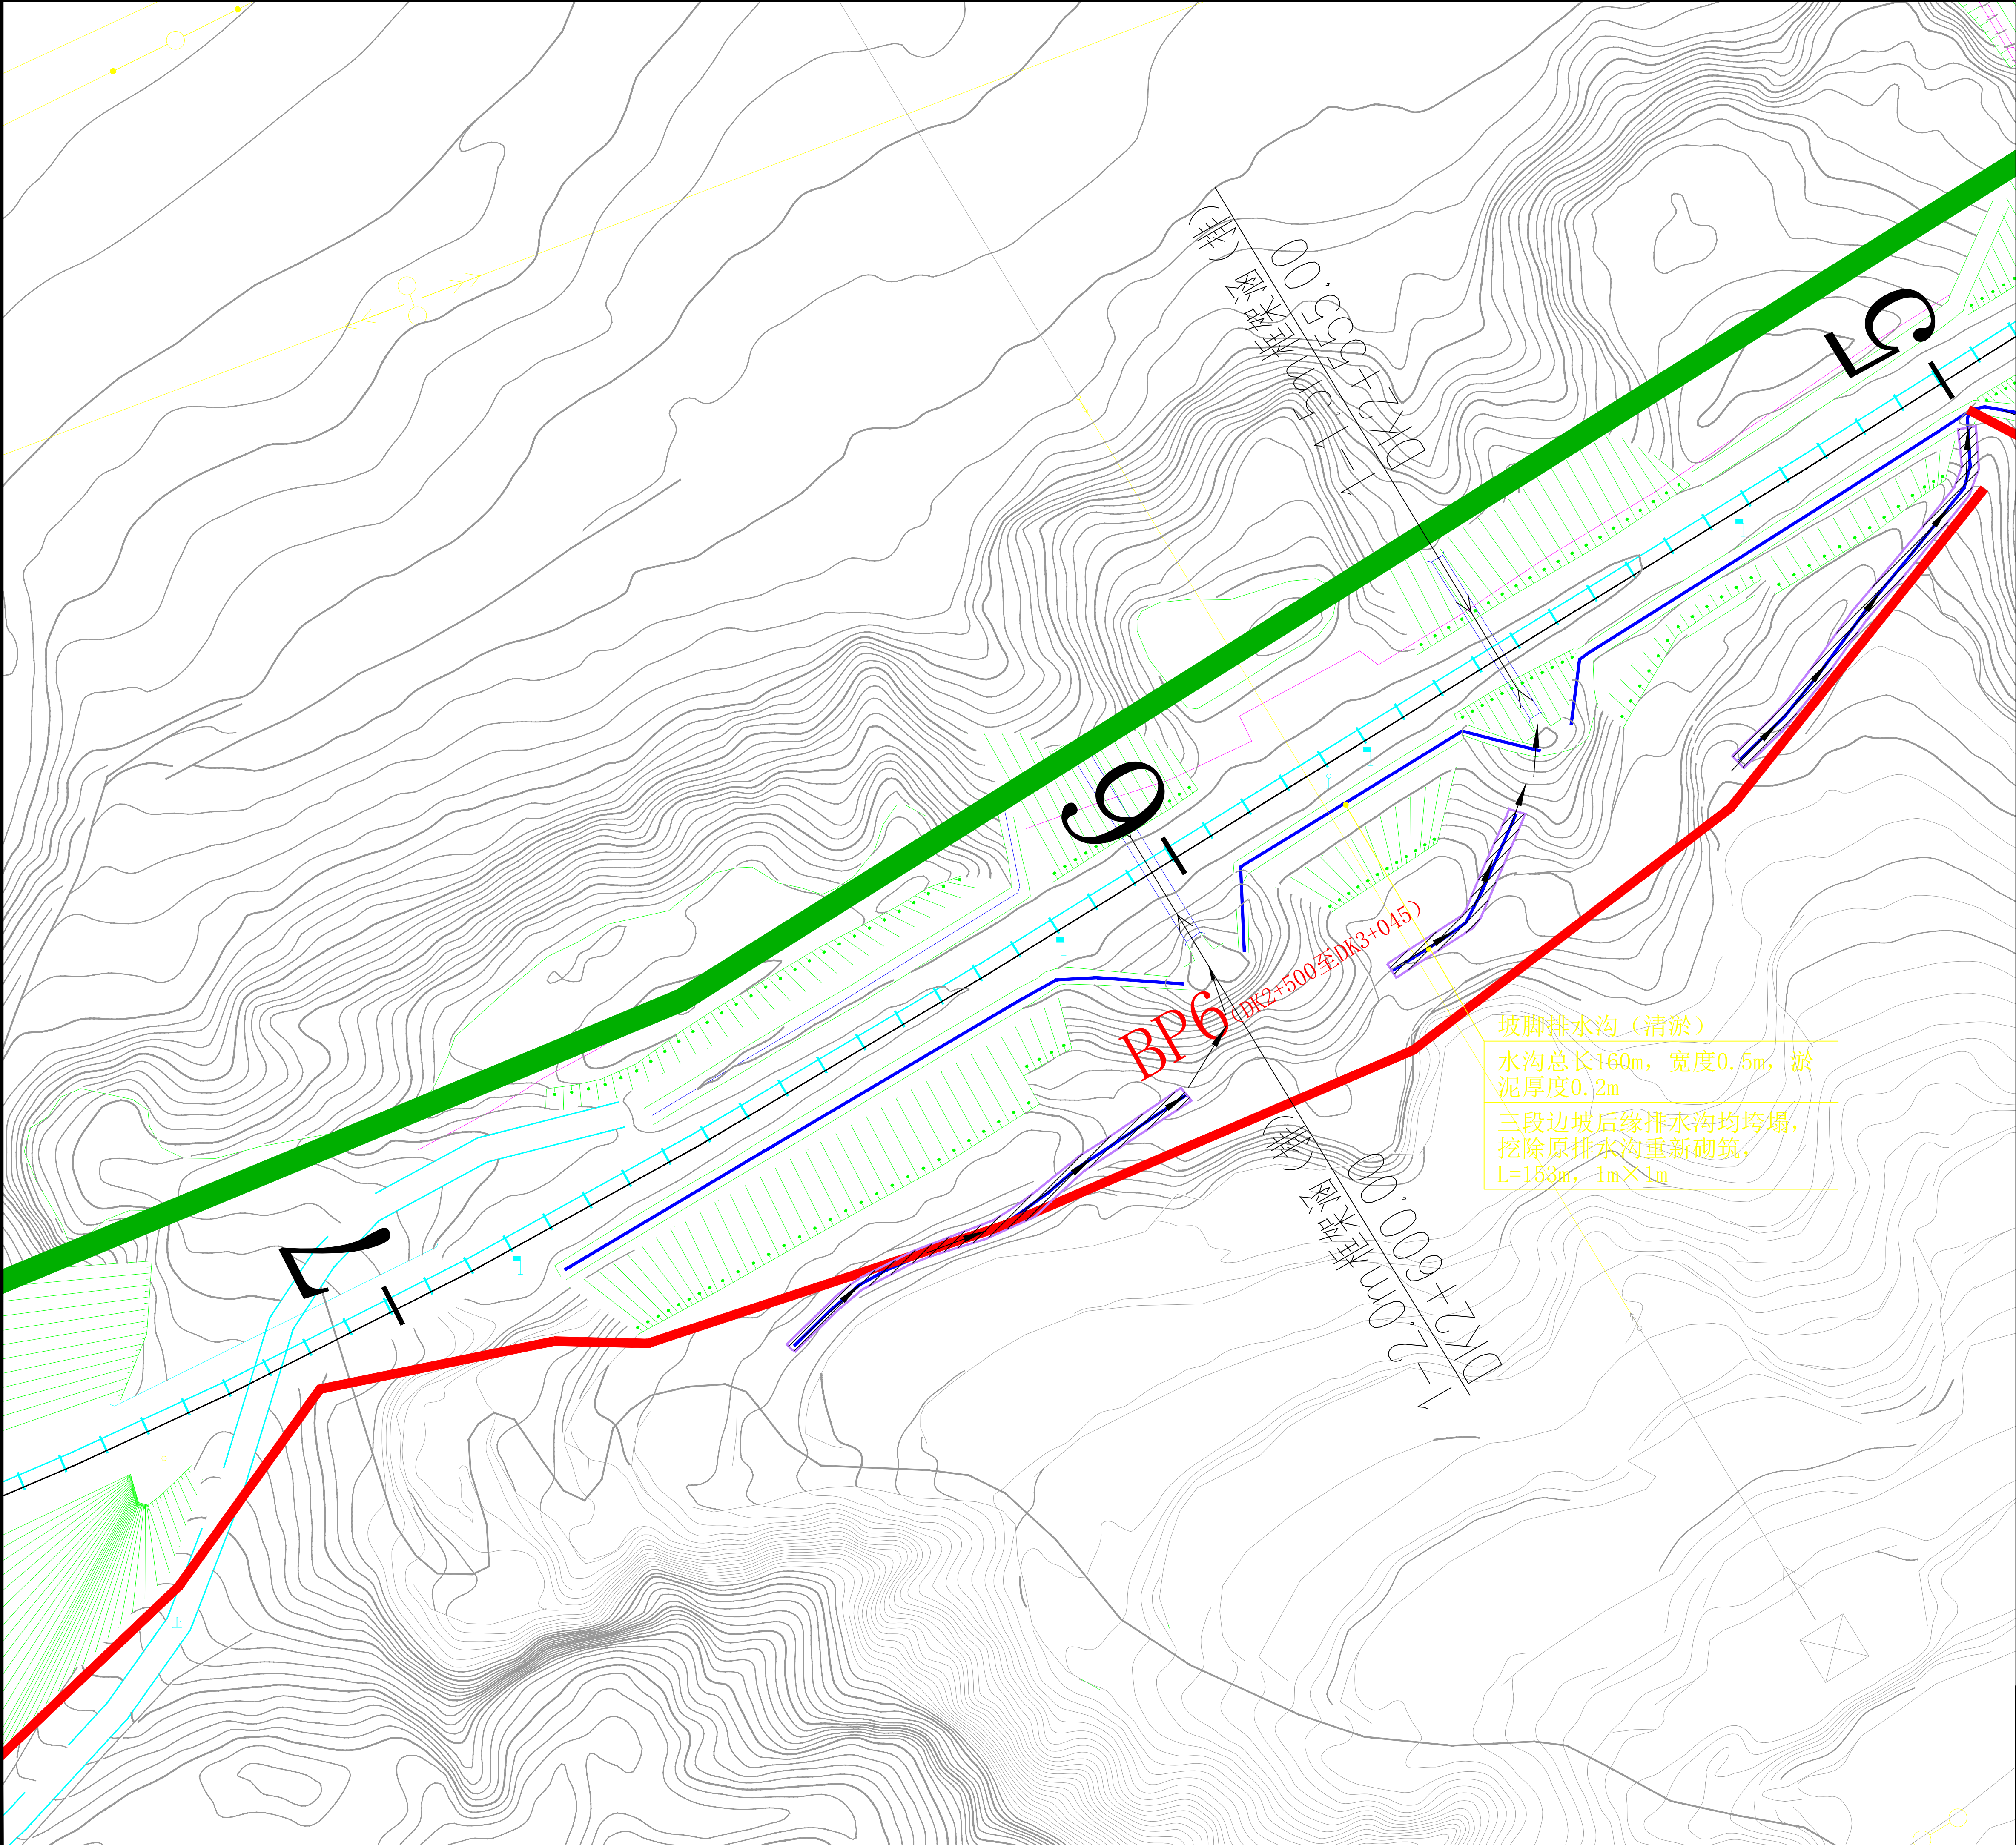


图 例：

- 新建截（排）水沟
- 急流槽
- 已有截（排）水沟
- 涵洞
- 排水方向

说明：

- 排水系统设置遵循“分级拦截、分段疏导、快速排出、防止冲刷”的原则。
- 截水沟：坡顶、平台设置截水沟，拦截坡顶及平台上方及平台汇集的地表水流，防止水流直接冲刷边坡坡面，避免雨水渗入坡体。坡顶截水沟设置在坡顶以外3-5米处，各分级平台排水沟设置在平台的外侧。
- 急流槽：平台间设置急流槽，快速疏导坡面汇水。急流槽设置在坡面汇集处、平台转角处或相随陡峭处。
- 排水措施以已有排水沟清淤疏通为主，上下平台间增设急流槽连通。
- 急流槽布设位置可根据现场实际情况进行调整。
- 其他未尽事项严格按现行国家规范标准执行。

山西文龙中美环能科技股份有限公司					
技术专用章					
标记	数量	设计	审核	批准	日期
设计	审核	批准	日期	审核	批准
检查	审核	批准	日期	审核	批准
审定	审核	批准	日期	审核	批准
2025年 10 月编制				排水系统平面布置图	
				山西文龙中美环能科技股份有限公司	