


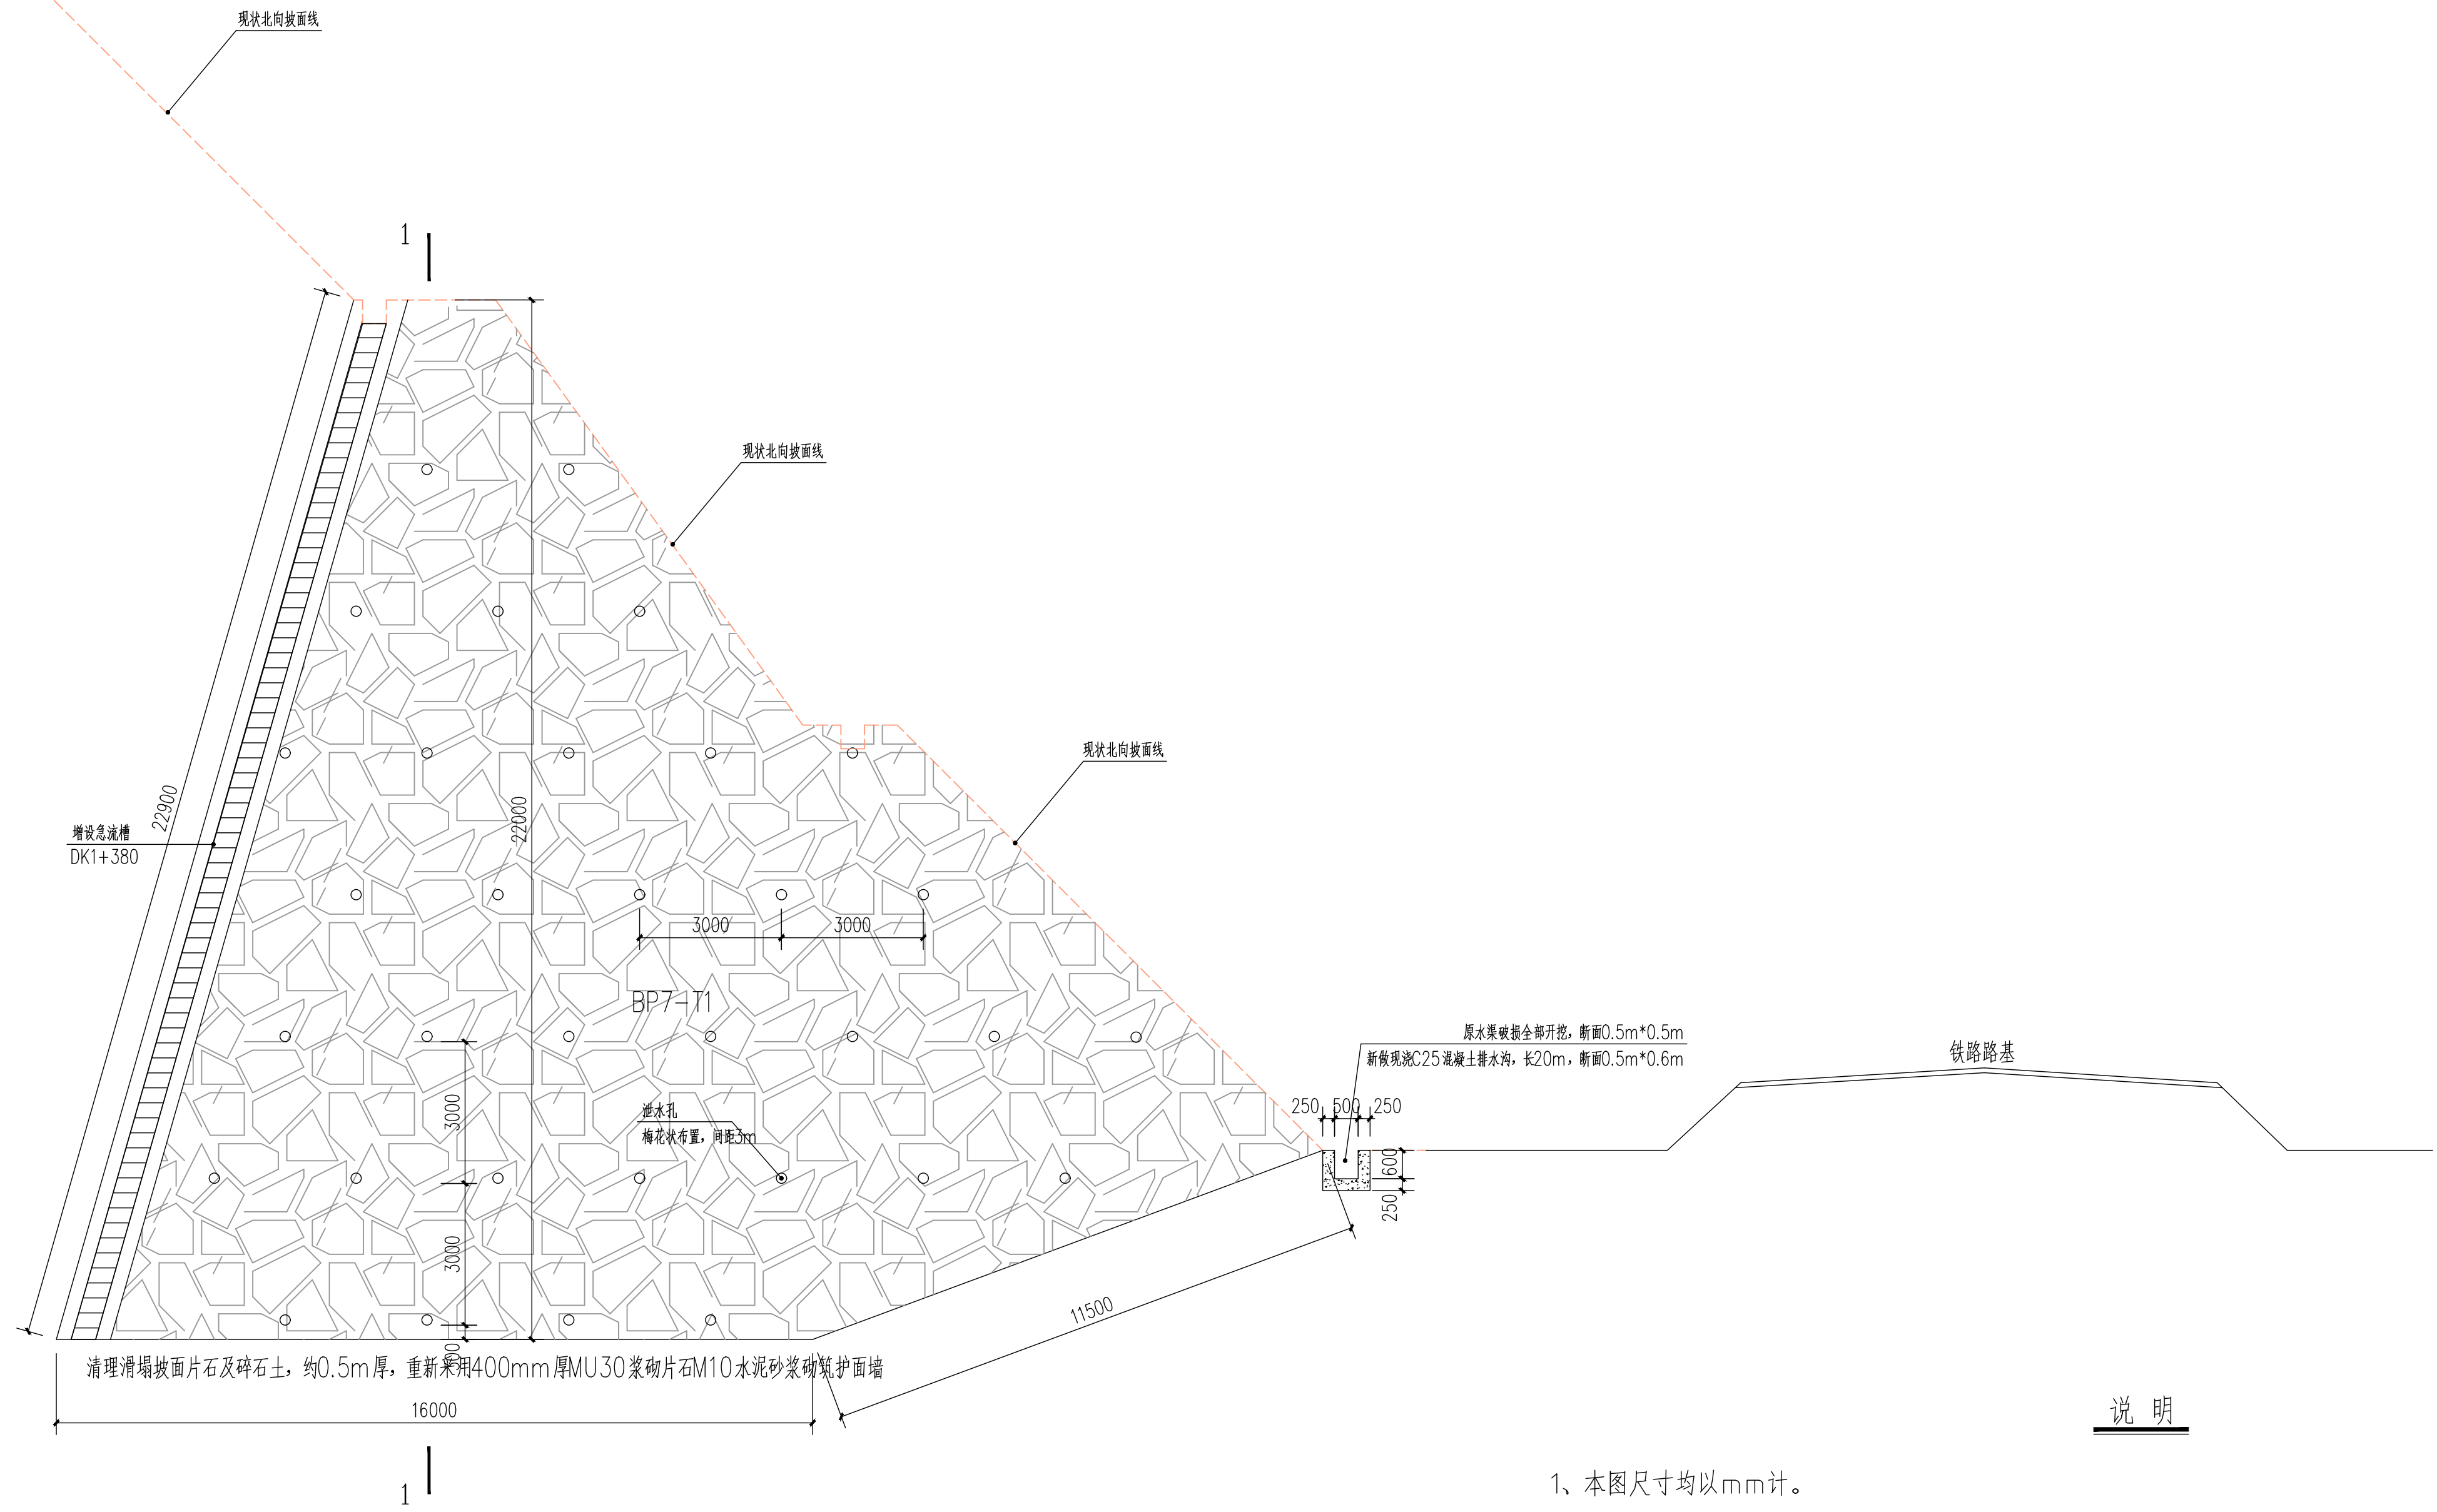



BP7边坡立面展开图 1:100  
此坡面面朝东。

说明

- 1、本图尺寸均以mm计。
- 2、BP7位于铁路专用线南部DK3+045m至DK3+090m段,现有南部边坡相邻东部坡面受降雨侵蚀影响,发生崩塌,该区域无支护;
- 3、东部边坡崩塌区域进行治理,清理滑塌面层后采用400厚MU30浆砌片石M10水泥砂浆砌筑护面墙;
- 4、南部边坡坡脚排水沟目前存在淤堵,清淤后可正常排水,总长度126m,淤泥厚度0.2m,宽度0.5m。
- 4、DK3+000段南侧水渠破损,长20m,全部开挖,开挖断面0.5m×0.5m,开挖后基底夯实,压实系数0.93,新做现浇C25混凝土排水沟(矩形),断面0.5m×0.6m;

|                  |    |           |      |    |                     |      |            |                            |          |
|------------------|----|-----------|------|----|---------------------|------|------------|----------------------------|----------|
| 山西文龙中美环能科技股份有限公司 |    |           |      |    |                     |      |            |                            |          |
| 技术专用章            |    |           |      |    |                     |      |            |                            |          |
| 标记               | 数量 | 修改者       | 审核者  | 日期 | 证书编号                | 资质等级 | 证书编号       | 原煤气化龙泉能源发展有限公司铁路沿线边坡维修处治工程 |          |
| 设计               | 1  | 设计        | 项目负责 | 审核 | 铁路专用线               |      |            | S1424-1951(7)-03           |          |
| 检查               | 1  | 煤炭行业工程师   | 审核   | 审核 | BP7-DK3+045至DK3+090 | 甲级   | A214001459 | 共5页                        | 规格比例     |
| 审定               | 1  | 煤炭行业高级工程师 | 审核   | 审核 | 边坡立面展开图             | 乙级   | A214001459 | 第3页                        | AI 1:100 |
| 2025年10月编制       |    |           |      |    |                     |      |            |                            |          |
| 山西文龙中美环能科技股份有限公司 |    |           |      |    |                     |      |            | 山西文龙中美环能科技股份有限公司           |          |
|                  |    |           |      |    |                     |      |            | (原名:山西文龙煤矿工程设计有限公司)        |          |



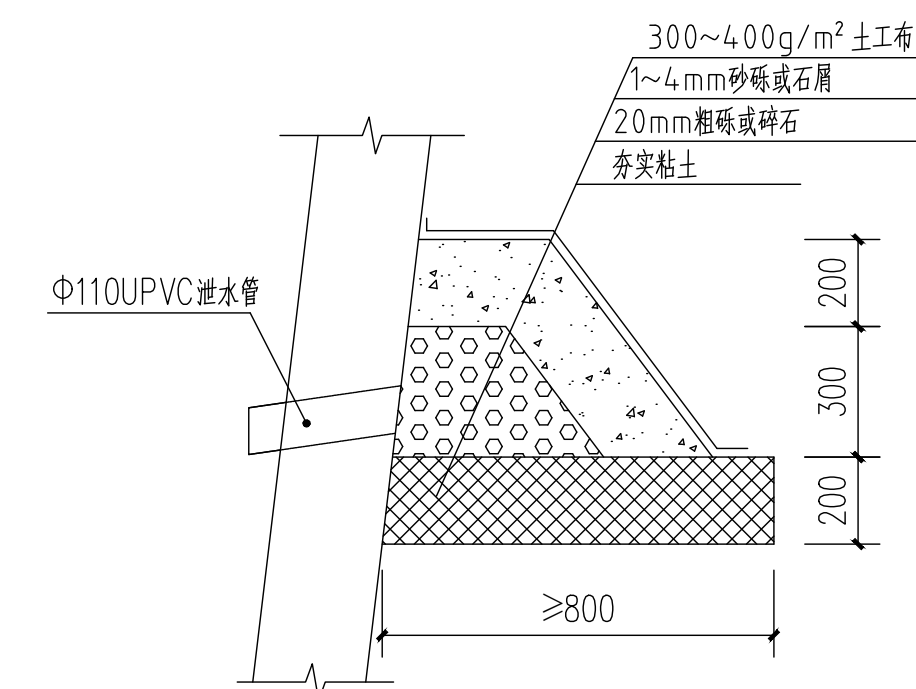
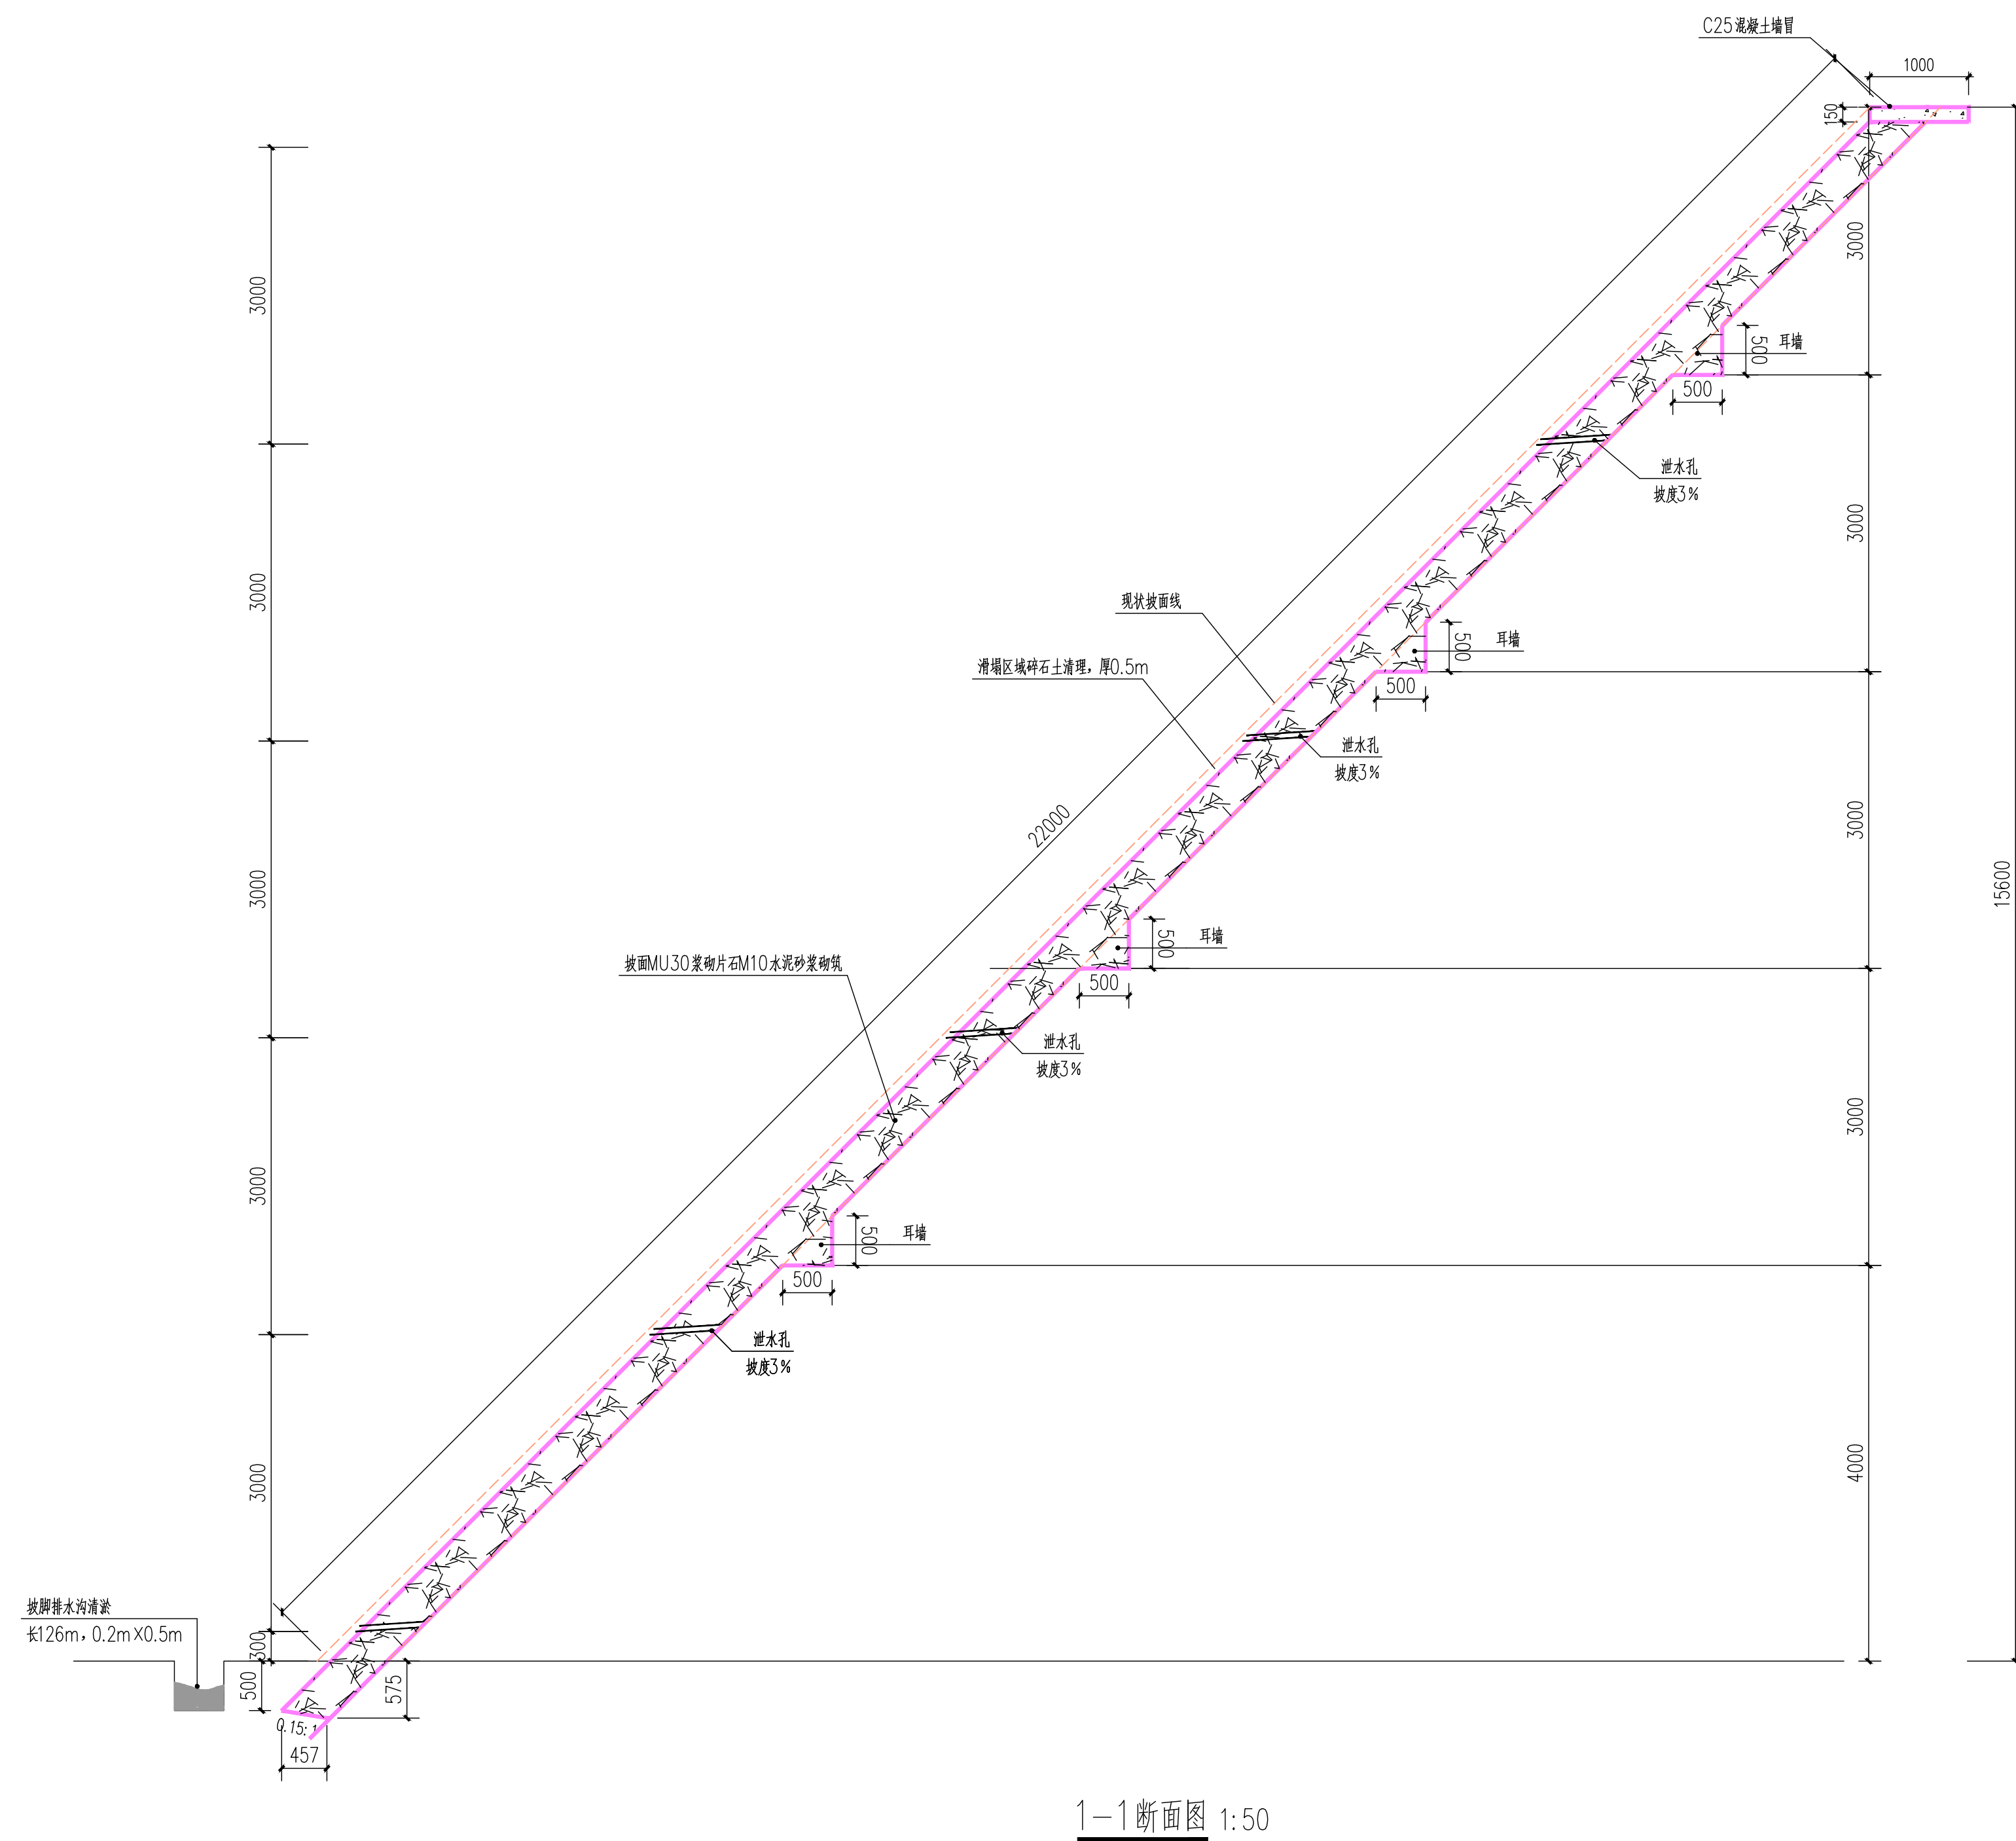


## 说 明

1. 实体护面墙的材料采用M10水泥砂浆砌筑MU30片石，地基承载力不小于150Kpa。
2. 实体护面墙墙身上预埋PVC管，位置见护面墙坡面布置图，呈梅花形交错布置。孔口大小直径为110mm，泄水孔后用碎石和沙砾作为反滤层，底层泄水孔距边沟顶面0.3m, 底层泄水孔下部设置粘土隔水层。
3. 护面墙施工必须紧贴坡面，墙身超挖部分应用C25混凝土砌筑，不得回填土；当实体护面墙高度为 $3\text{m} \leq H \leq 6\text{m}$ 时，墙背设一个耳墙； $H > 6\text{m}$ 时，墙背设两个耳墙。
4. 护面墙顶部应原土夯实，以免边坡水流冲刷，渗入墙后引起破坏。
5. 护面墙施工时各道工序应紧密衔接，连续施工，严禁爆破，以免坡面长期暴露或爆破震松造成边坡坍塌，护面墙基础应设置在稳定的地基上。
6. 修筑护面墙前，对所防护的边坡，应清除滑塌的片石及碎石土等，凹陷处可挖成错台；平台用M10水泥砂浆砌筑MU30片石，铺砌厚度250mm。
7. 本图尺寸标注均以毫米计。
8. 图中未详按相关规范执行。

|                           |    |    |    |    |      |                 |                  |  |  |
|---------------------------|----|----|----|----|------|-----------------|------------------|--|--|
| 山西文龙中美环能科技股份有限公司          |    |    |    |    |      |                 |                  |  |  |
| 技术专用章                     |    |    |    |    |      |                 |                  |  |  |
| 原煤气化龙泉能源发展有限公司铁路沿线边坡维修治工程 |    |    |    |    |      |                 |                  |  |  |
| 标记                        | 数量 | 修改 | 更改 | 日期 | 质量等级 | 证书编号            | SI424-1951(7)-04 |  |  |
| 设计                        | 张  | 张  | 张  | 张  | 合格   | 铁路专用线           | 共 5 页            |  |  |
| 检查                        | 张  | 张  | 张  | 张  | 合格   | DK3+045至DK3+090 | 规 格              |  |  |
| 审定                        | 张  | 张  | 张  | 张  | 合格   | 乙级              | 比 例              |  |  |
| 山西文龙中美环能科技股份有限公司          |    |    |    |    |      |                 | 第 4 页            |  |  |
| 山西文龙中美环能科技股份有限公司          |    |    |    |    |      |                 | 比 例              |  |  |
| 山西文龙中美环能科技股份有限公司          |    |    |    |    |      |                 | L: 100           |  |  |
| 山西文龙中美环能科技股份有限公司          |    |    |    |    |      |                 | 1-1 断面图          |  |  |
| 山西文龙中美环能科技股份有限公司          |    |    |    |    |      |                 | 山西文龙中美环能科技股份有限公司 |  |  |
| 山西文龙中美环能科技股份有限公司          |    |    |    |    |      |                 | 山西文龙中美环能科技股份有限公司 |  |  |



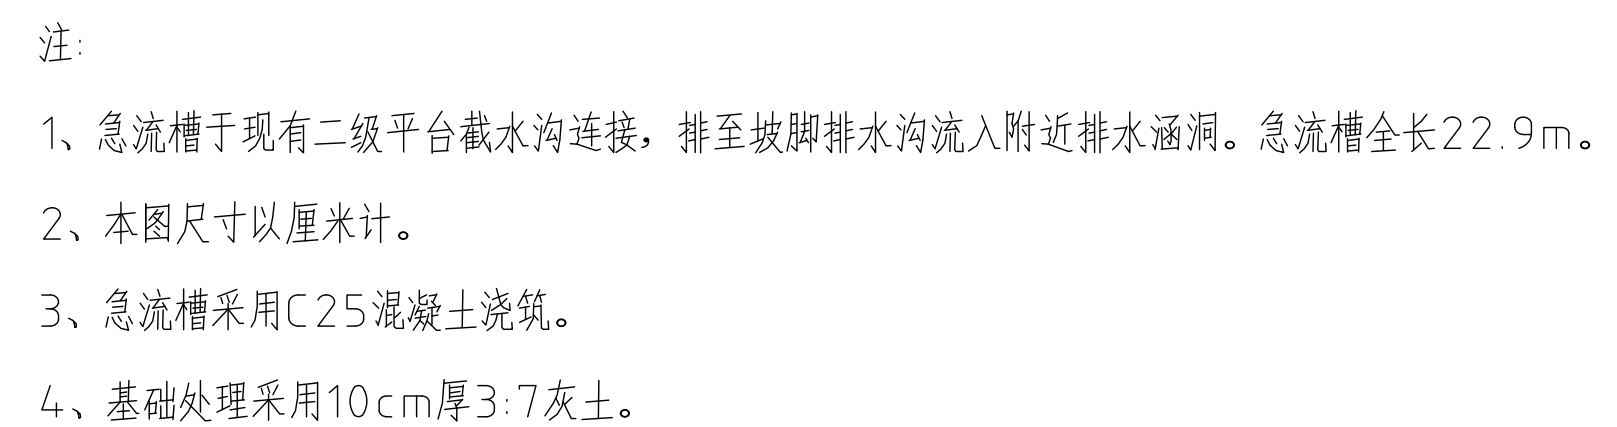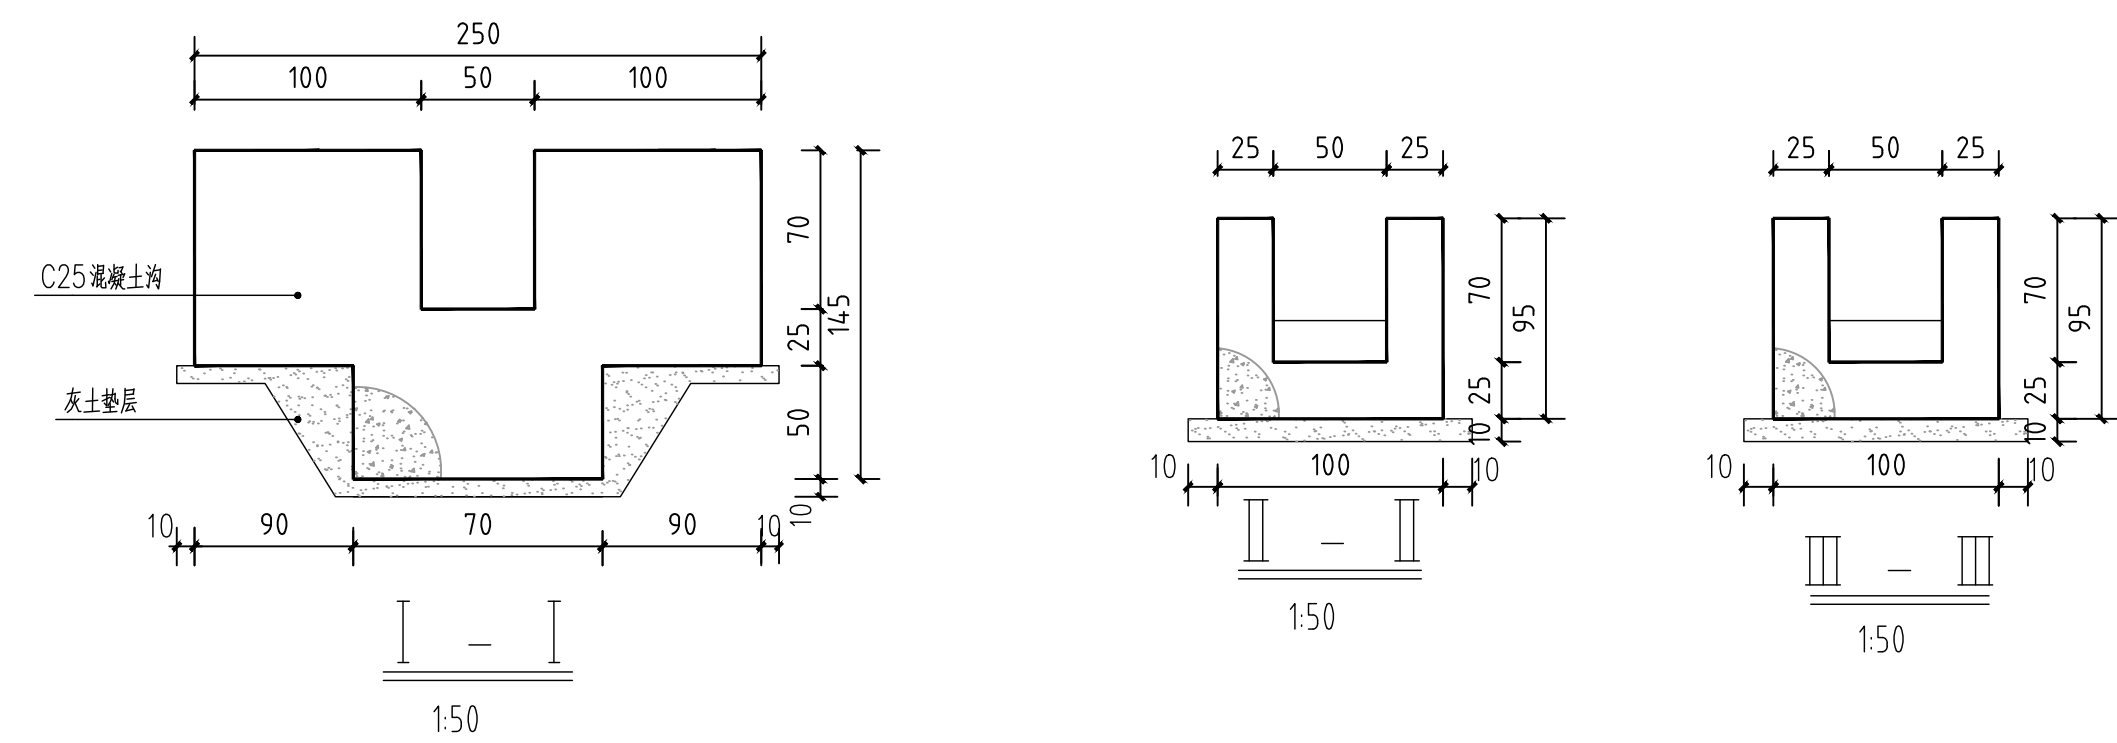

|                             |     |       |       |         |           |                                         |                    |        |  |
|-----------------------------|-----|-------|-------|---------|-----------|-----------------------------------------|--------------------|--------|--|
| 山西文龙中美环能科技股份有限公司            |     |       |       |         |           |                                         |                    |        |  |
| 技术专用章                       |     |       |       |         |           |                                         |                    |        |  |
| 太原煤气化龙泉能源发展有限公司铁路沿线边坡维修治理工程 |     |       |       |         |           |                                         |                    |        |  |
| 标 记                         | 数 量 | 修 改 号 | 版 本   | 日 期     | 质 量 等 级   | 证 书 编 号                                 | S1424-1951 (7) -05 |        |  |
| 设 计                         | 校 对 | 书 写   | 校 对   | 项 目 负 责 | 铁 路 专 用 线 | DP7 DK3+045~DK3+090                     | 共 5 页              |        |  |
| 检 查                         | 提 交 | 工 程 师 | 工 程 师 | 工 程 师   | 乙 类       | A210001458                              | 第 5 页              |        |  |
| 审 定                         | 审 定 | 审 定   | 审 定   | 审 定     | 乙 类       | A210001458                              | 比 例                |        |  |
| 2025年10月                    |     |       |       |         |           | 急流槽详图                                   |                    | 1: 100 |  |
| 山西文龙中美环能科技股份有限公司            |     |       |       |         |           | 山西文龙中美环能科技股份有限公司<br>(原名：山西文龙煤矿工程设计有限公司) |                    |        |  |