

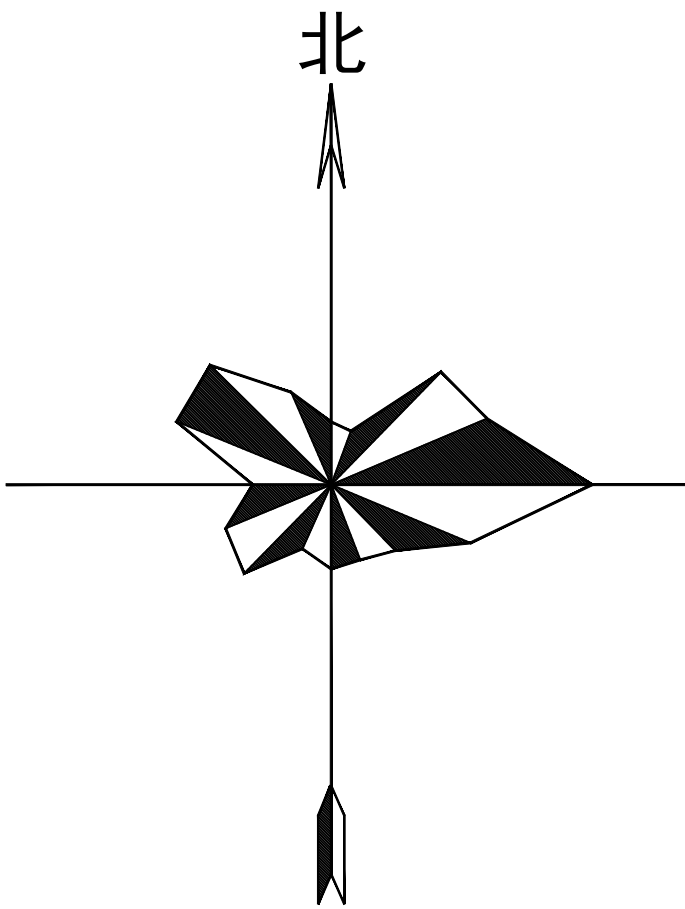
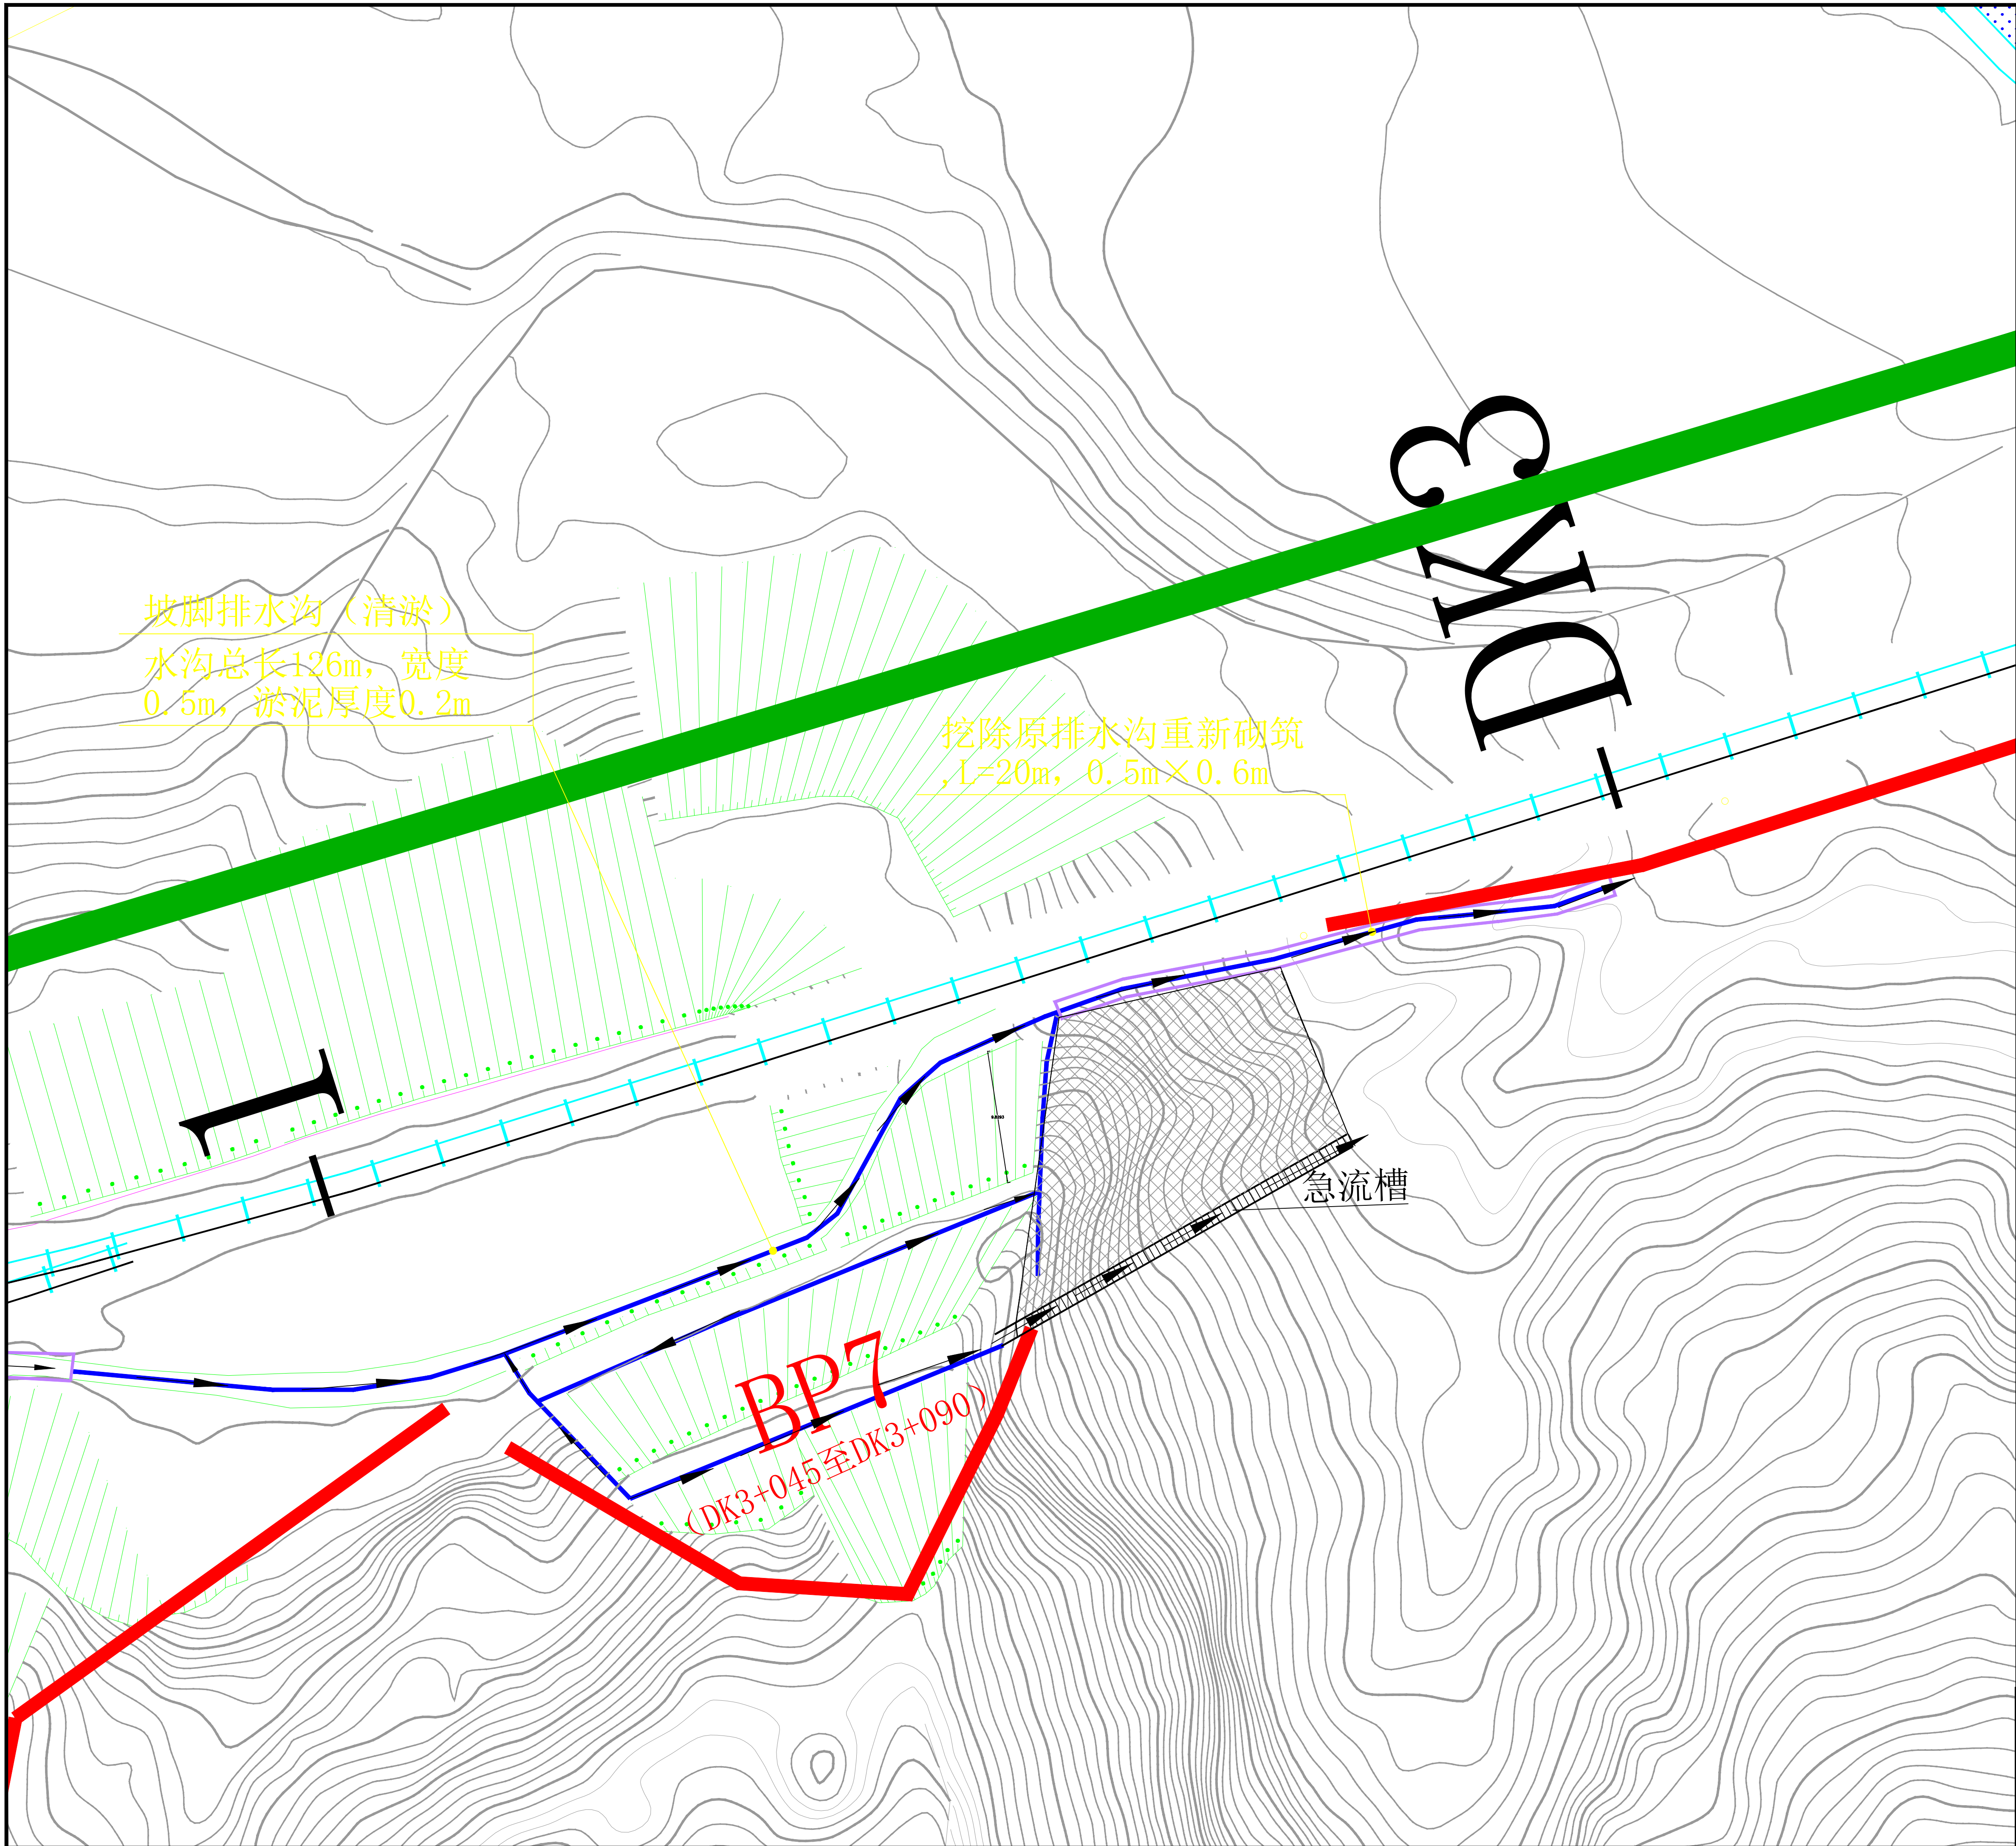


图 例:

- 新建截（排）水沟
- 急流槽
- 已有截（排）水沟
- 涵洞
- 排水方向

- 说明:
- 排水系统设置遵循“分级拦截、分段疏导、快速排出、防止冲刷”的原则。
 - 截水沟：坡顶、平台设置截水沟，拦截坡顶及平台上方及平台汇集的地表水流，防止水流直接冲刷边坡坡面，避免雨水渗入坡体。坡顶截水沟设置在坡顶以外3-5米处，各分级平台排水沟设置在平台的外侧。
 - 急流槽：平台间设置急流槽，快速疏导坡面汇水。急流槽设置在坡面汇集处、平台转角处或相随陡峭处。
 - 排水措施以已有排水沟清淤疏通为主，上下平台间增设急流槽连通。
 - 急流槽布设位置可根据现场实际情况进行调整。
 - 其他未尽事项严格按现行国家规范标准执行。

山西文龙中美环能科技股份有限公司									
太原燃气化龙泉能源发展有限公司铁路沿线边坡维修处治工程									
标记	数量	修改者	审核者	日期	技术专用章	证书编号	S1424-1951(7)-02		
设计	1	张明	张明	2025.10.10	铁路专用线	铁路专用线	共 5 页	规 格	比 例
检查	1	张明	张明	2025.10.10	BP7 (DK3+045至DK3+090)	BP7 (DK3+045至DK3+090)	第 2 页	A1	1: 500
审定	1	张明	张明	2025.10.10	排水系统平面布置图	排水系统平面布置图	山西文龙中美环能科技股份有限公司 (原名: 山西文龙矿冶工程有限公司)		