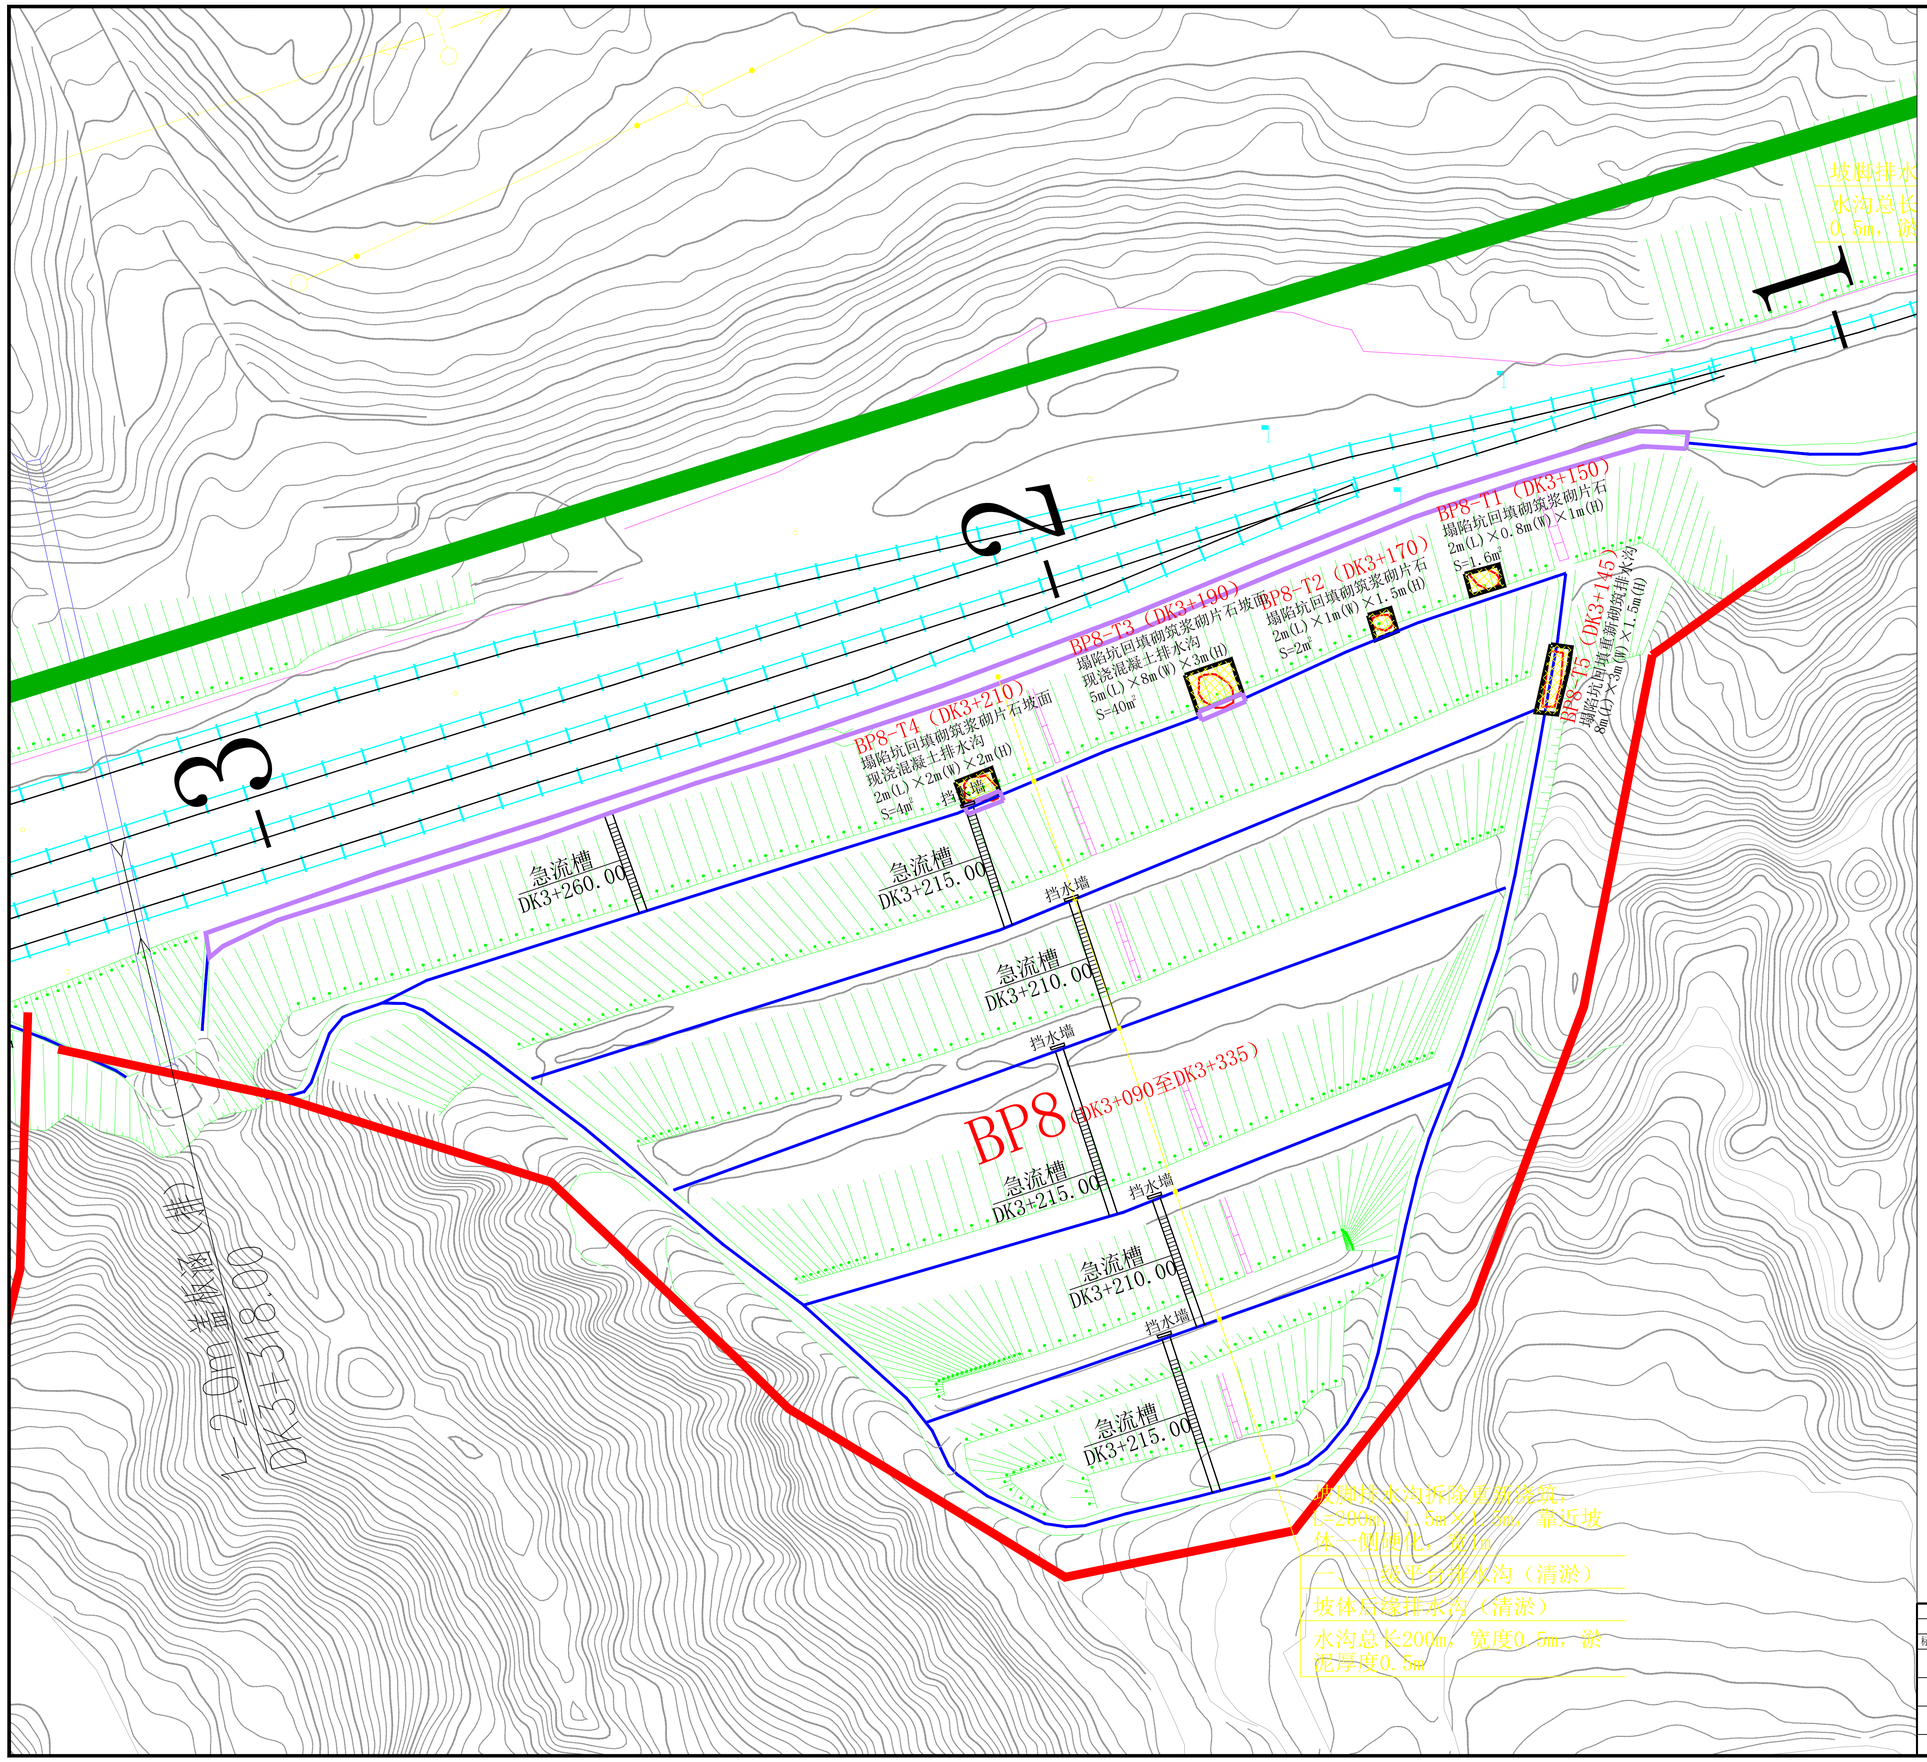

山西文龙中美环能科技股份有限公司

技术专用章

标记	数量	修改者	批准者	日期
设计				
检查				
审定				

2025年 10 月编制

大原煤气化龙泉能源发展有限公司铁路沿线边坡维修处治工程

铁路专用线

BP8（DK3+090至DK3+335）

总平面布置图

资质等级	证书编号
总经理	
总工程师	
项目负责人	
设计	
审核	
工程设计 乙级	A214001459

S1424-1951(8)-01		
共 6 页	规 格	比 例
第 1 页	A1	1：500

山西文龙中美环能科技股份有限公司
（原名：山西文龙煤矿工程设计有限公司）