

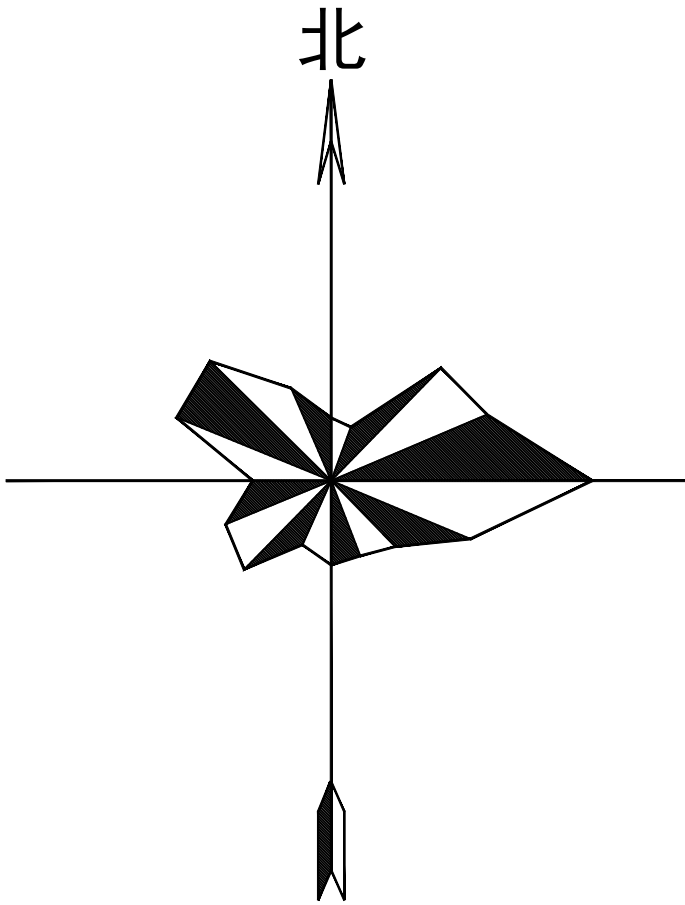
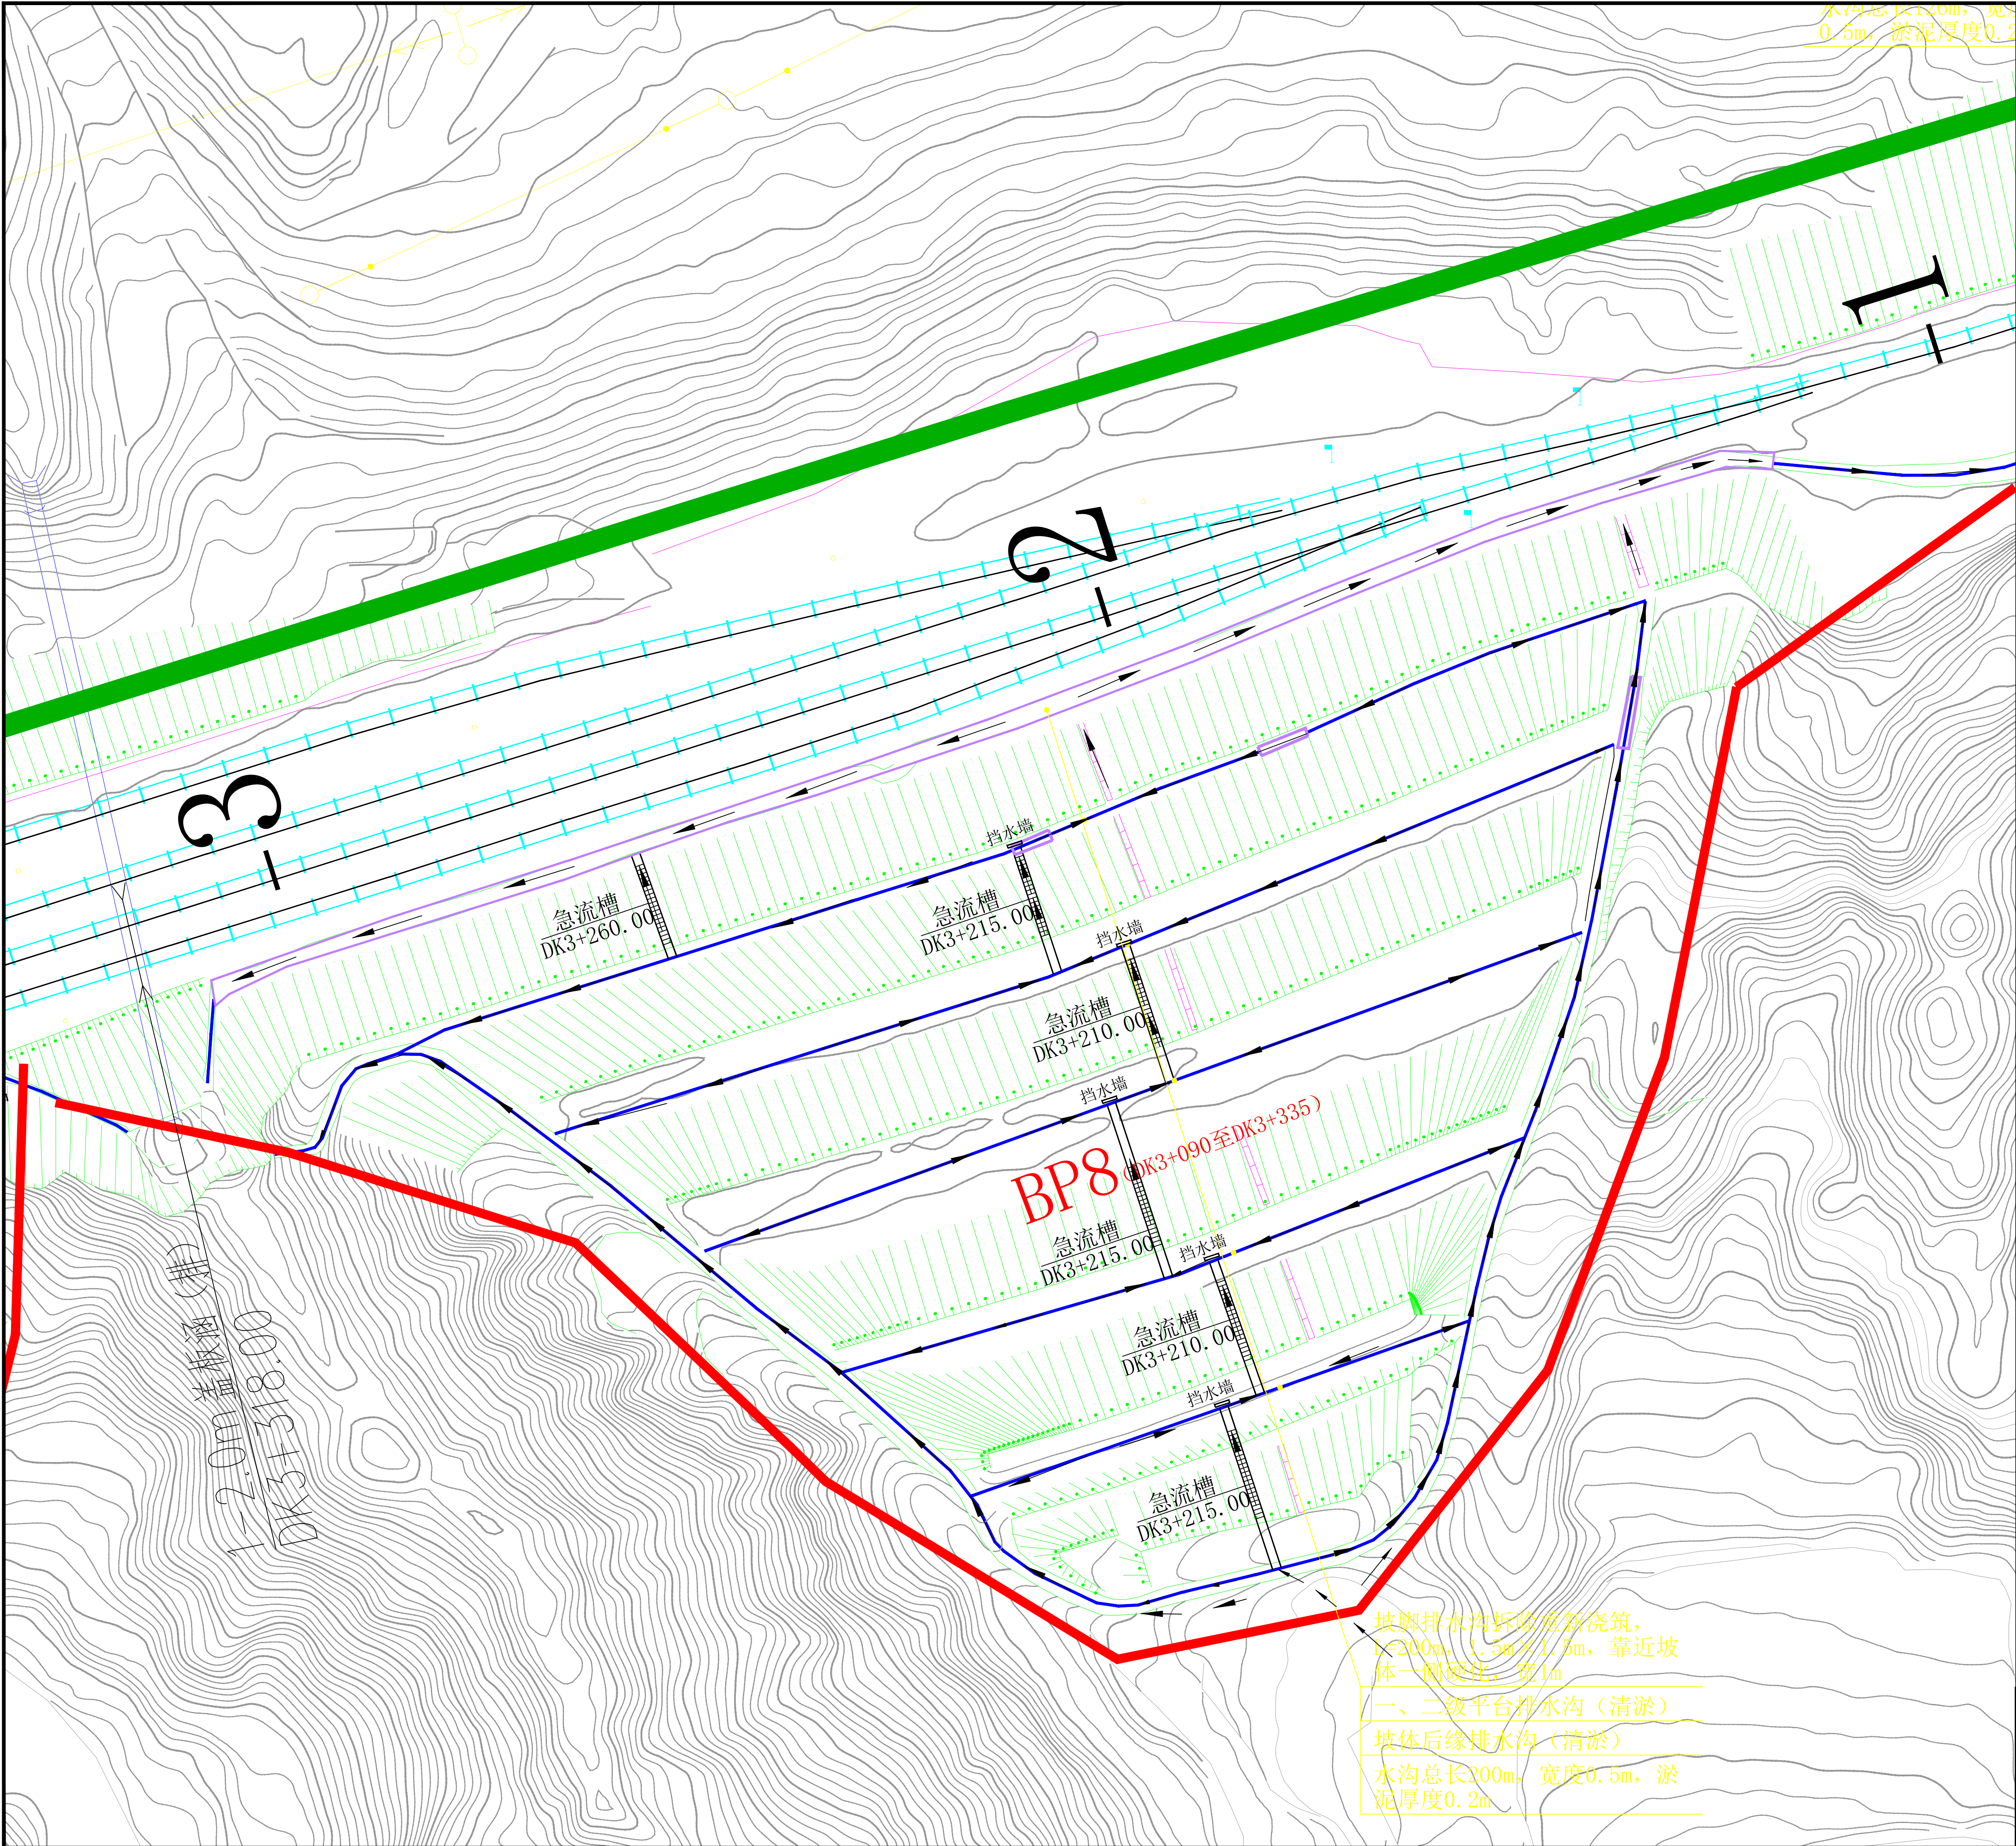


图 例：

- 新建截（排）水沟
- 急流槽
- 已有截（排）水沟
- 涵洞
- 排水方向

说明：

- 排水系统设置遵循“分级拦截、分段疏导、快速排出、防止冲刷”的原则。
- 截水沟：坡顶、平台设置截水沟，拦截坡顶及平台上方及平台汇集的地表水流，防止水流直接冲刷边坡坡面，避免雨水渗入坡体。坡顶截水沟设置在坡顶以外3-5米处，各分级平台排水沟设置在平台的外侧。
- 急流槽：平台间设置急流槽，快速疏导坡面汇水。急流槽设置在坡面汇水集中处、平台转角处或相随陡峭处。
- 排水措施以已有排水沟清淤疏通为主，上下平台间增设急流槽连通。
- 急流槽布设位置可根据现场实际情况进行调整。
- 其他未尽事项严格按现行国家规范标准执行。

山西文龙中美环能科技股份有限公司									
技术专刊									
标记	数量	修改者	批准者	日期	工程名称	设计	审核	校核	备注
设	计	不	同	不	同	不	同	不	同
检	查	煤	炭	行	业	总	工	程	师
审	定	煤	炭	行	业	建	筑	行	业
2025年 10 月编制					排水系统平面布置图				
共 6 页					S1424-1951(8)-02				
第 2 页					1: 500				
					山西文龙中美环能科技股份有限公司				