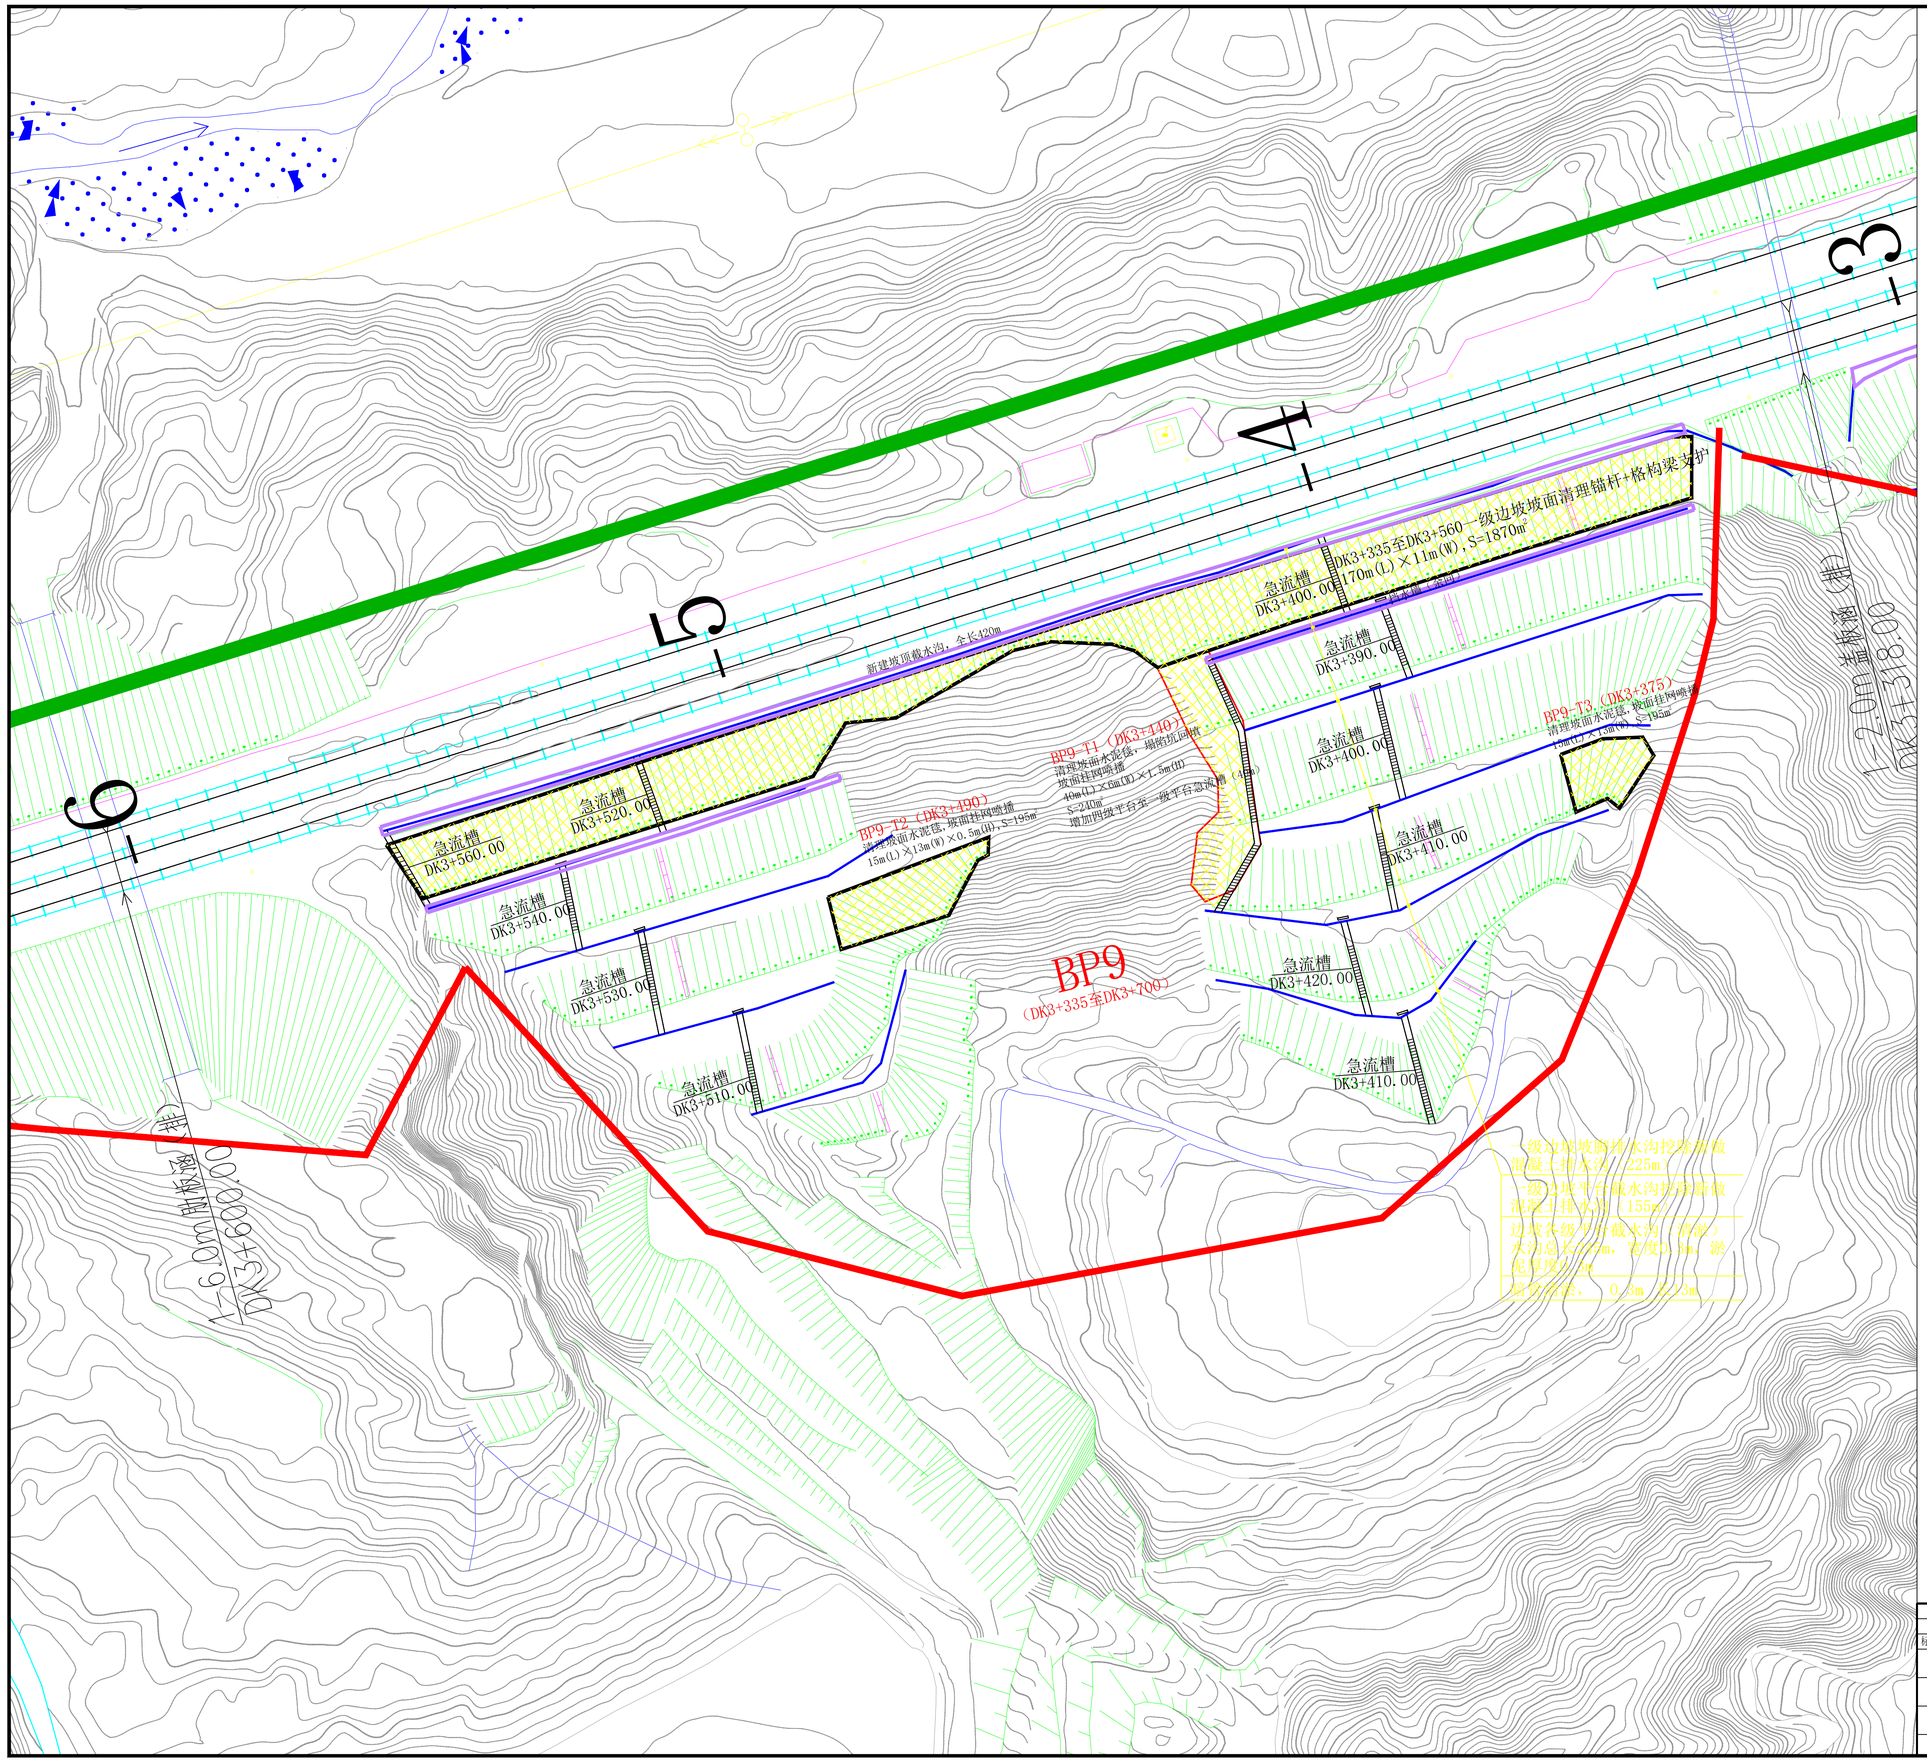


山西文龙中美环能科技股份有限公司

技术专用章

标记	数量	修改者	批准者	日期	灵石县煤气化龙泉能源发展有限公司铁路沿线边坡维修处治工程			
设计			项目负责		煤炭行业（选煤）甲级	证书编号	S1424-1951(9)-01	
检查			总工程师		煤炭行业（选煤）工程设计 乙级	A214001459	共 8 页	规格 A1
审定			总经理		建筑行业（建筑）工程设计 乙级	A214001459	第 1 页	比例 1：500
2025年 10 月编制					铁路专用线 BP9（DK3+335至DK3+700） 总平面布置图		山西文龙中美环能科技股份有限公司（原名：山西文龙煤矿工程设计有限公司）	